
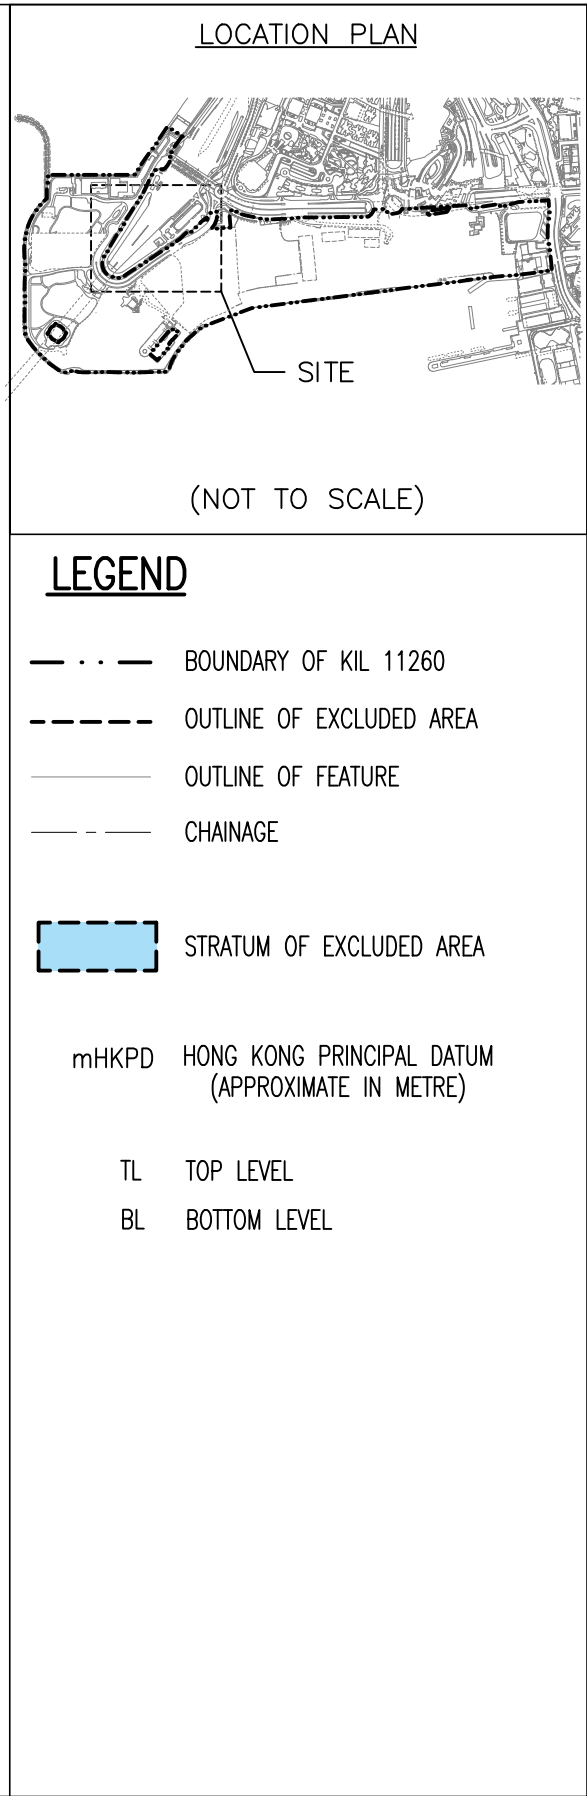
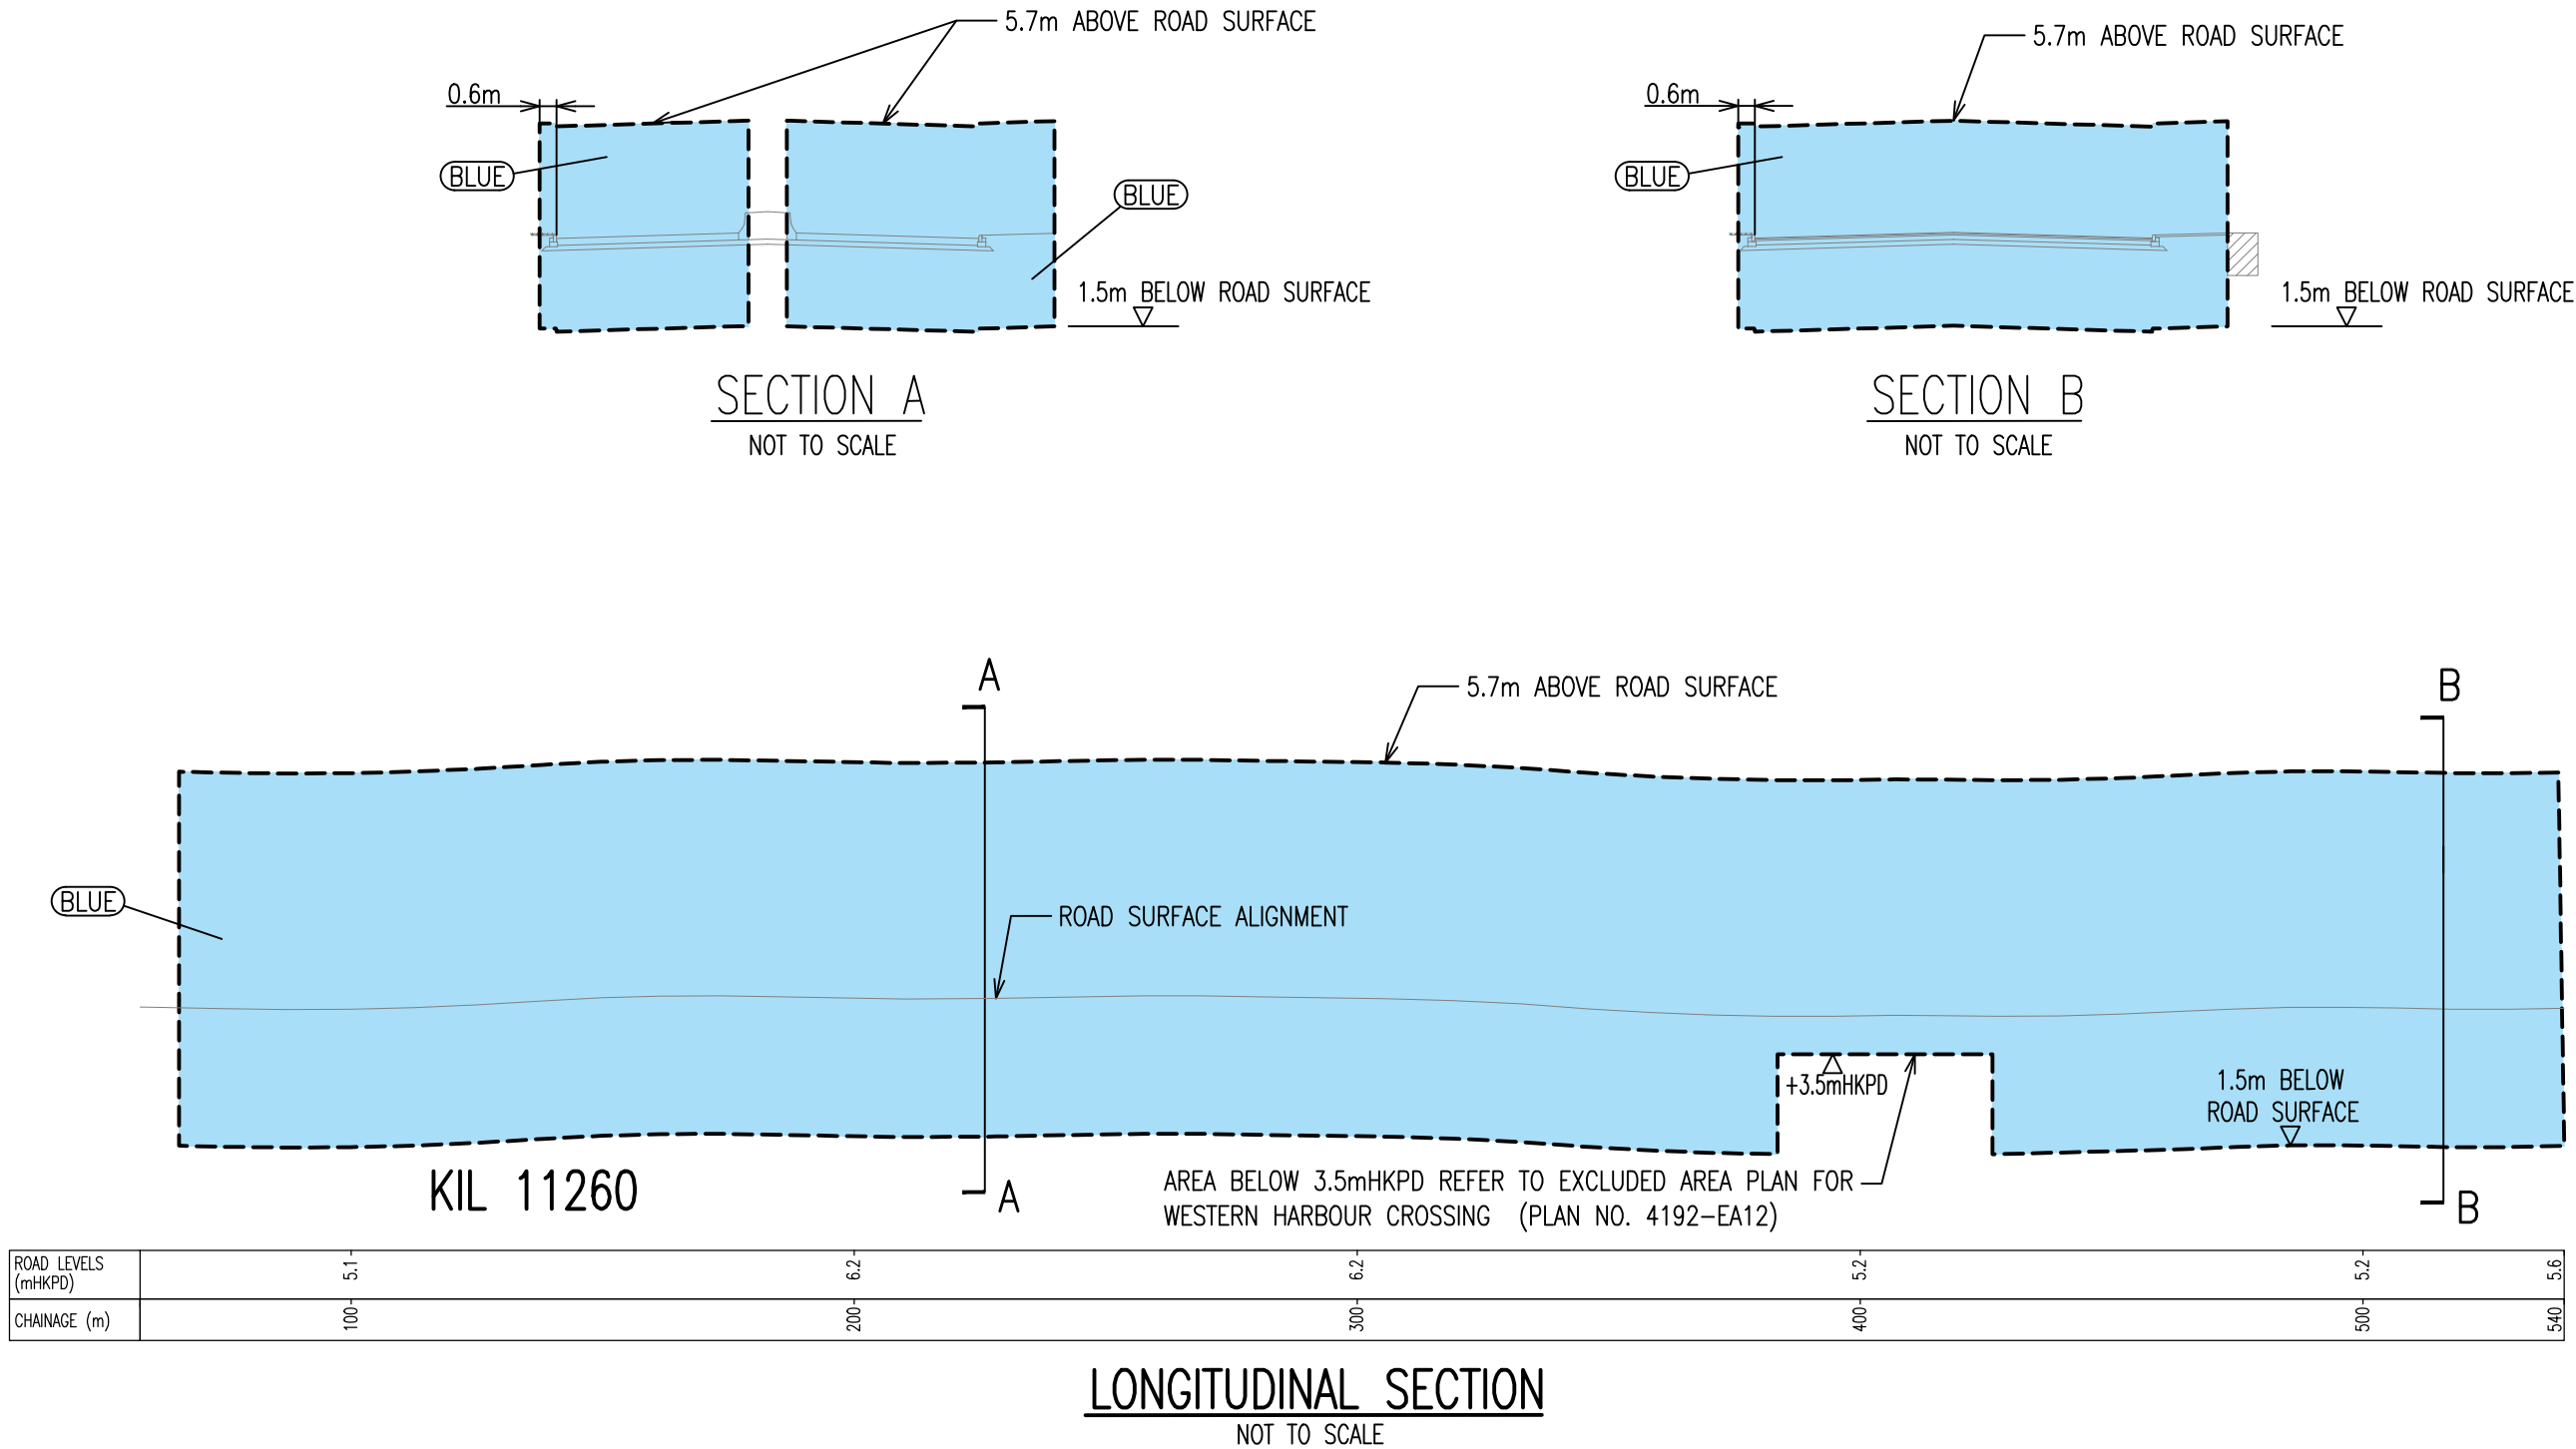


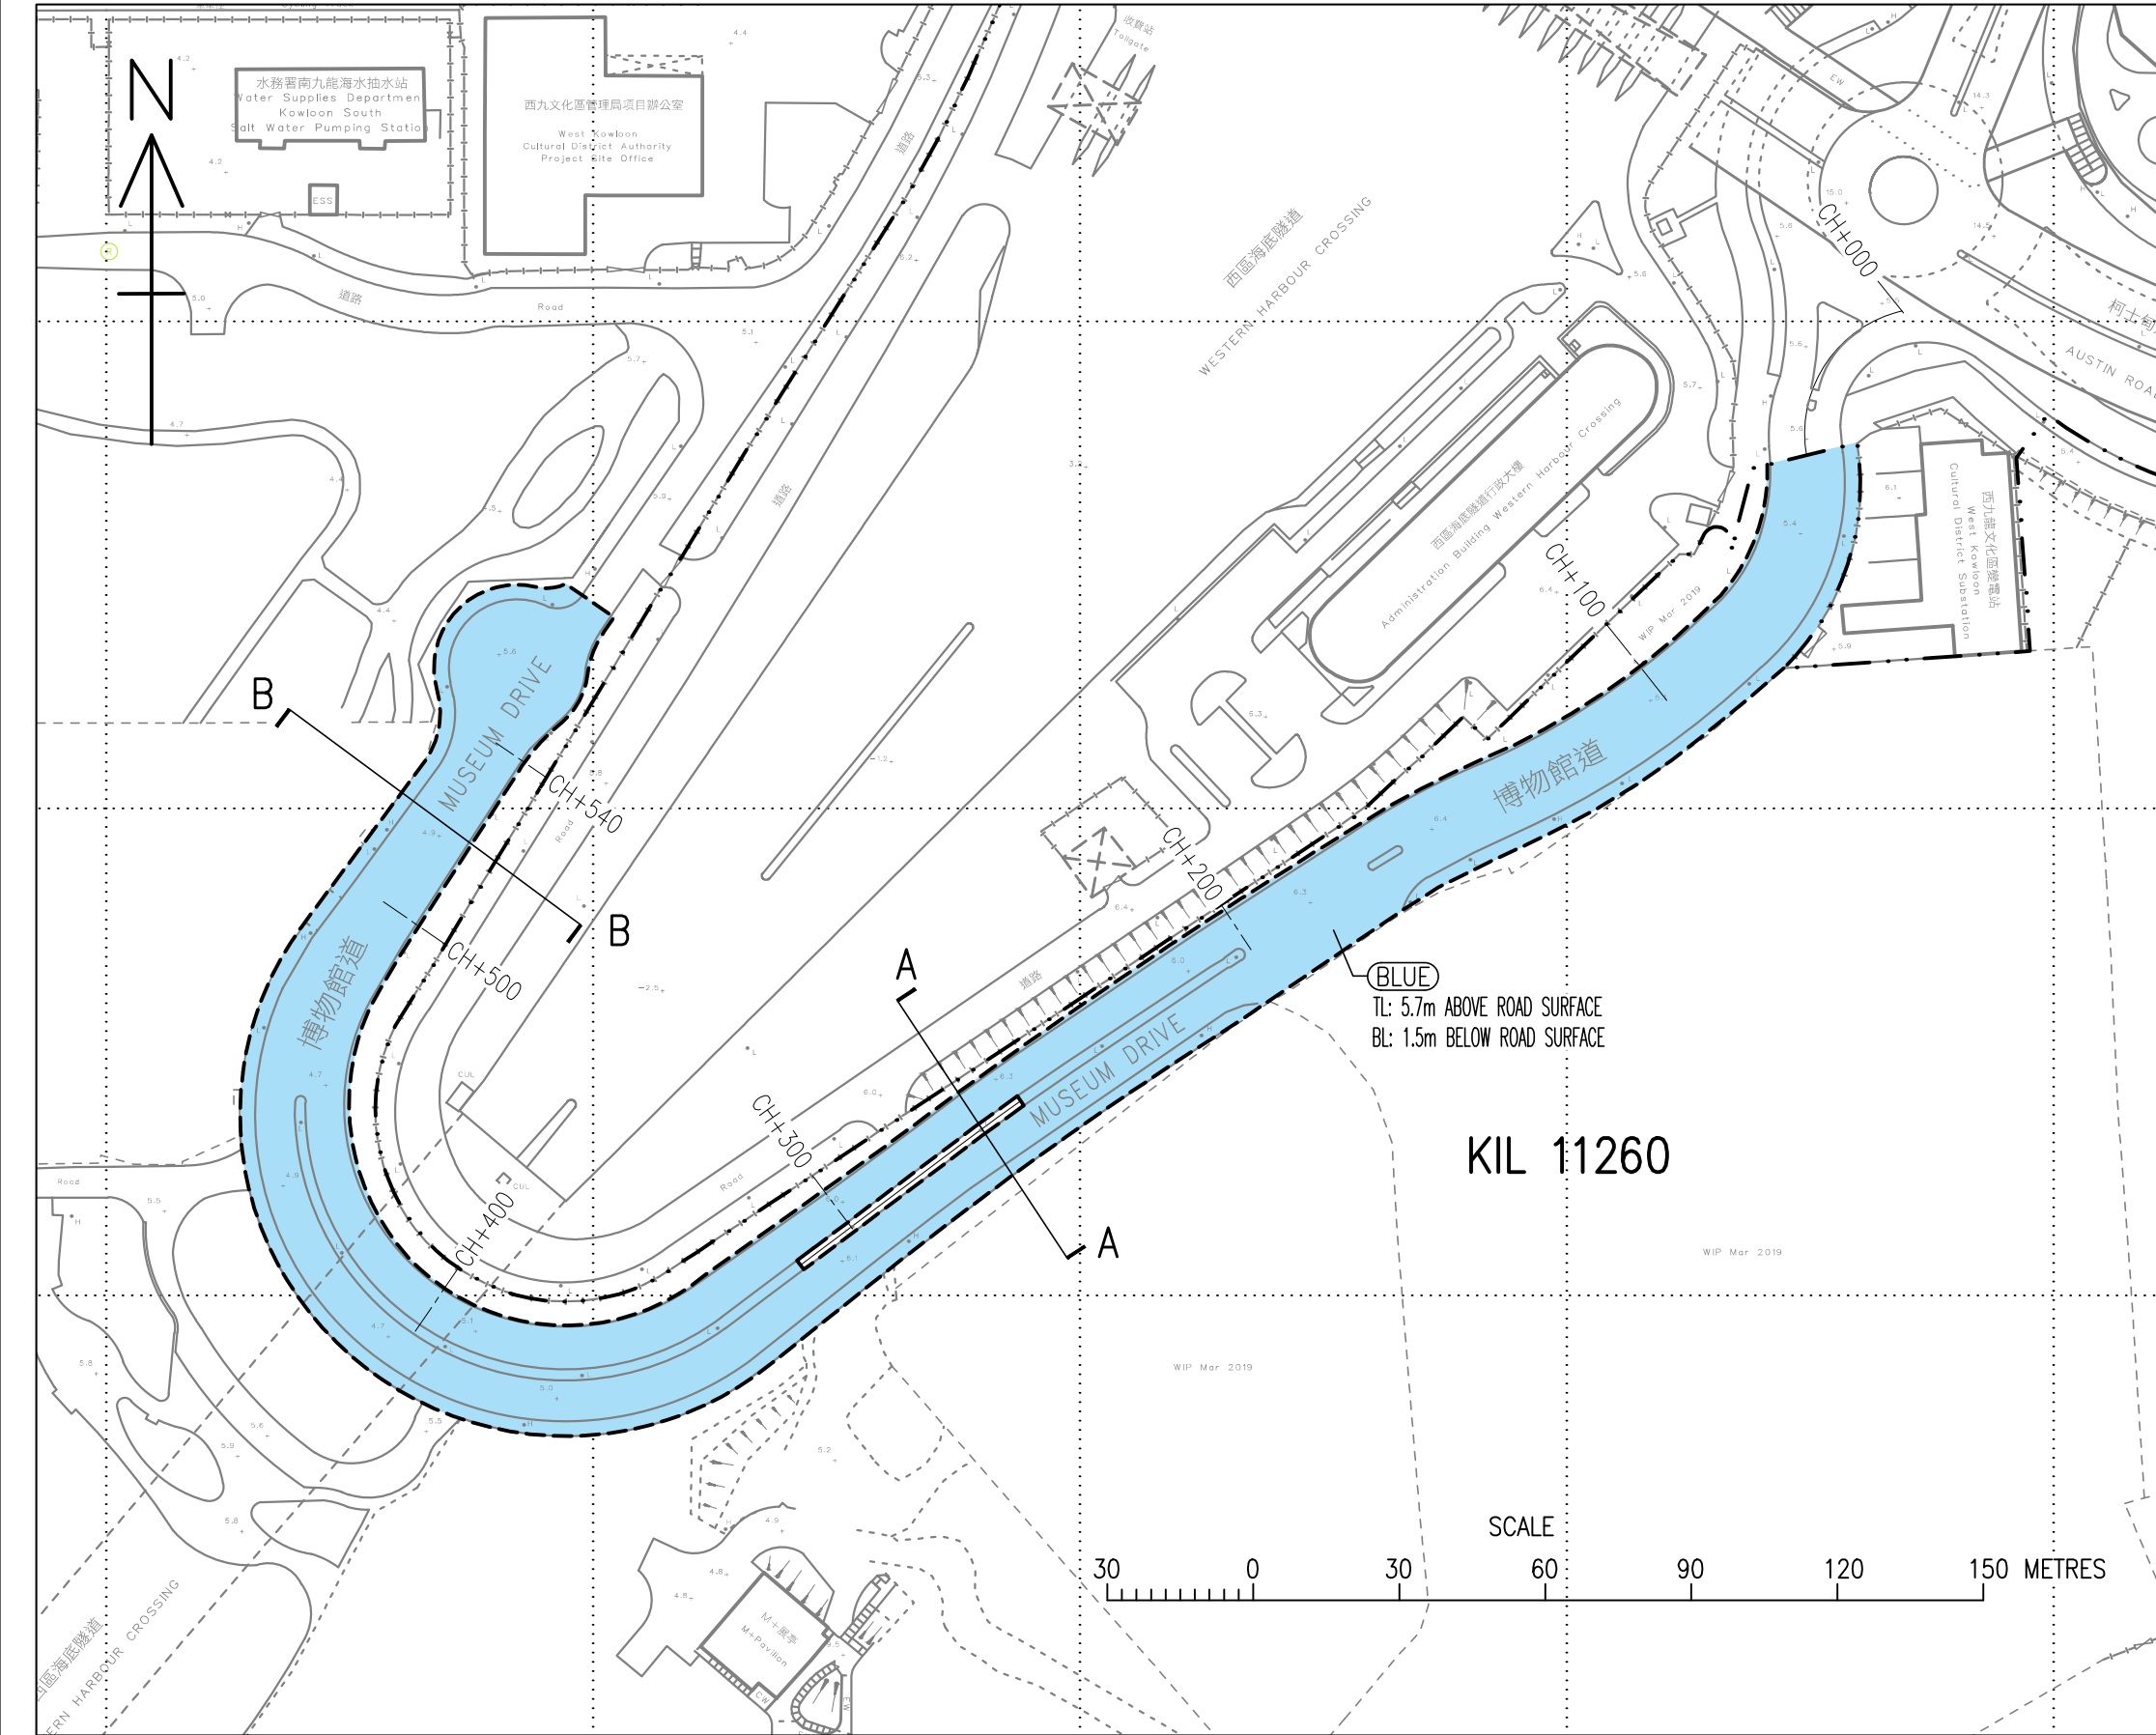

LAND MARKER (1980) H.K. Co., LTD.
標註測量(1980)香港有限公司
Survey District : KOWLOON
Survey Sheet : 11-NW-23D & 24C, 11-SW-3B & 4A
Plan No.: 4192-EA05

KOWLOON INLAND LOT No. 11260 EXCLUDED AREA FOR MUSEUM DRIVE

SIGNED BY

JOSEPH Y C WONG
AUTHORIZED LAND SURVEYOR FHKIS MRICS RPS(LS)
Date: 6 DECEMBER 2019