

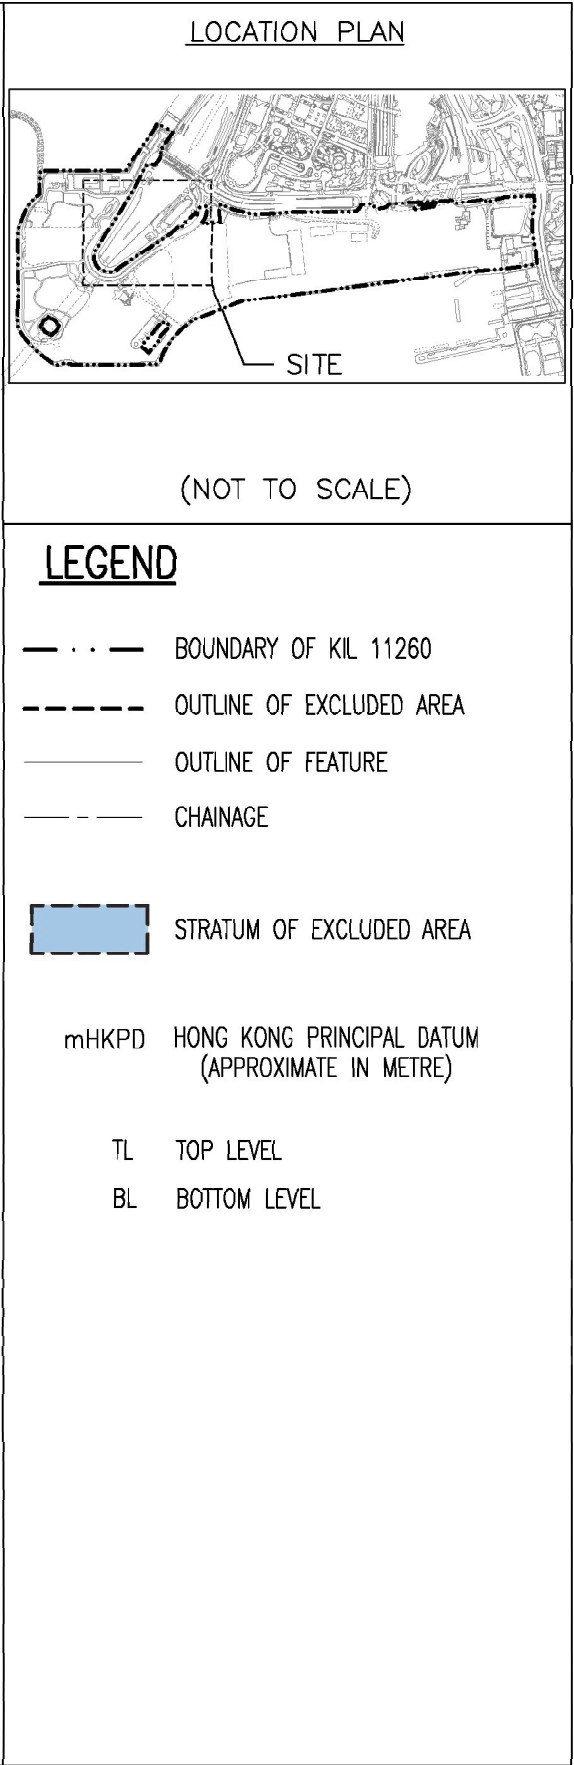


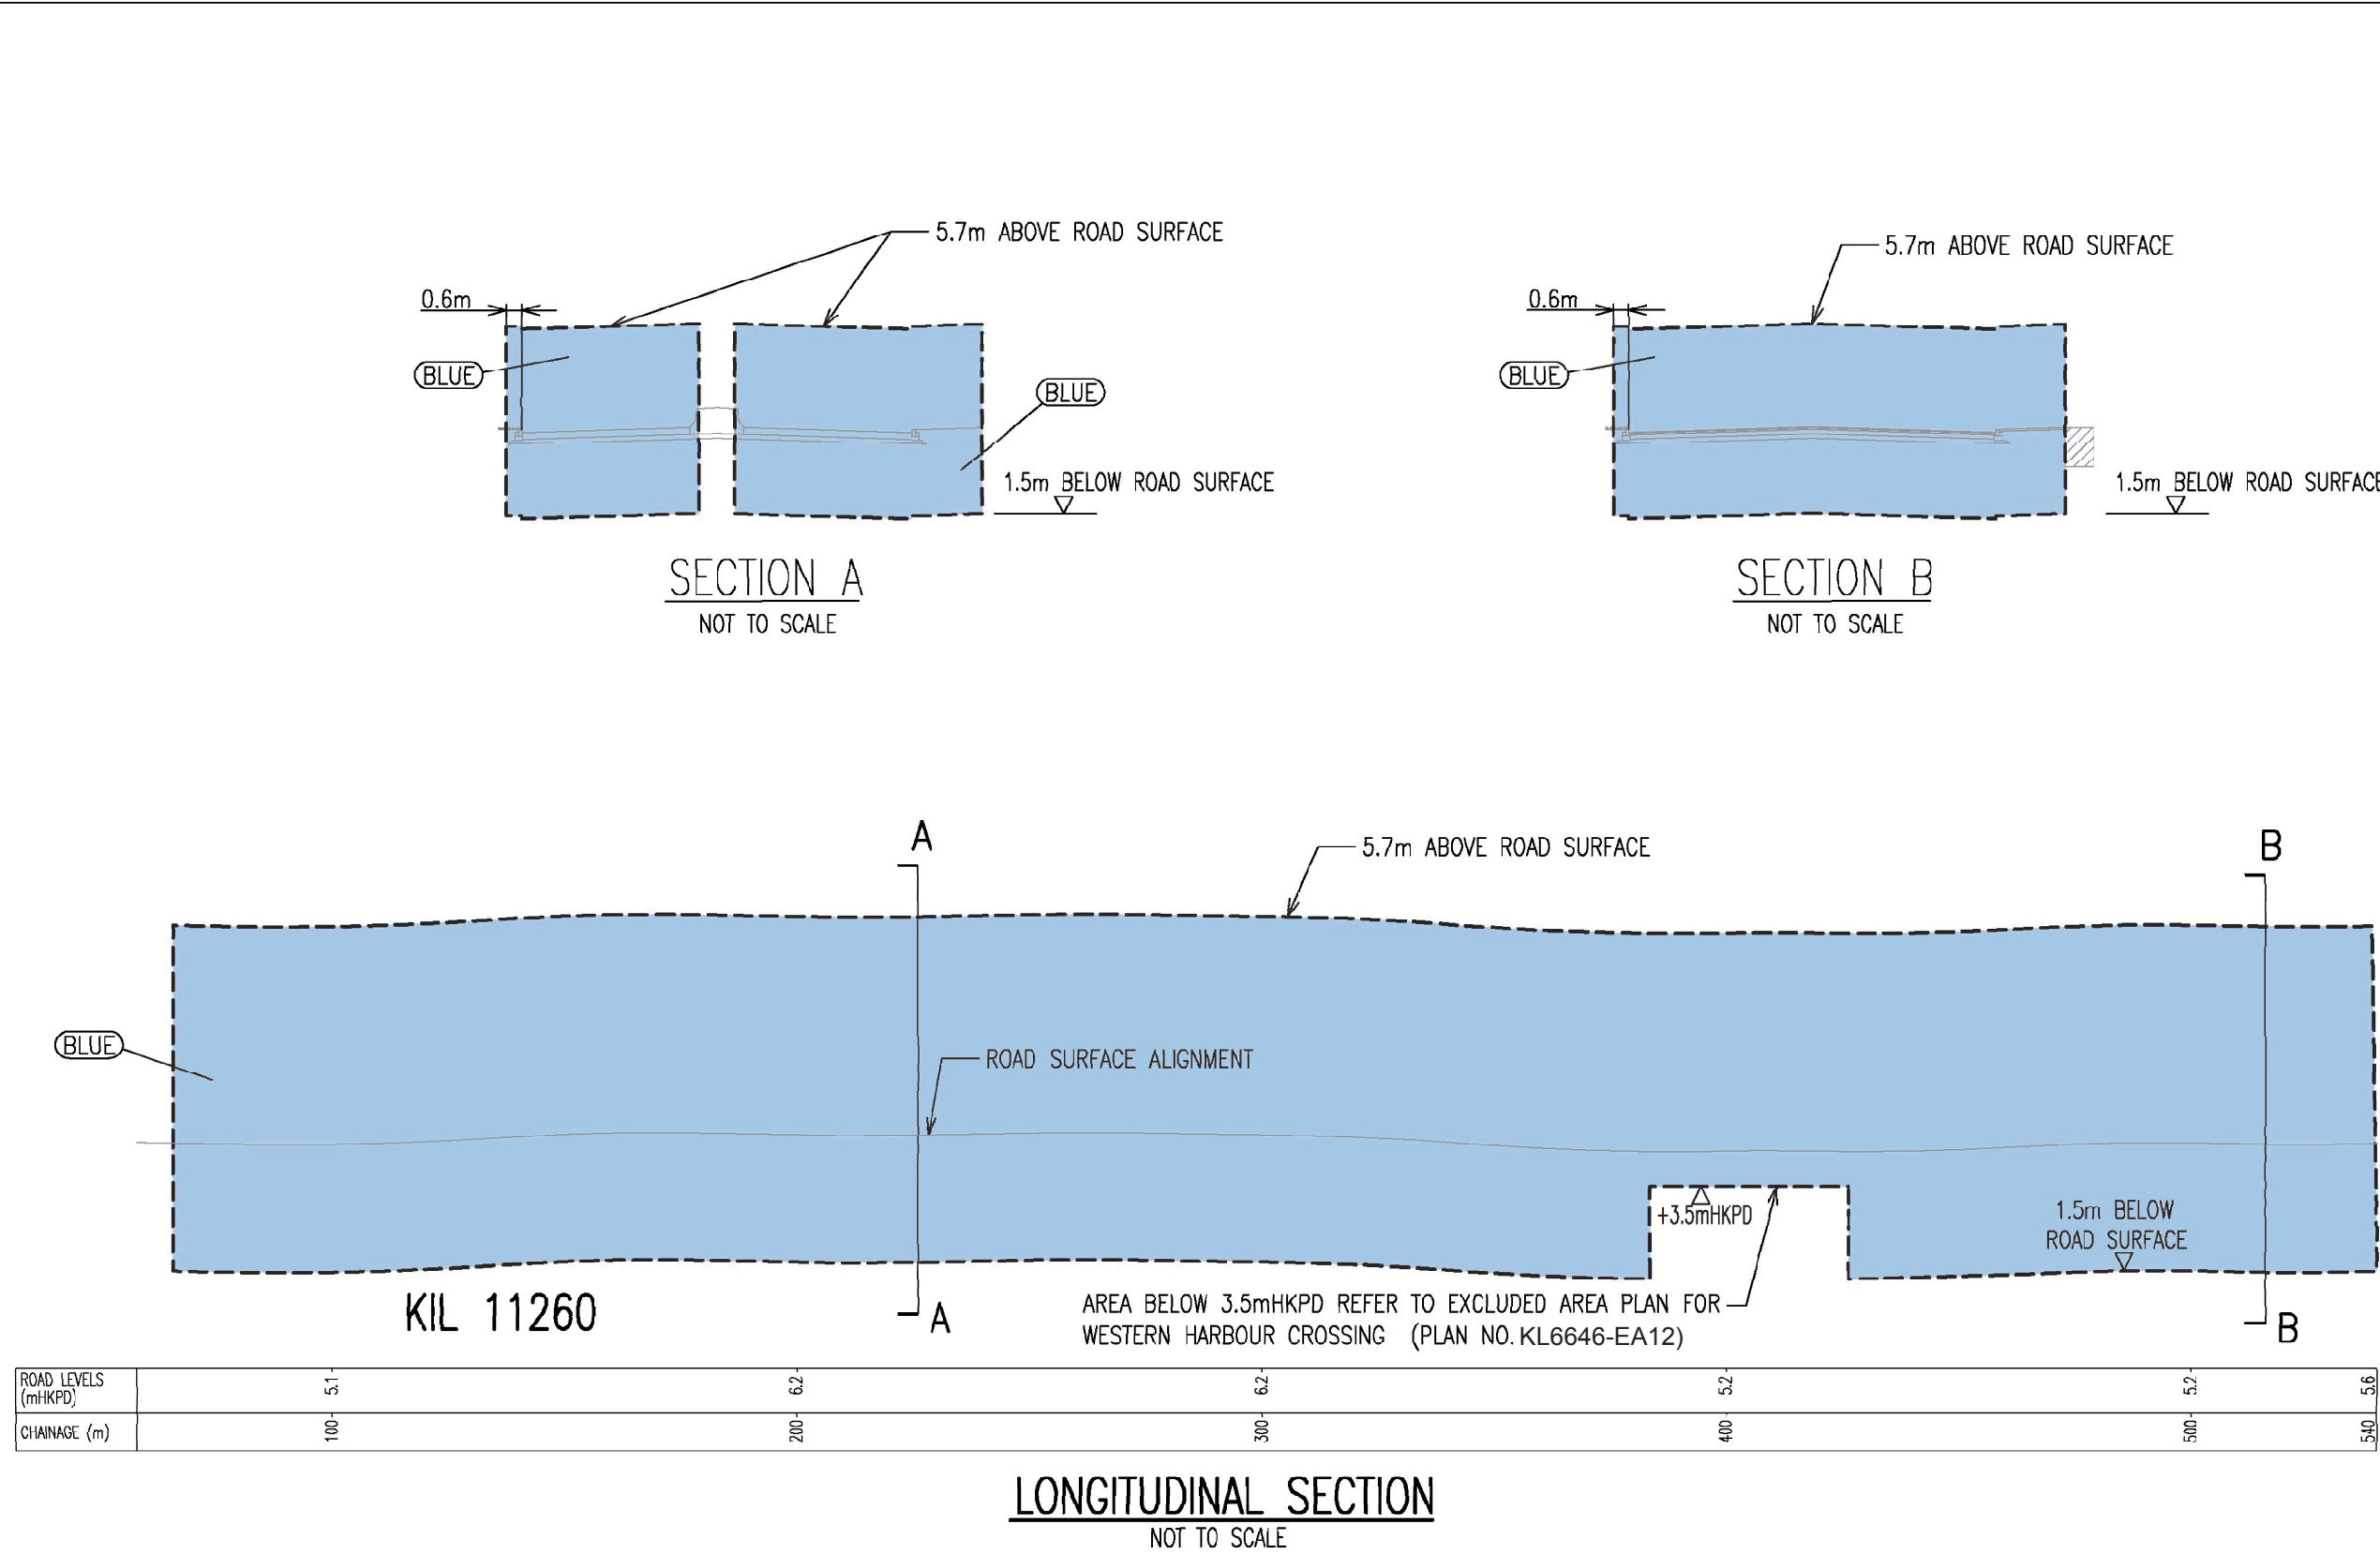

DISTRICT LANDS OFFICE
KOWLOON WEST
LANDS DEPARTMENT

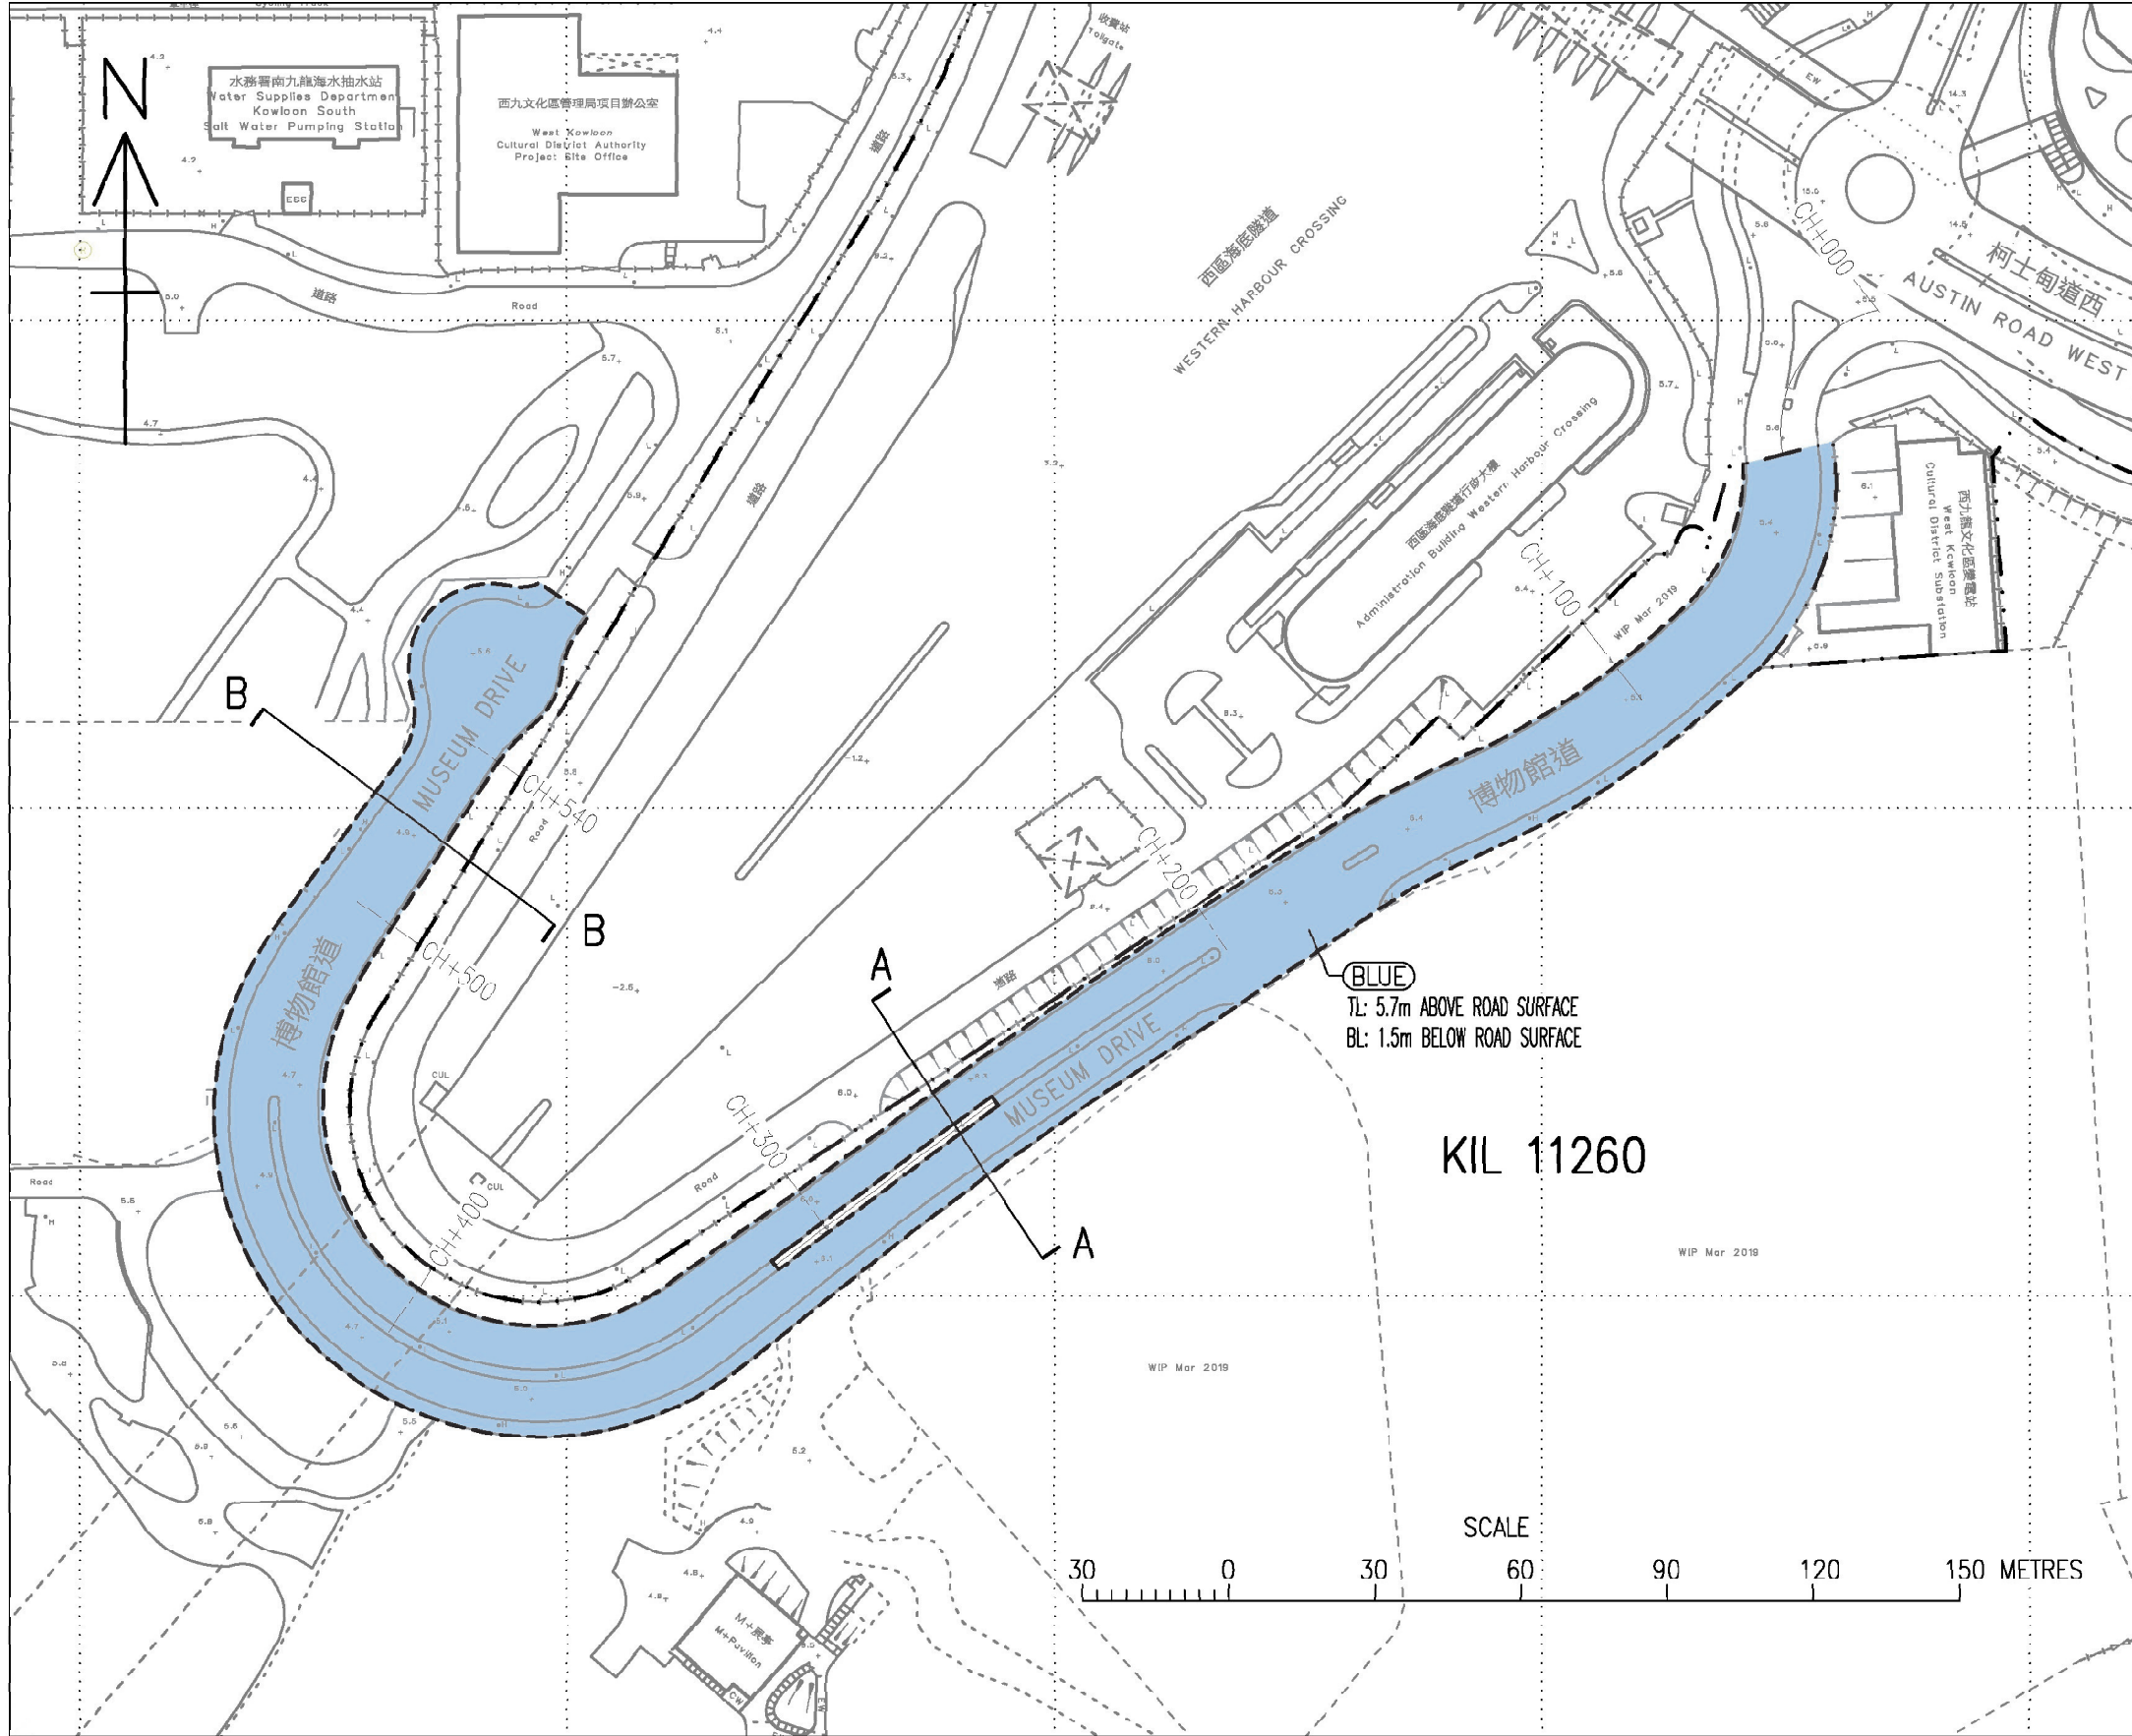

The Corporate Seal of the Grantee is affixed
by authority of the Board of the Grantee and
authenticated by the following members of the
Board of the Grantee authorised by the Board:

Member of the Board of the Grantee

Member of the Board of the Grantee

Witness to the signature of
District Lands Officer, Kowloon West

Civil Servant,
Lands Department

District Lands Officer,
Kowloon West

FOR IDENTIFICATION PURPOSES ONLY

District Lands Office, Kowloon West
Lands Department

Plan Prepared by District Survey Office, Kowloon
© Copyright reserved - Hong Kong SAR Government

KOWLOON INLAND LOT No. 11260
EXCLUDED AREA FOR MUSEUM DRIVE

File No. DSO/K 031/2015
Survey Sheet No. 11-NW-23D & 24C, 11-SW-3B & 4A
Layout Plan No. ---
Reference Plan No. 4192-EA05 (06 DEC 2019)
PLAN No. KL6646-EA05

Date :23/01/2020

Dated this ___ day of _____ 20__