

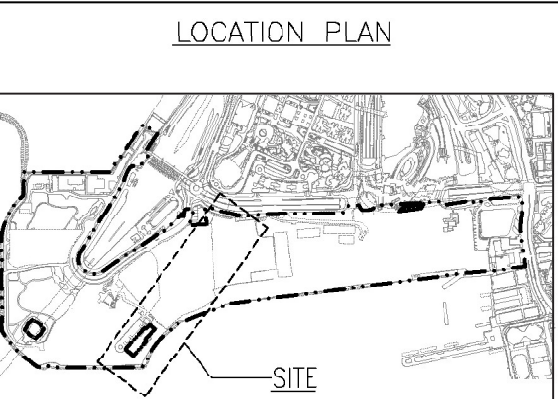


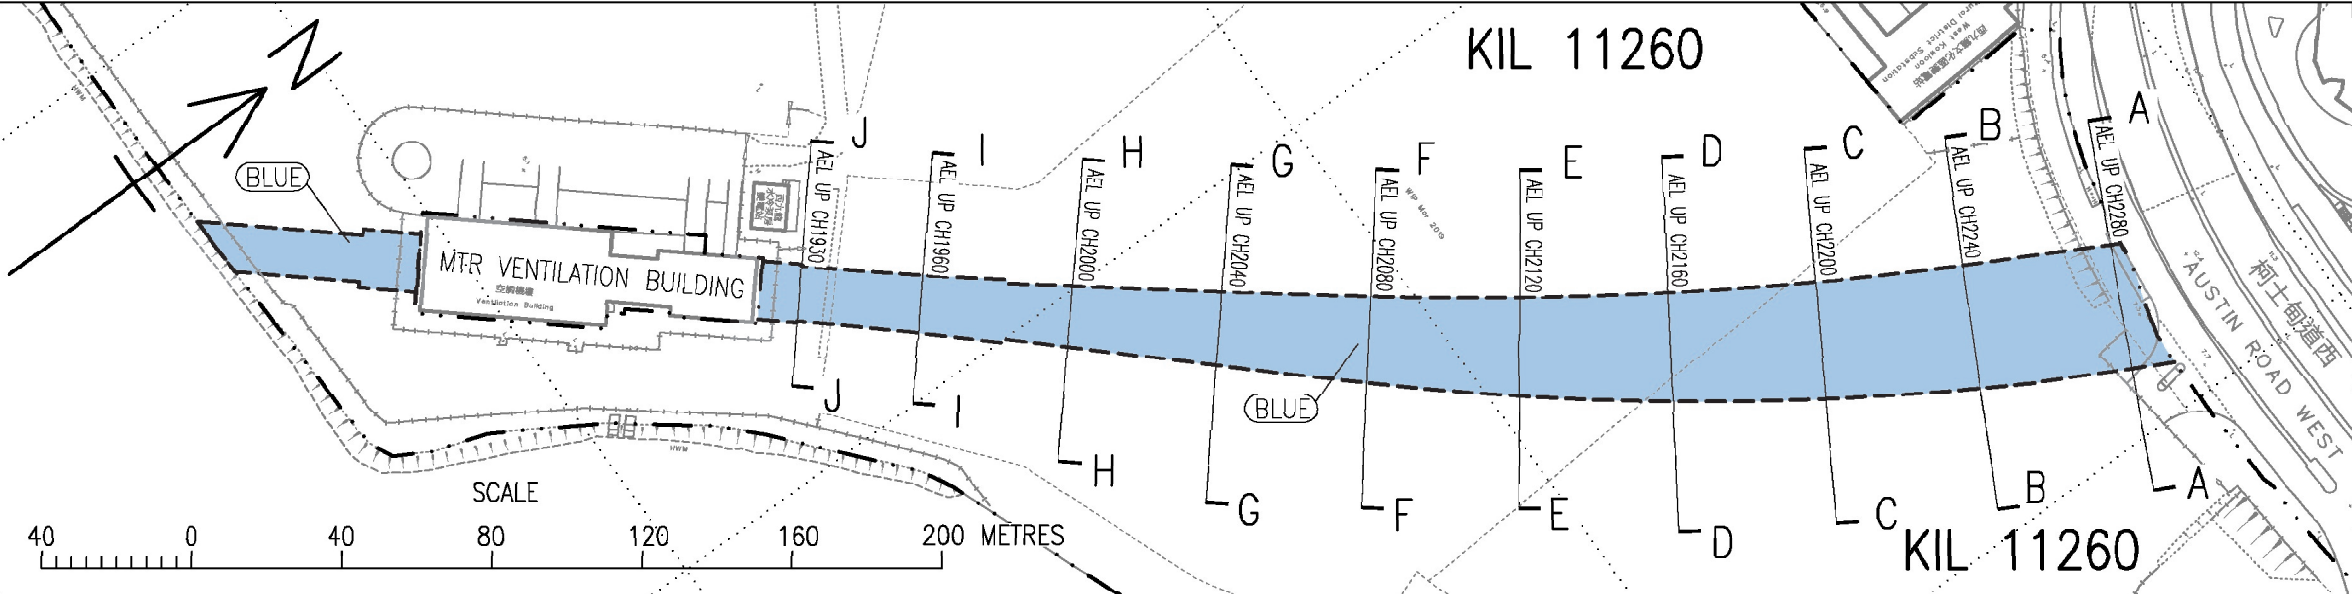

(NOT TO SCALE)

LEGEND

- BOUNDARY OF KIL 11260
- - - OUTLINE OF EXCLUDED AREA
- OUTLINE OF FEATURE
- [Blue Shaded Area] STRATA OF EXCLUDED AREAS
- mHKPD HONG KONG PRINCIPAL DATUM (APPROXIMATE IN METRE)

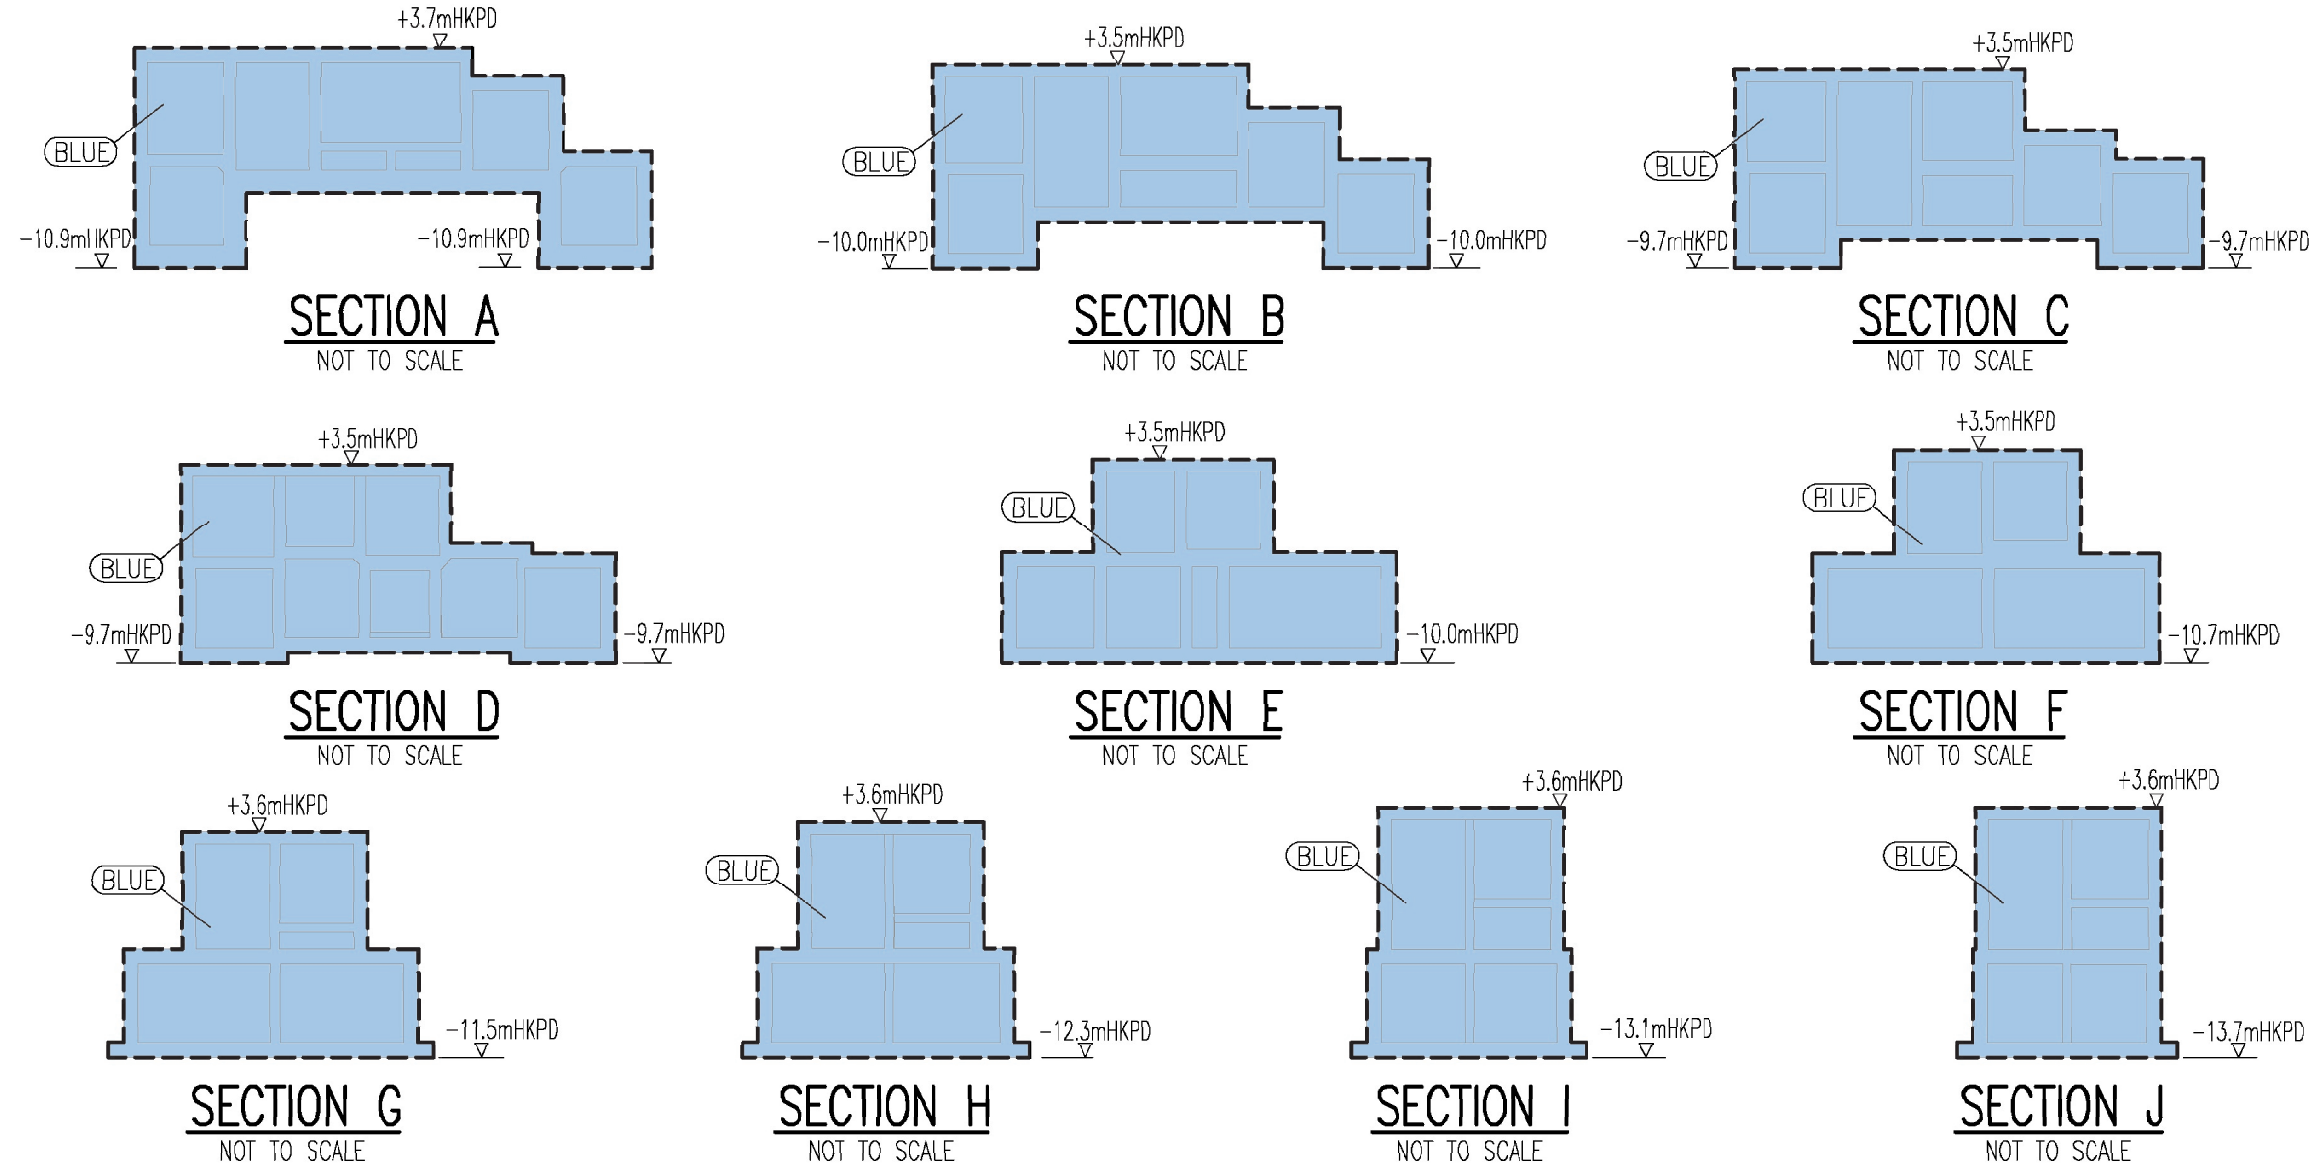

The Corporate Seal of the Grantee is affixed by authority of the Board of the Grantee and authenticated by the following members of the Board of the Grantee authorised by the Board:

Member of the Board of the Grantee

Member of the Board of the Grantee

Witness to the signature of
District Lands Officer, Kowloon West

Civil Servant,
Lands Department

District Lands Officer,
Kowloon West

FOR IDENTIFICATION PURPOSES ONLY

District Lands Office, Kowloon West
Lands Department

Plan Prepared by District Survey Office, Kowloon
© Copyright reserved - Hong Kong SAR Government

KOWLOON INLAND LOT No. 11260
EXCLUDED AREAS FOR MTR LOT No. 2 RP

File No. DSO/K 031/2015
Survey Sheet No. 11-NW-23D & 24C,11-SW-3B & 4A
Layout Plan No. ---
Reference Plan No. 4192-EA10 (06 DEC 2019)
PLAN No. KL6646-EA10

Date :23/01/2020

Dated this ___ day of _____ 20__