

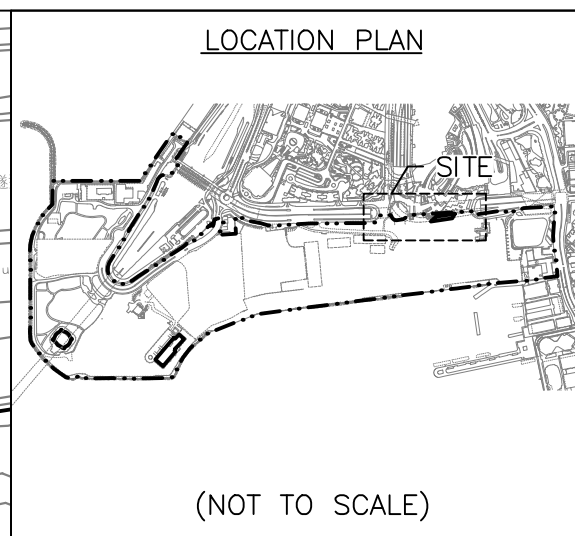


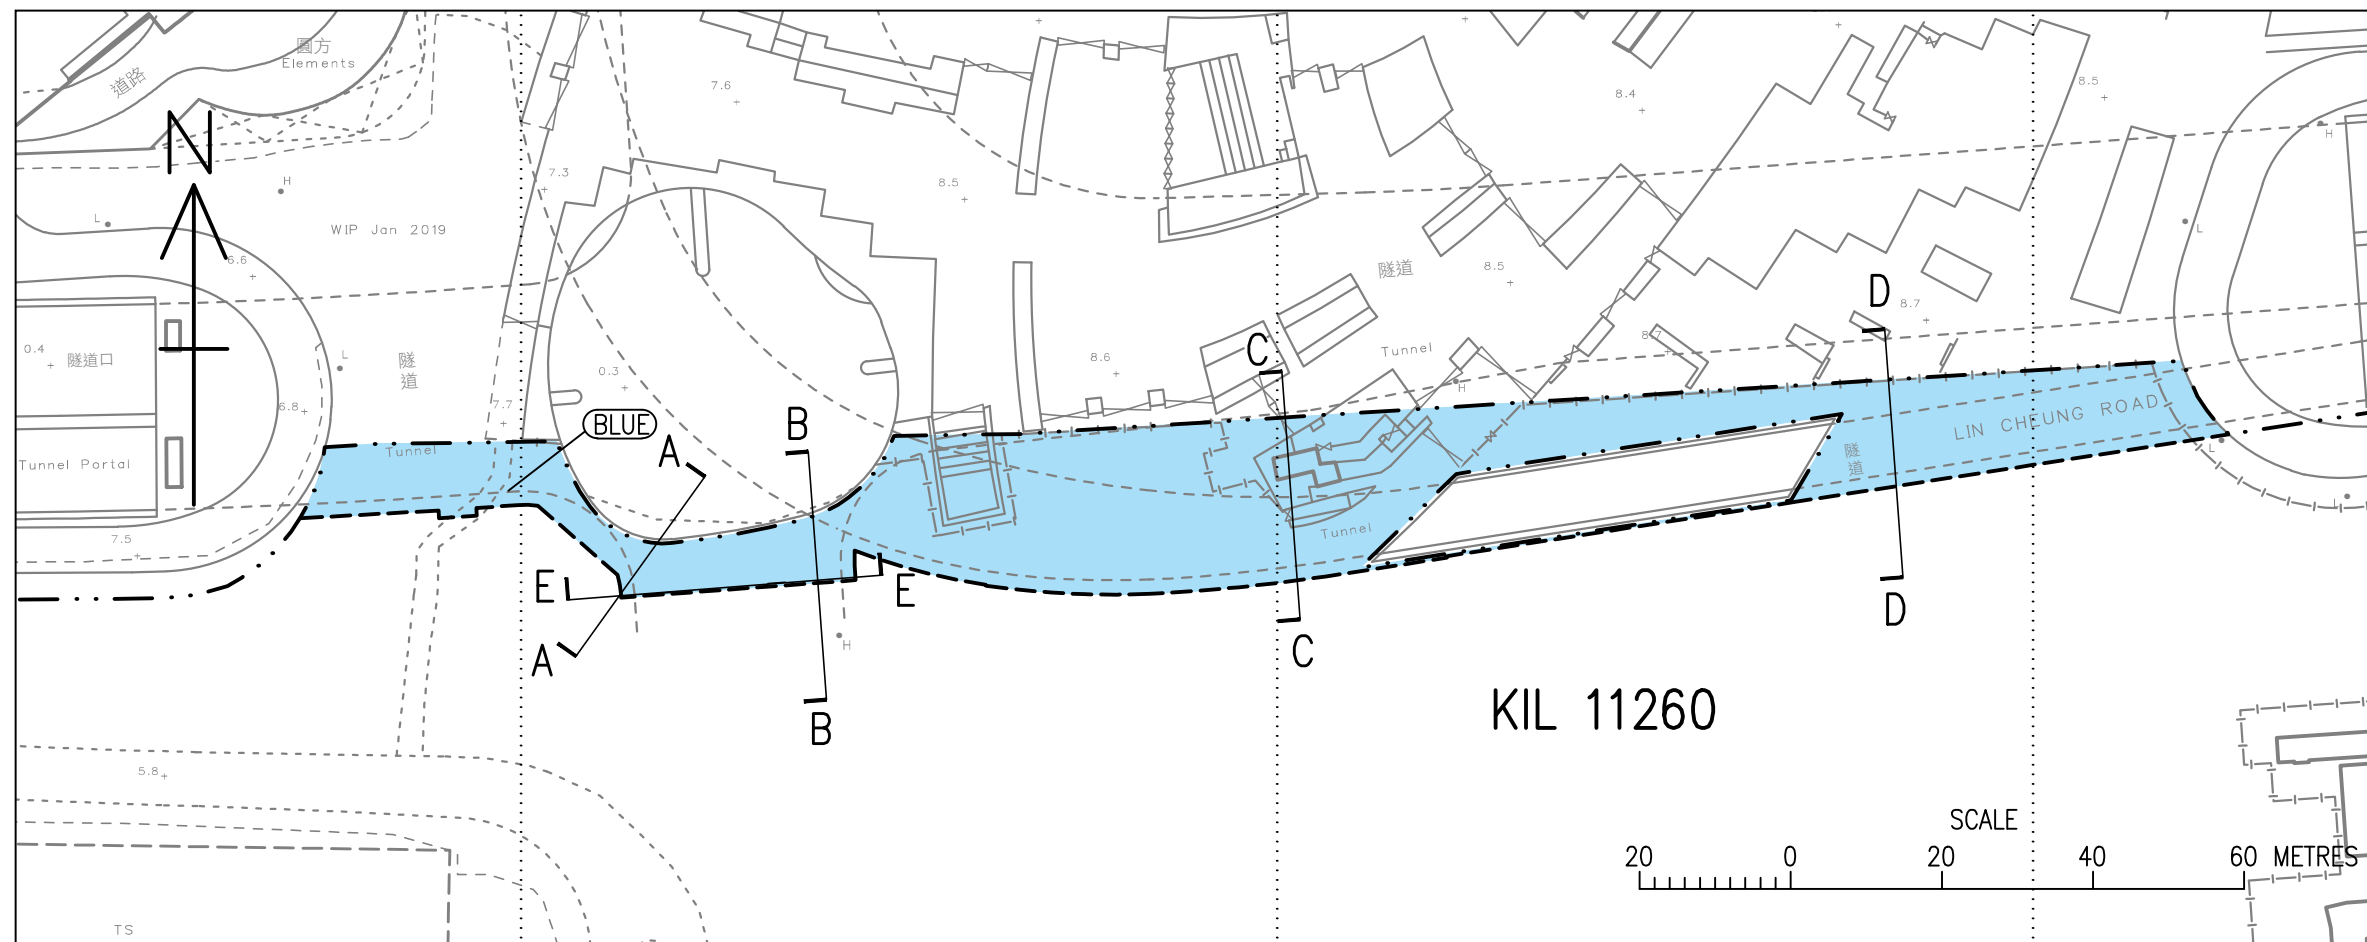


LEGEND

- BOUNDARY OF KIL 11260
- - - OUTLINE OF EXCLUDED AREA
- OUTLINE OF FEATURE
- STRATUM OF EXCLUDED AREA


mHKPD HONG KONG PRINCIPAL DATUM
(APPROXIMATE IN METRE)

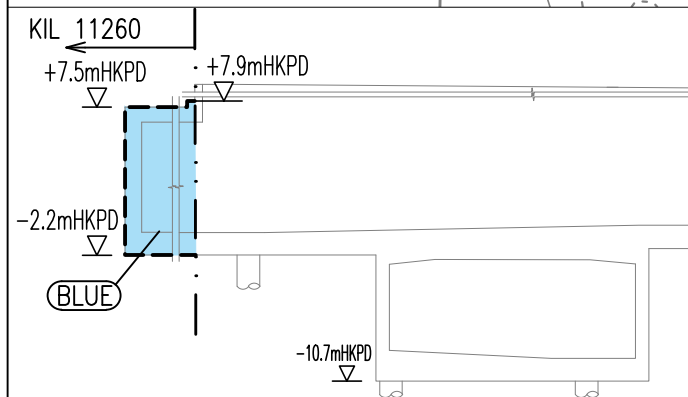


SECTION A
NOT TO SCALE

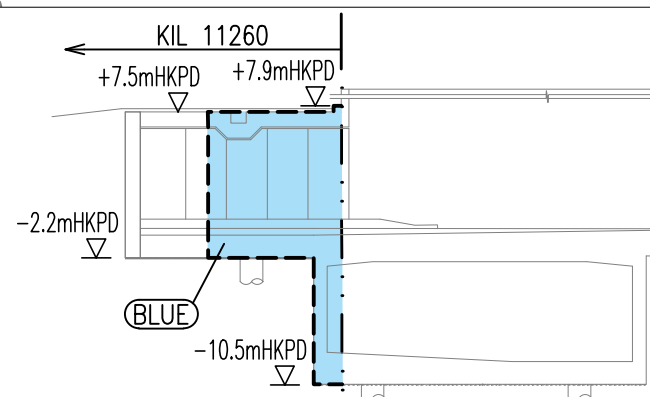


SECTION B
NOT TO SCALE

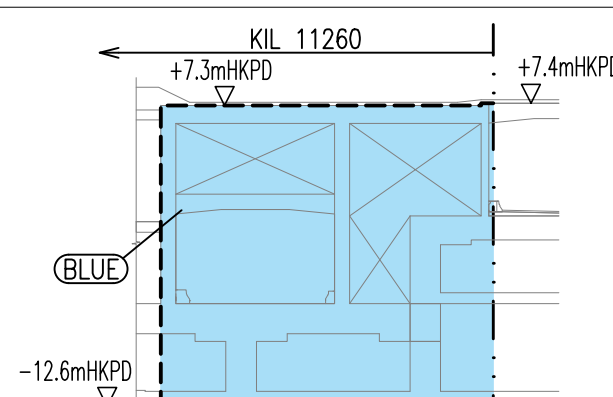

SECTION C
NOT TO SCALE

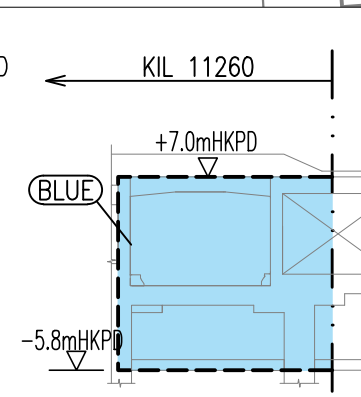

SECTION D
NOT TO SCALE

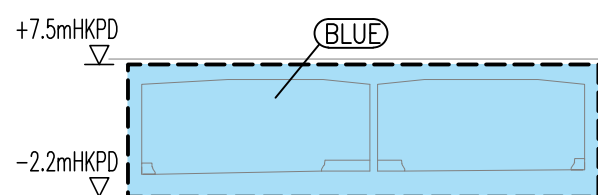

SECTION E
NOT TO SCALE

LAND MARKER (1980) H.K. Co., LTD.
標記測量(1980)香港有限公司

Survey District : KOWLOON

Survey Sheet : 11-NW-24C

Plan No.: 4192-EA03

KOWLOON INLAND LOT No. 11260 EXCLUDED AREA FOR UNDERPASS

SIGNED BY

JOSEPH Y C WONG
AUTHORIZED LAND SURVEYOR FHKIS MRICS RPS(LS)

Date: 27 NOVEMBER 2019