
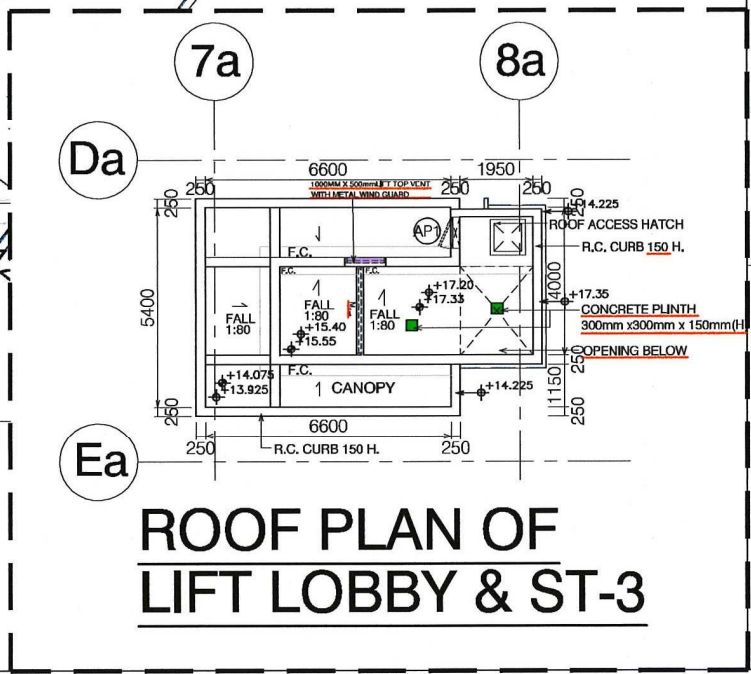
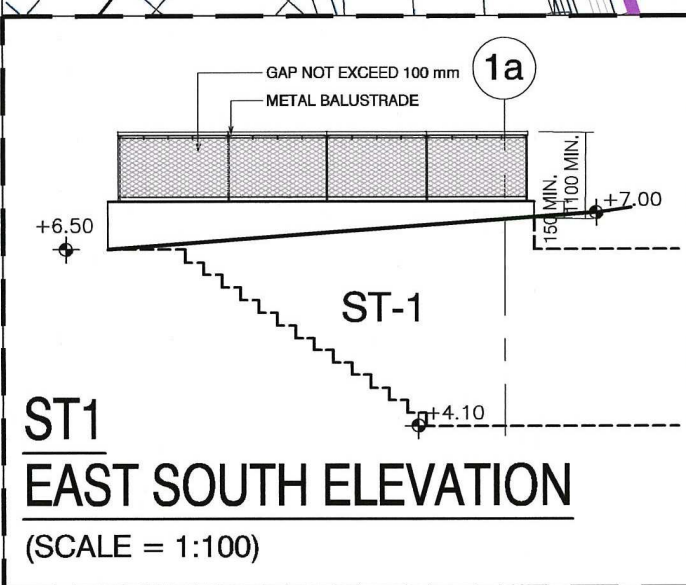
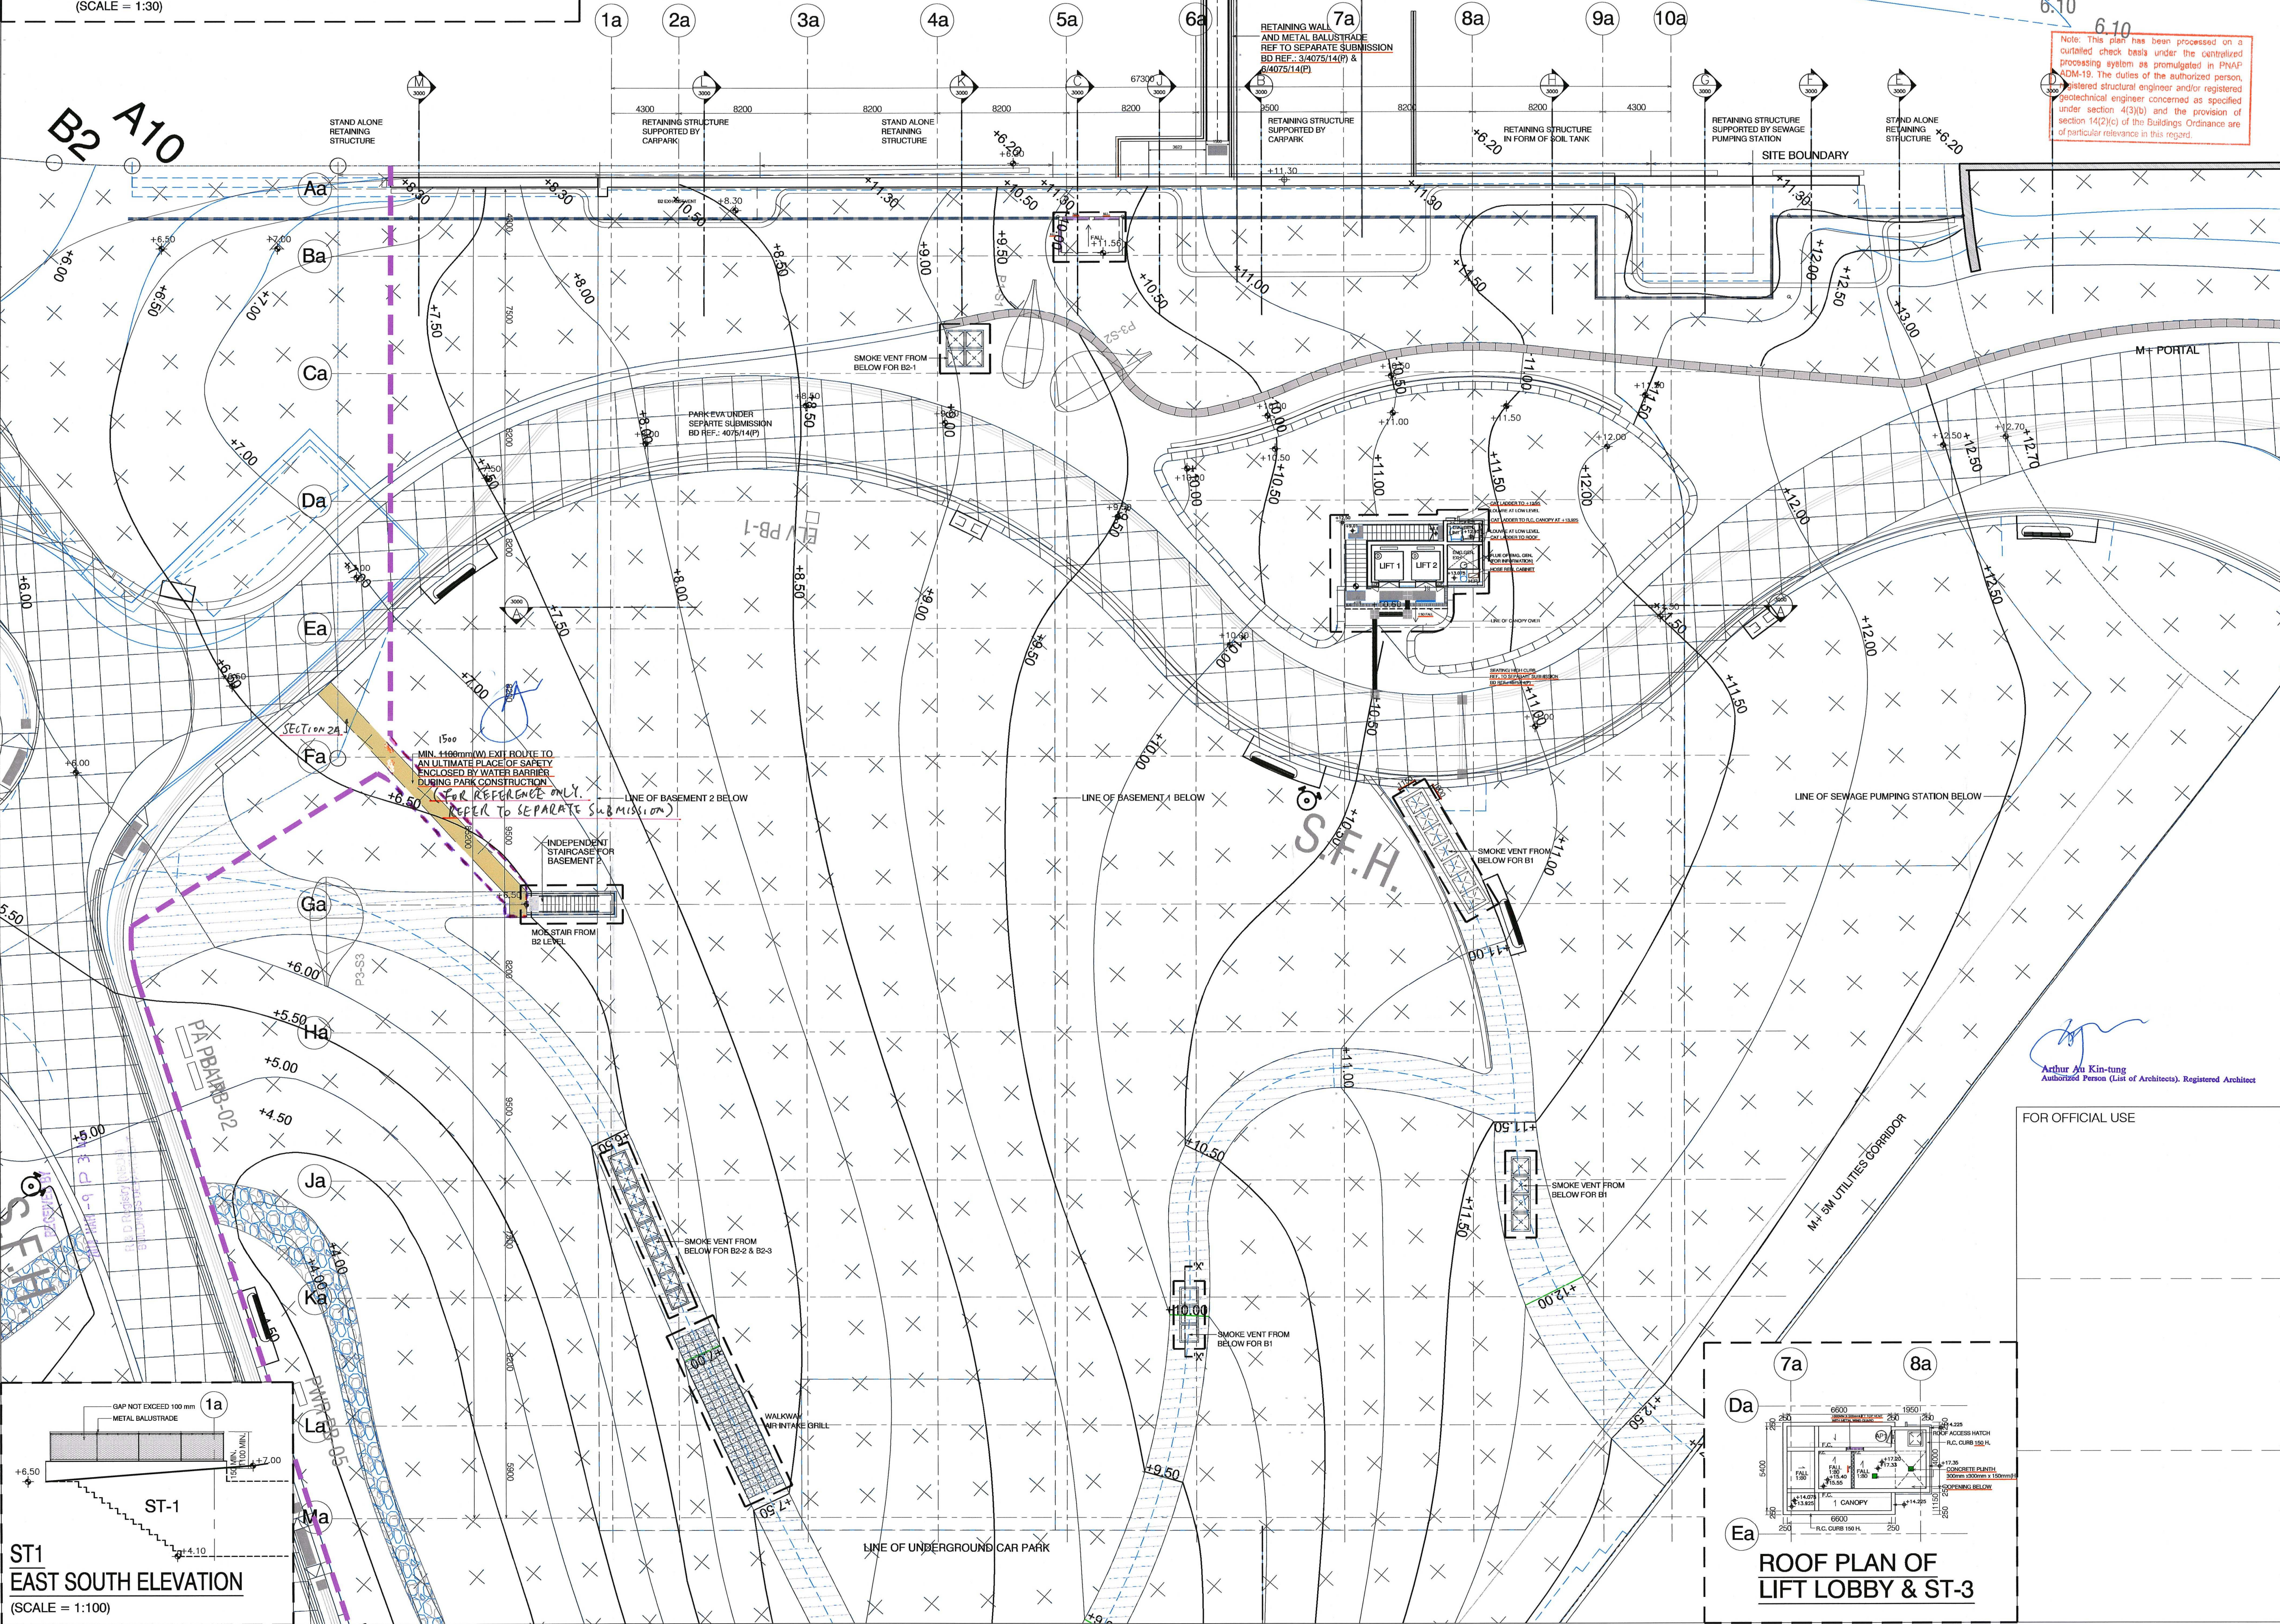
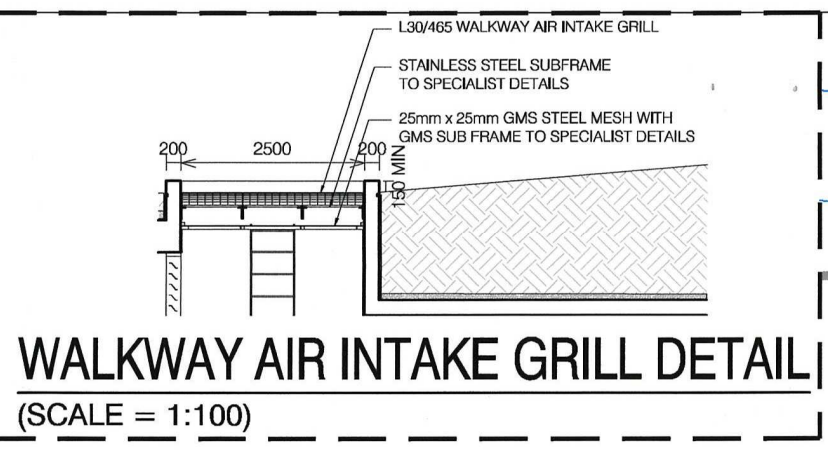


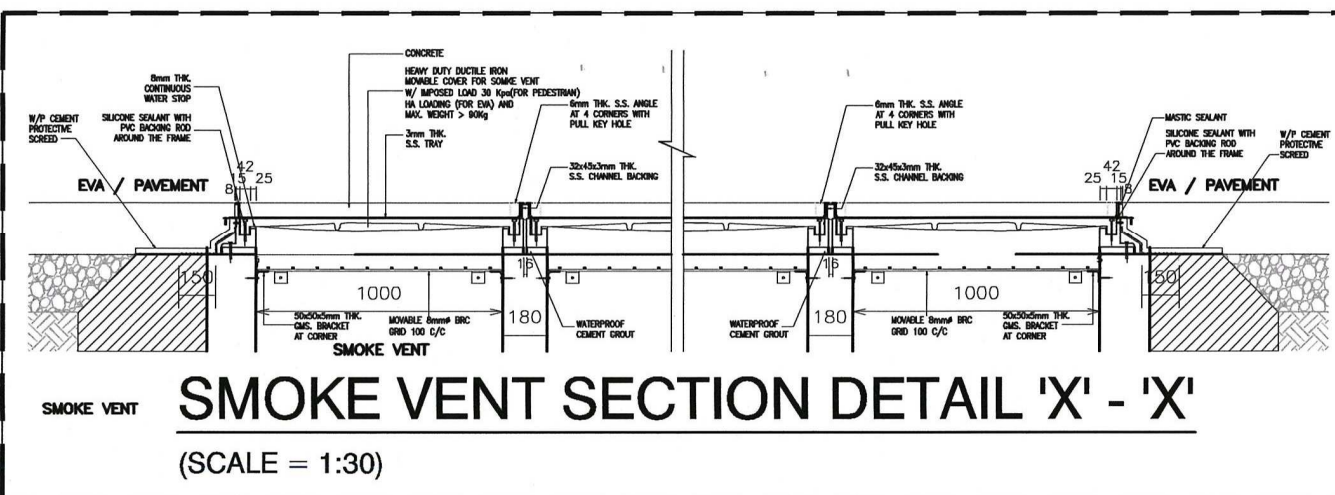

B.D. REF: BD 2/4043/14(P)
F.S.D. REF:
KEY PLAN

NOTES:

UNDER THIS SUBMISSION

Plan Approved

LI Ming-cham, Gordon
Senior Building Surveyor
for BUILDING AUTHORITY

29 MAR 2018

FOR BD APPROVAL

STATEMENT II: The works shown on these plans are Type II works in respect of which the Building Authority's consent is applied for.

REV.	DATE	DESCRIPTION	INITIAL
04	FEB 2018	GENERAL REVISION	K.T.
03	OCT 2017	GENERAL REVISION	H.K.
02	JUN 2017	GENERAL REVISION	H.K.
01	DEC 2015	GENERAL REVISION	H.K.

LEAD CONSULTANT & ARCHITECT

DLN

Dennis Lau & Ng Chun Man Architects & Engineers (HK) Ltd
46/F, Tower 1, Times Square, Matheson Street, Causeway Bay, Hong Kong

URBAN DESIGN & LANDSCAPE ARCHITECT

WEST 8

West 8 Urban Design & Landscape Architecture B.V.
Schiedamschen 13M, Postbus 8220, 3002 AE Rotterdam

CIVIL, GEO-TECHNICAL, STRUCTURAL, BUILDING SERVICES & ENVIRONMENTAL ENGINEER

ARCADIS

Hyder Consulting Limited
20/F, AKA Tower, Landmark East, 100 How Ming Street, Kowloon, Hong Kong

PROJECT LANDSCAPE ARCHITECT

ACLA

ACLA Limited
47/F, Hopewell Centre, 183 Queen's Road East, Wan Chai, Hong Kong

PROJECT QUANTITY SURVEYOR

利比 RLB

Rider Levett Bucknall
20th Floor, Eastern Central Plaza, 3 Yau Hong Road, Shaokwan, Hong Kong

JOB TITLE

THE PARK DEVELOPMENT FOR THE WEST KOWLOON CULTURAL DISTRICT

DRAWING TITLE

GROUND FLOOR PLAN

SCALE	1 : 200	PRINTED	31 DEC 2014
CHECKED	BRUCE LAW	DATE	31 DEC 2014
APPROVED	ARTHUR AU	DATE	31 DEC 2014
DRAWN	STELLA IP	DATE	31 DEC 2014

CONTRACT NO. CC/2015/3B/025

DRAWING NO. 3B52X-ARC-DWG-P00-L001-0003-GBP

CAD REF NAME: 00

DEVELOPER

westKowloon
西九文化區