


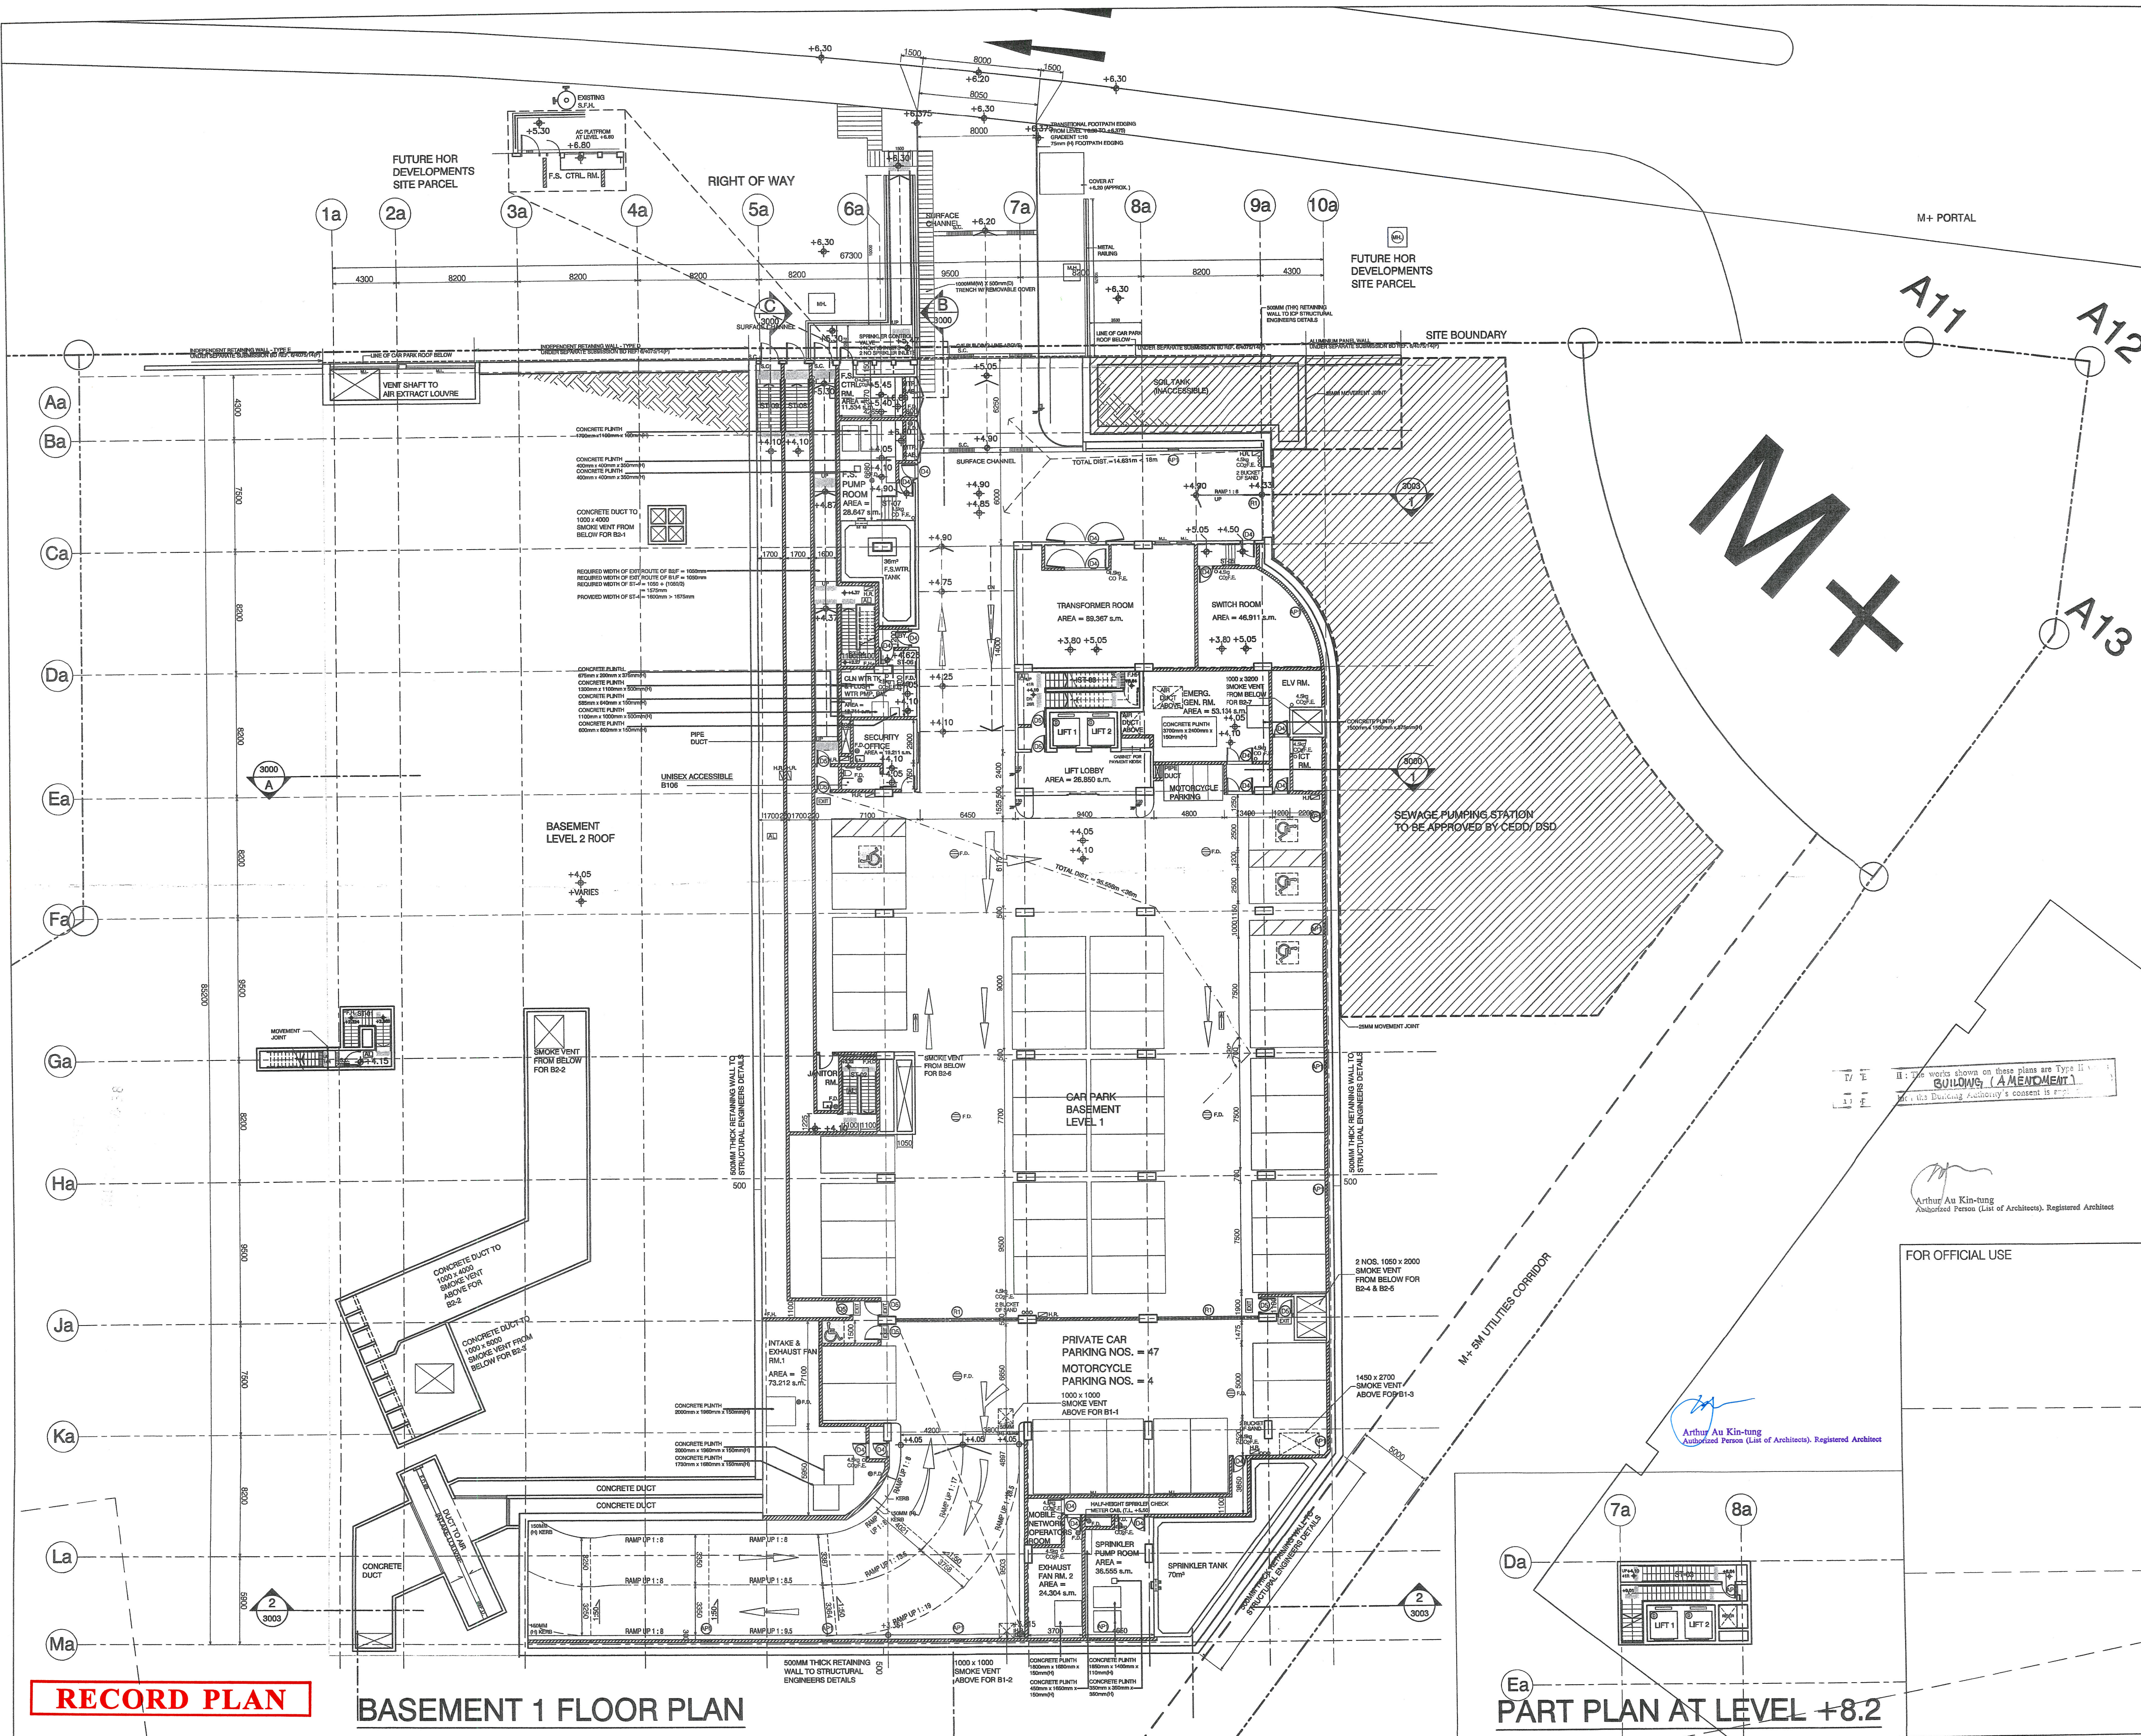

B.D. REF: BD 2/4043/14(P)
F.S.D. REF:
KEY PLAN

NOTES:

This plan has been processed on a limited check basis under the centralized processing system as stipulated in RAR. Having the duties of the authorized person, registered structural engineer and registered geotechnical engineer (concrete) as required under section 13(1)(b) and the provision of section 14(1)(b) of the Building Ordinance and in compliance with the RAR.

Plan Approved
LI Ming-chang Gordon
Senior Building Surveyor
for BUILDING AUTHORITY
- 8 JAN 2019

REV.	DATE	DESCRIPTION	INITIAL
07	DEC 2018	GENERAL REVISION	B.L.
06	DEC 2018	GENERAL REVISION	A.C.
05	OCT 2018	GENERAL REVISION	K.T.
04	FEB 2018	GENERAL REVISION	K.T.
03	OCT 2017	GENERAL REVISION	K.T.
02	JUN 2017	GENERAL REVISION	H.K.
01	DEC 2016	GENERAL REVISION	H.K.

LEAD CONSULTANT & ARCHITECT

Dennis Lau & Ng Chun Man
Architects & Engineers (HK) Ltd.
46/F, Tower 1, Times Square,
Matheson Street
Causeway Bay
Hong Kong

URBAN DESIGN & LANDSCAPE ARCHITECT

West 8 Urban Design & Landscape Architecture B.V.
Schiedamschen 134A
Postbus 6250
3002 AE Rotterdam

CIVIL, GEO-TECHNICAL, STRUCTURAL,
BUILDING SERVICES &
ENVIRONMENTAL ENGINEER

Hyder Consulting Limited
22/F, AIA Tower, Landmark East
100 How Ming Street
Kwai Tong, Kowloon
Hong Kong

PROJECT LANDSCAPE ARCHITECT

ACLA Limited
47/F, Hopwood Centre,
183 Queen's Road East,
Wan Chai
Hong Kong

PROJECT QUANTITY SURVEYOR

Rider Levett Bucknall
25th Floor,
Eastern Central Plaza,
3 Yiu Hing Road,
Shaohkwan, Hong Kong

JOB TITLE
**THE PARK DEVELOPMENT FOR
THE WEST KOWLOON CULTURAL DISTRICT**

DRAWING TITLE
BASEMENT 1 PLAN

SCALE	1 : 200	PRINTED	31 DEC 2014
CHECKED	BRUCE LAW	DATE	31 DEC 2014
APPROVED	ARTHUR AU	DATE	31 DEC 2014
DRAWN	STELLA IP	DATE	31 DEC 2014

CONTRACT NO. CC/2015/3B/025

DRAWING NO. 3B52X-ARC-DWG-P00-LB01-0002-GBP

CAD REF NAME: 3B52X-ARC-DWG-P00-LB01-0002-GBP

DEVELOPER

西九文化區