



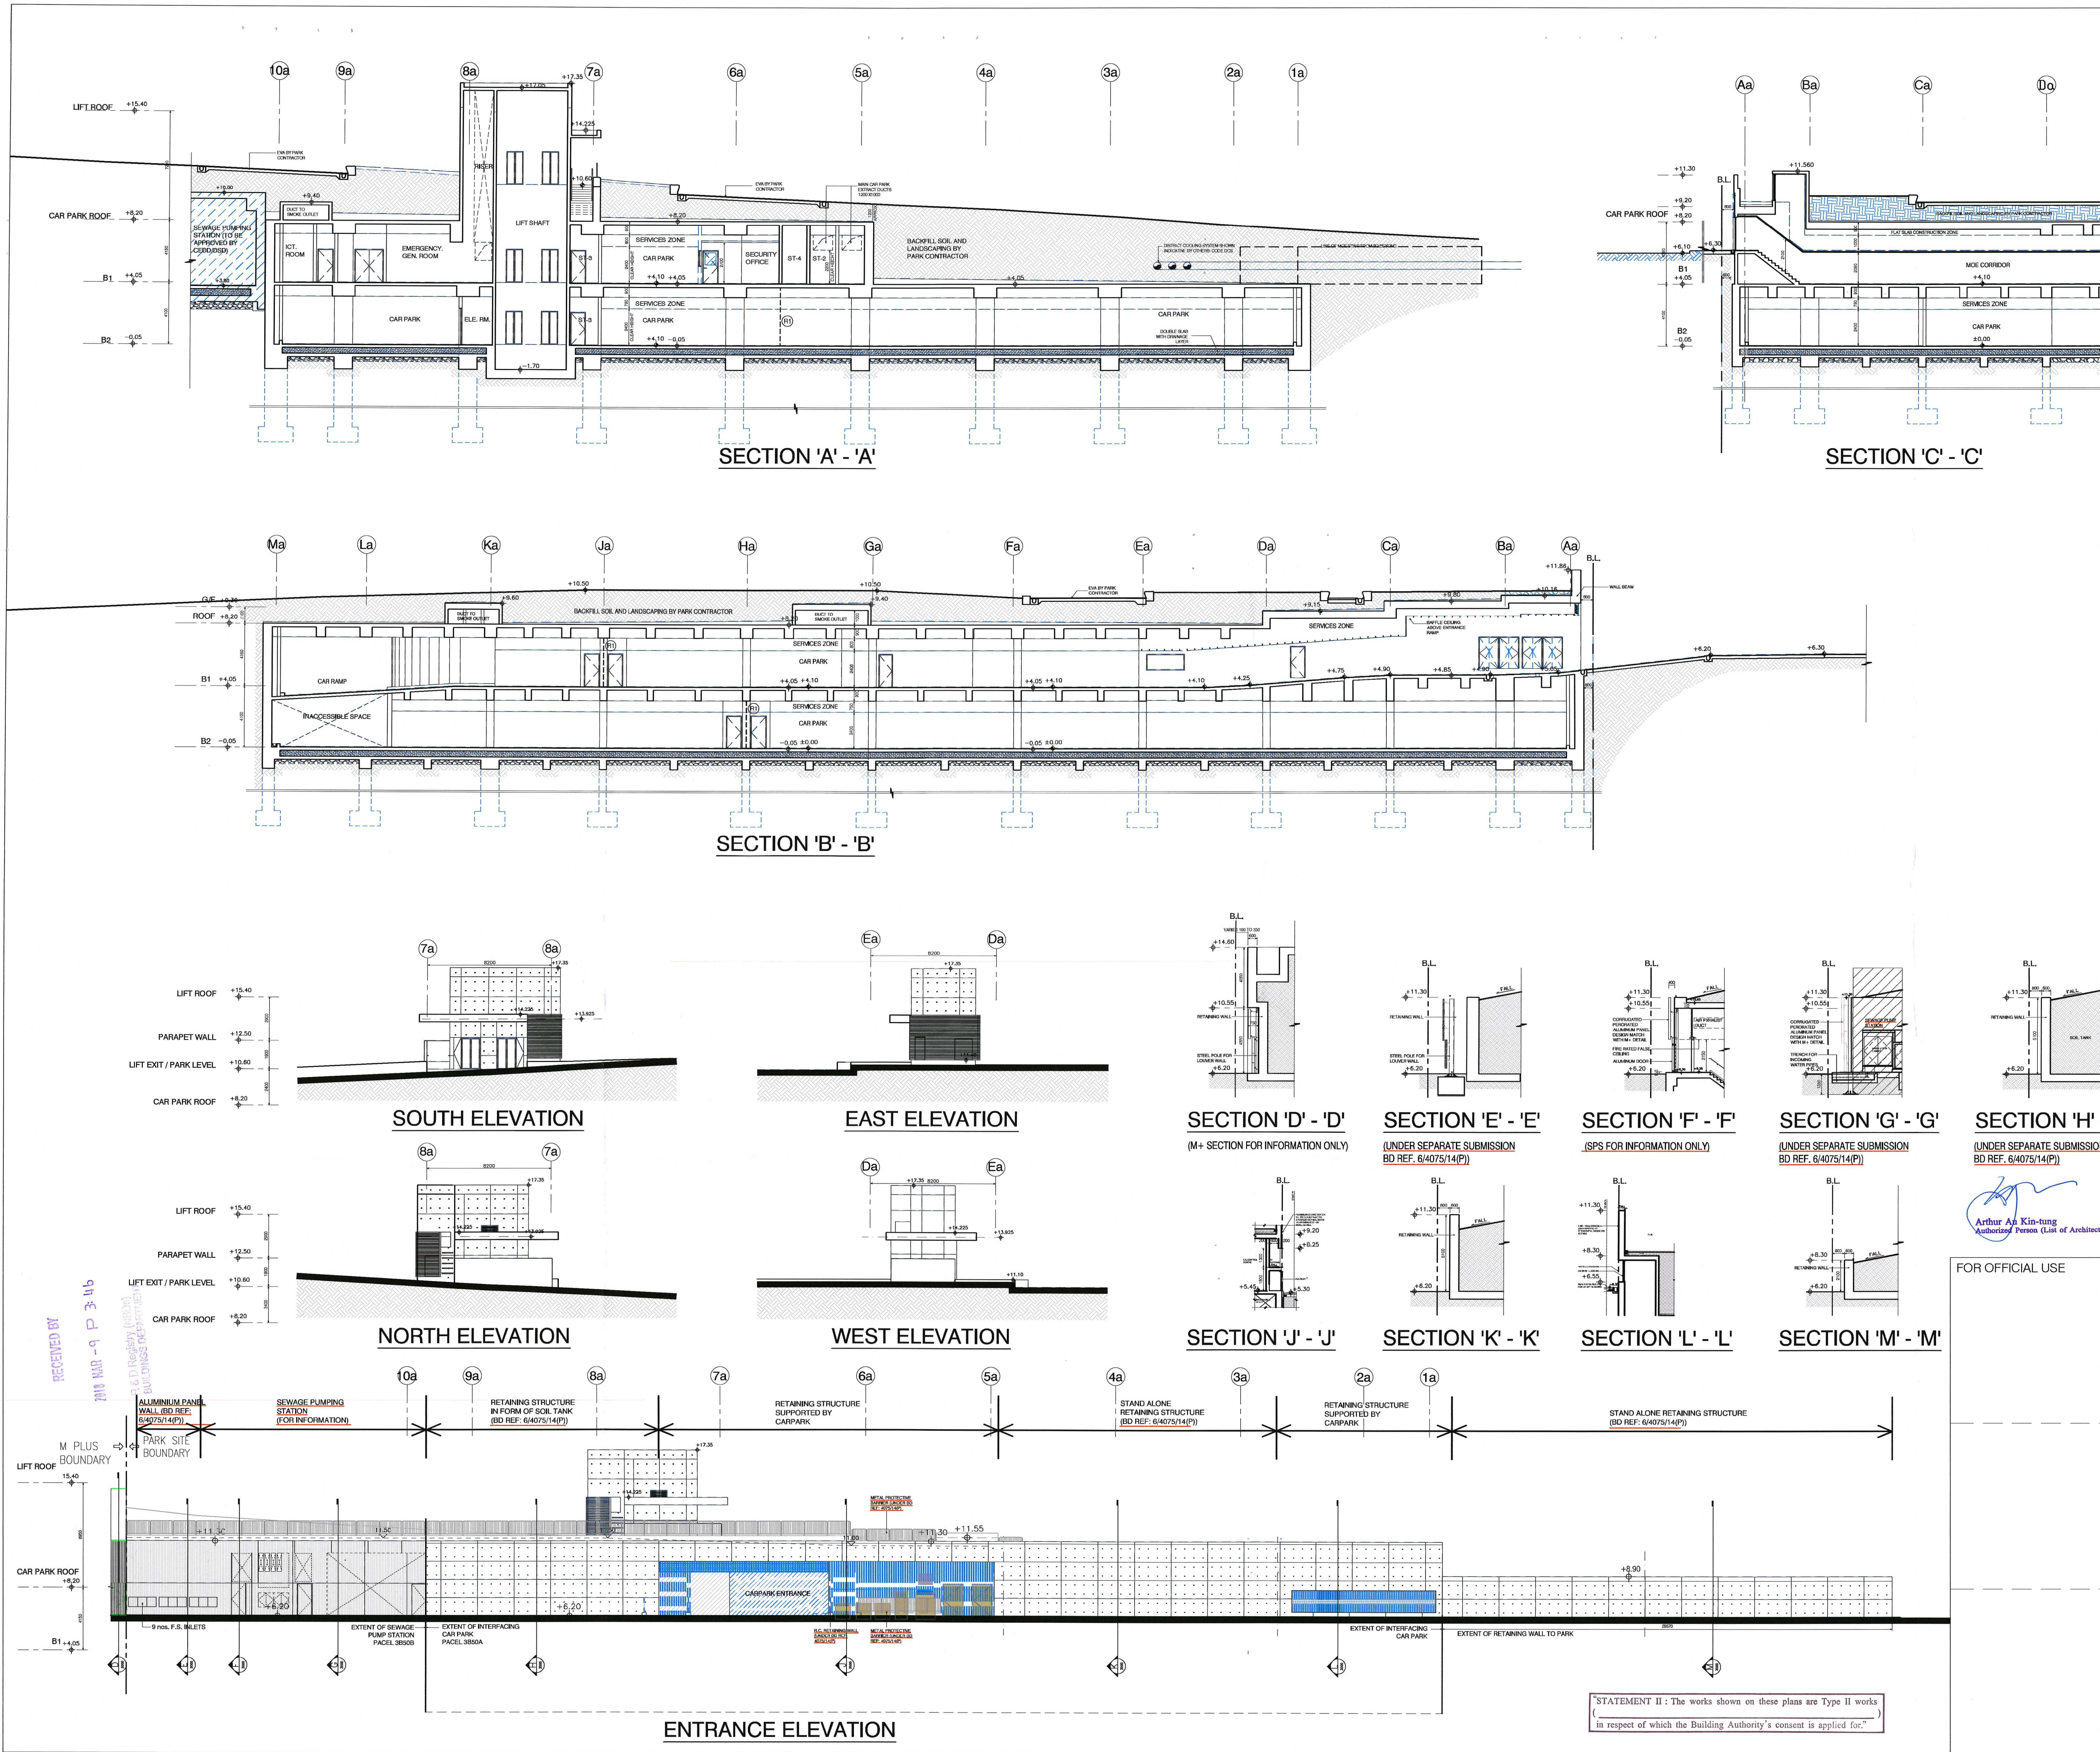

B.D. REF: BD 2/4043/14(P)
F.S.D. REF:
KEY PLAN

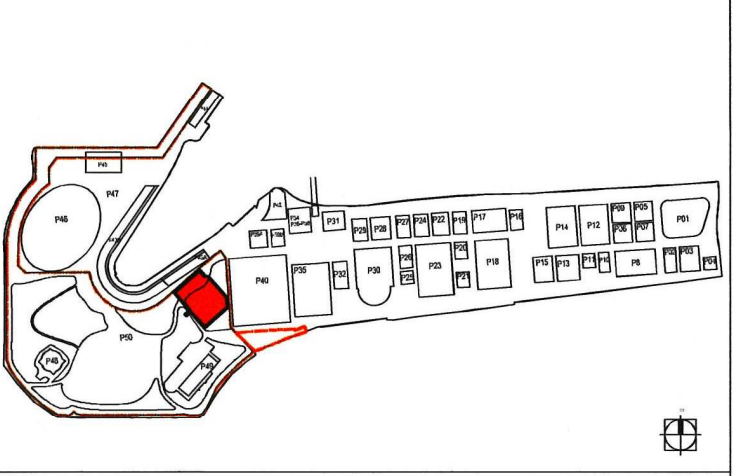

KEY PLAN
NOTES:
Note: This plan has been processed on a curtailed check basis under the centralized processing system as promulgated in PNAP A04-19. The duties of the authorized person, registered structural engineer and/or registered geotechnical engineer concerned as specified under section 4(3)(b) and the provision of section 14(2)(c) of the Buildings Ordinance are of particular relevance in this regard.

Plan Approved
LI Ming-cham, Gordon
Senior Building Surveyor
for BUILDING AUTHORITY
29 MAR 2018

FOR BD APPROVAL

REV.	DATE	DESCRIPTION	INITIAL
03	FEB 2018	GENERAL REVISION	K.T.
02	JUN 2017	GENERAL REVISION	H.K.
01	DEC 2015	GENERAL REVISION	H.K.

LEAD CONSULTANT & ARCHITECT
DLN
Dennis Lau & Ng Chun Man
Architects & Engineers (HK) Ltd.
46/F, Tower 1, Times Square,
Matheson Street
Causeway Bay
Hong Kong

URBAN DESIGN & LANDSCAPE ARCHITECT
WEST 8
West 8 Urban Design & Landscape Architecture B.V.
Schiedamschen 13M
Postbus 6020
3002 AE Rotterdam

CIVIL, GEO-TECHNICAL, STRUCTURAL,
BUILDING SERVICES &
ENVIRONMENTAL ENGINEER
ARCADIS
Hyder Consulting Limited
20/F, AXA Tower Landmark East
100 How Ming Street
Kowloon Tong, Kowloon
Hong Kong

PROJECT LANDSCAPE ARCHITECT
ACLA
ACLA Limited
47/F, Hopewell Centre,
183 Queen's Road East,
Wan Chai
Hong Kong

PROJECT QUANTITY SURVEYOR
利比 RLB/Rider Levett Bucknall
Rider Levett Bucknall
28th Floor,
Eastern Central Plaza,
3 Yiu Hing Road,
Shaohwan, Hong Kong

JOB TITLE

THE PARK DEVELOPMENT FOR
THE WEST KOWLOON CULTURAL DISTRICT
DRAWING TITLE
CAR PARK SECTION 'A', 'B', 'C' &
WEST NORTH ELEVATION

SCALE 1 : 200 PRINTED 31 DEC 2014

CHECKED BRUCE LAW DATE 31 DEC 2014

APPROVED ARTHUR AU DATE 31 DEC 2014

DRAWN STELLA IP DATE 31 DEC 2014

CONTRACT NO. CC/2015/3B/025

DRAWING NO. 3B52X-ARC-DWG-P00-XXXX-3000-GBP

CAD REF NAME: 00

DEVELOPER

REV. 03

westKowloon
西九文化區