



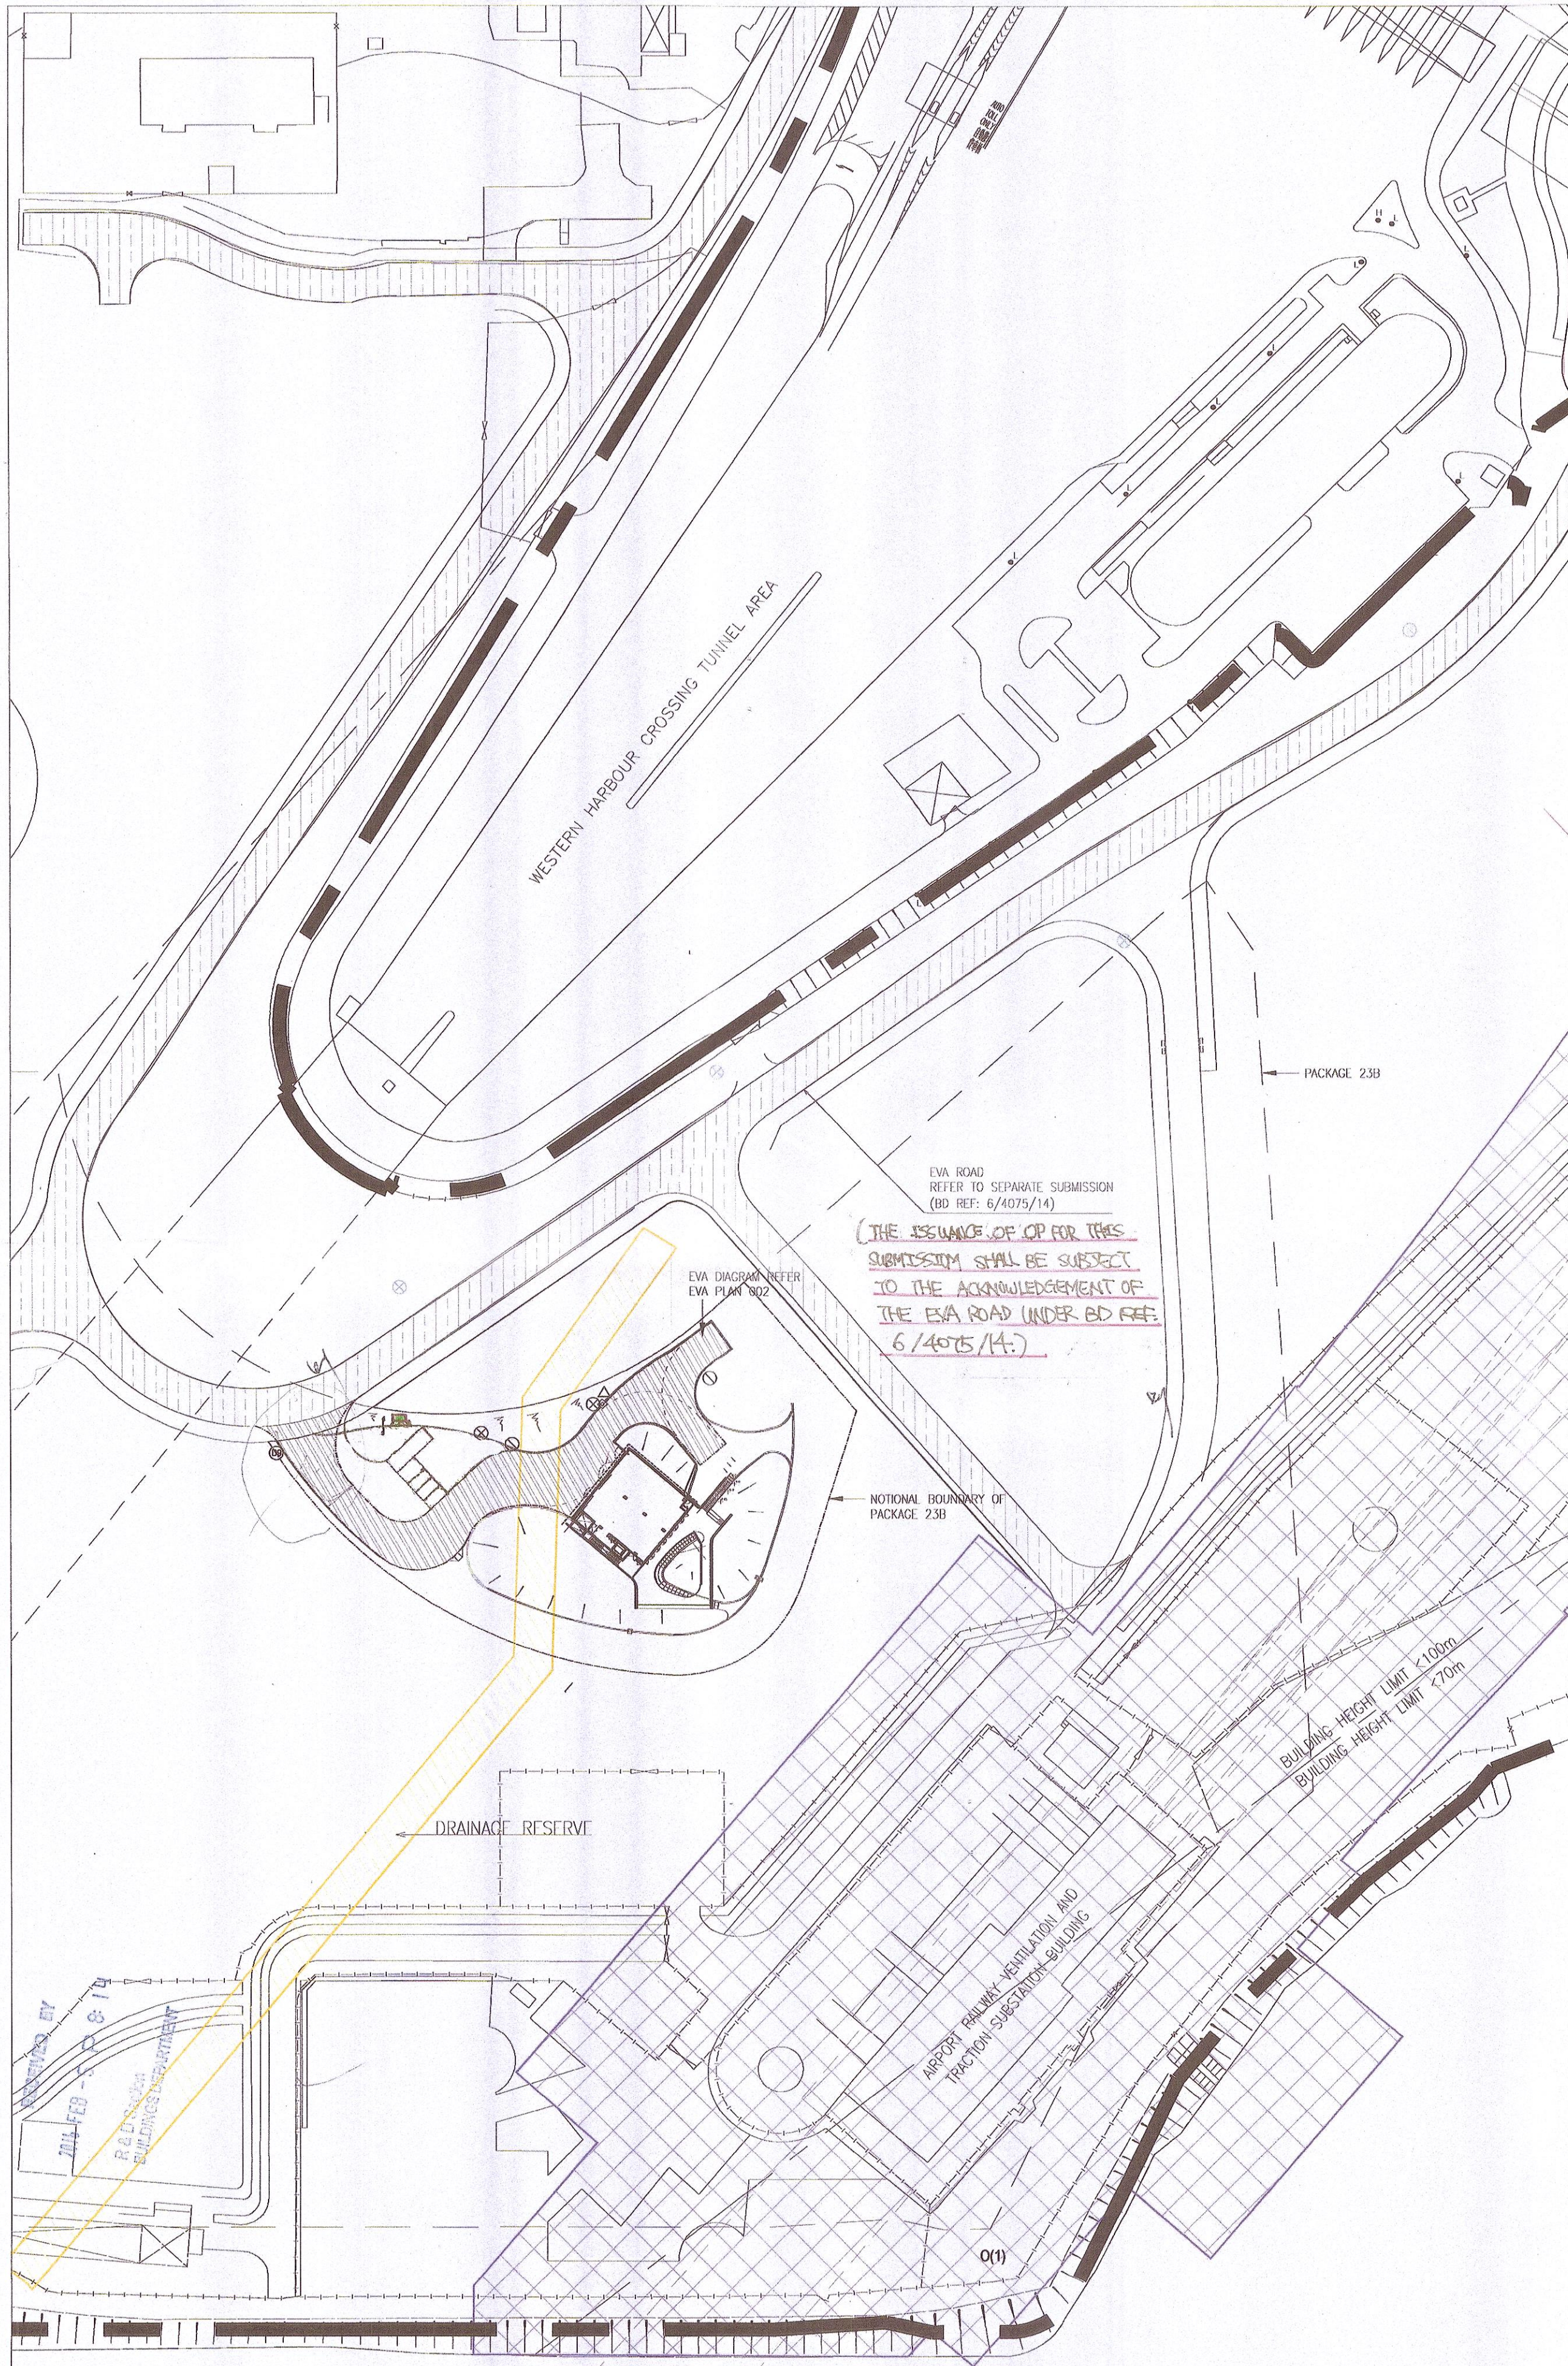


001 MASTER LAYOUT PLAN SCALE 1:1000

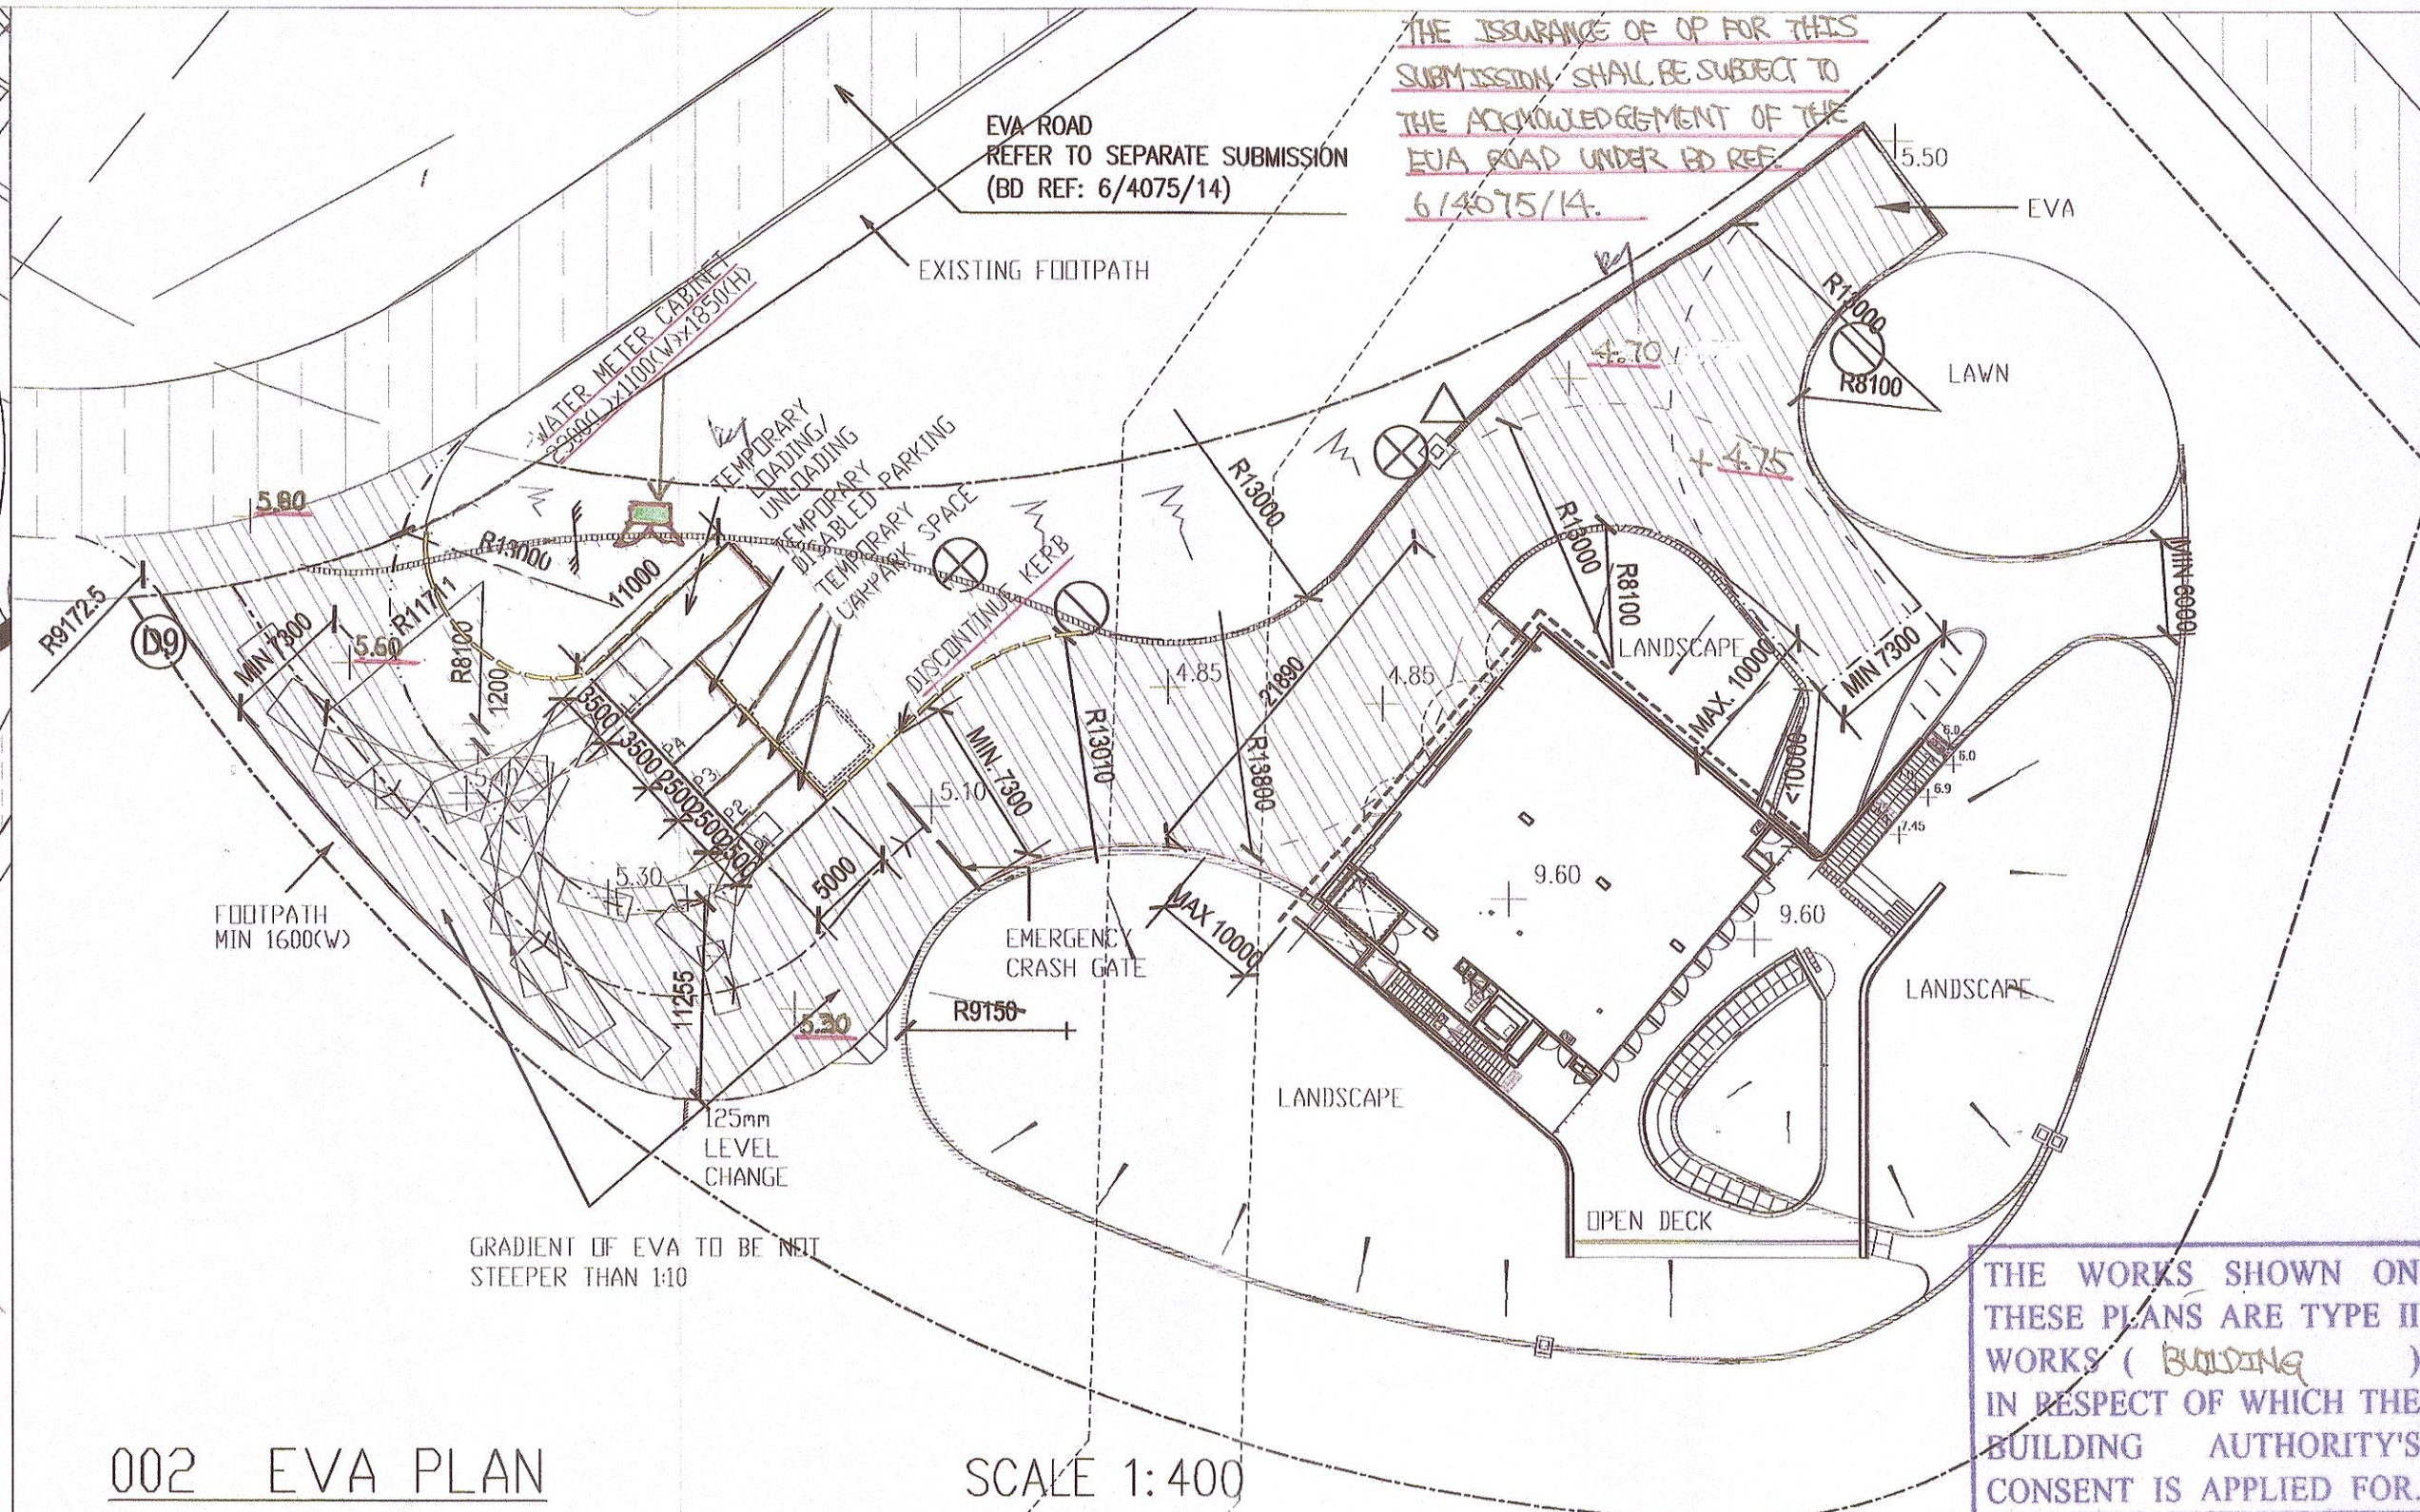

002 EVA PLAN

SCALE 1:400

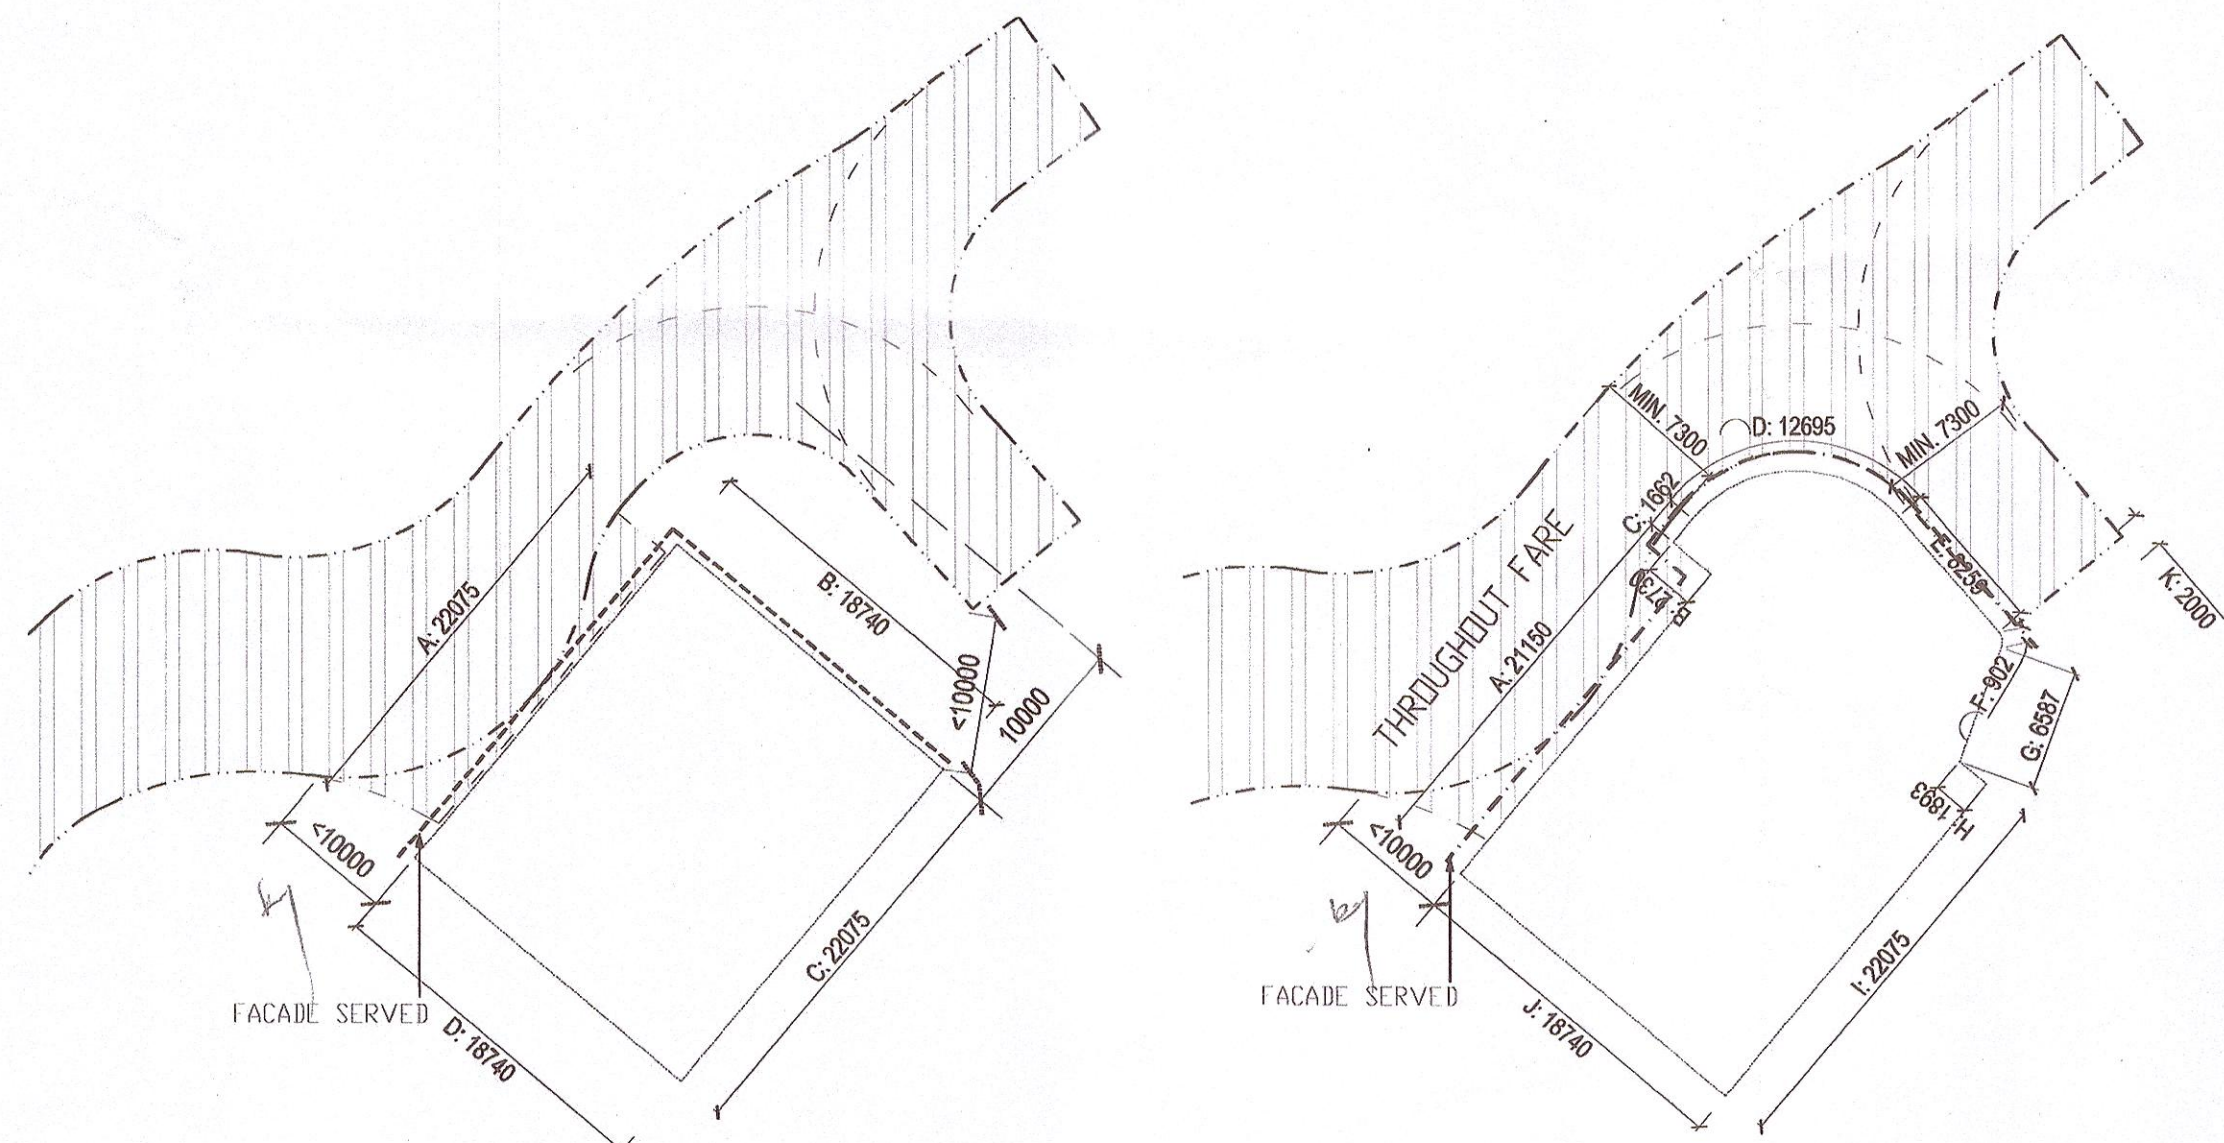

LENGTH CALCULATION OF
FACADE TO BE SERVED BY EVA
PERIMETER : A + B + C + D
= 22.075 + 18.740 + 22.075 + 18.740
= 81.630m
REQUIRED LENGTH : 81.630m x 0.5 = 40.815m
PROVIDED LENGTH : A + B
= 22.075 + 18.740
= 40.815m = 40.815m

LENGTH CALCULATION OF
FACADE TO BE SERVED BY THROUGHOUT FARE
PERIMETER : A + B + C + D + E + F + G + H + I + J
= 21.150 + 2.730 + 1.662 + 12.695 + 8.259
+ 0.902 + 6.587 + 1.893 + 22.075 + 18.740
= 96.693
REQUIRED LENGTH : 96.693m x 0.5 = 48.347m
PROVIDED LENGTH : A + B + C + D + E + K
= 21.150 + 2.730 + 1.662 + 12.695 + 8.259
+ 2.000
= 48.496m > 48.347m

Plan Approved
YEUNG Yee-man, Ella
Senior Building Surveyor
for BUILDING AUTHORITY
- 4 MAR 2016

Note: This plan has been processed on a
curtailed check basis under the centralized
processing system as promulgated in PNAP
ADM-19. The duties of the authorized person,
registered structural engineer and/or registered
geotechnical engineer concerned as specified
under section 4(3)(b) and the provision of
section 14(2)(c) of the Buildings Ordinance are
of particular relevance in this regard.

DENNIS W. C. WONG
SSE (Hons), C. Eng., MStructE, MInstE,
MRICS, MRAS, RPS, RPE, R1
Authorized Person
Registered Structural Engineer

B.D. REF: BD 2/4027/14
F.S.D. REF: FP 8/27927 (B)
NOTES:

FINAL AMENDMENT

LEGEND:

- EMERGENCY VEHICULAR ACCESS (TO BE PROVIDED IN HARD PAVING & DESIGNATED FOR FIRE APPLIANCE OF 30 TONNES)
- PERMANENT ROAD TO BE COMPLETED BEFORE OP TO BE SUBMITTED BY OTHERS SEPARATELY
- D9 EVA LAYOUT SIGN AT ENTRANCE (D9)
- EVA INDICATION SIGN (D10)
- EVA "NO PARKING" INDICATION SIGN
- STREET FIRE HYDRANT
- LINE OF FACADE SERVED BY EVA
- LINE OF FACADE SERVED BY THROUGHOUT FARE

AUTHORIZED PERSON:

Dennis W.C. Wong
SSE (Hons), MStructE, MInstE,
MRICS, MRAS, RPS, RPE,
Authorized Person
Registered Structural Engineer

REV.	DATE	DESCRIPTION	INITIAL
04	15-01-2015	AMENDMENT C (FINAL AMENDMENT)	IC
03	20-08-2015	AMENDMENT B	HW
02	30-01-2015	AMENDMENT A	ZC
01	25-08-2014	RESUBMISSION	ZC
00	12-06-2014	FIRST SUBMISSION	ZC

LEAD ARCHITECT:

VPANG ARCHITECTS

ARCHITECT:

JET ARCHITECTURE

AUTHORIZED PERSON & REGISTERED STRUCTURAL ENGINEER:

aurecon

REGISTERED GEOTECHNICAL ENGINEER:

HUNG CHI CONSULTANTS LTD.

LANDSCAPE CONSULTANT:

SOSCAPE

JOB TITLE
ARTS PAVILION
AT WEST KOWLOON CULTURAL DISTRICT
LOT NO. STT KX2844

DRAWING TITLE
MASTER LAYOUT PLAN
& EVA PLAN

SCALE	AS SHOWN	PRINTED	15-07-2015
CHECKED	LC	DATE	10-07-2015
APPROVED	LC	DATE	10-07-2015
DRAWN	HW	DATE	10-07-2015

CONTRACT NO. PA/2014/3B/051

DRAWING NO. 3B52X-ARC-DWG-P01-L000-0002-GBP-XA 04

CAD REF NAME: 3B52X-ARC-DWG-P01-L000-0002-GBP-XA

DEVELOPER

westKowloon
西九文化區