



G.F.A. CALCULATION

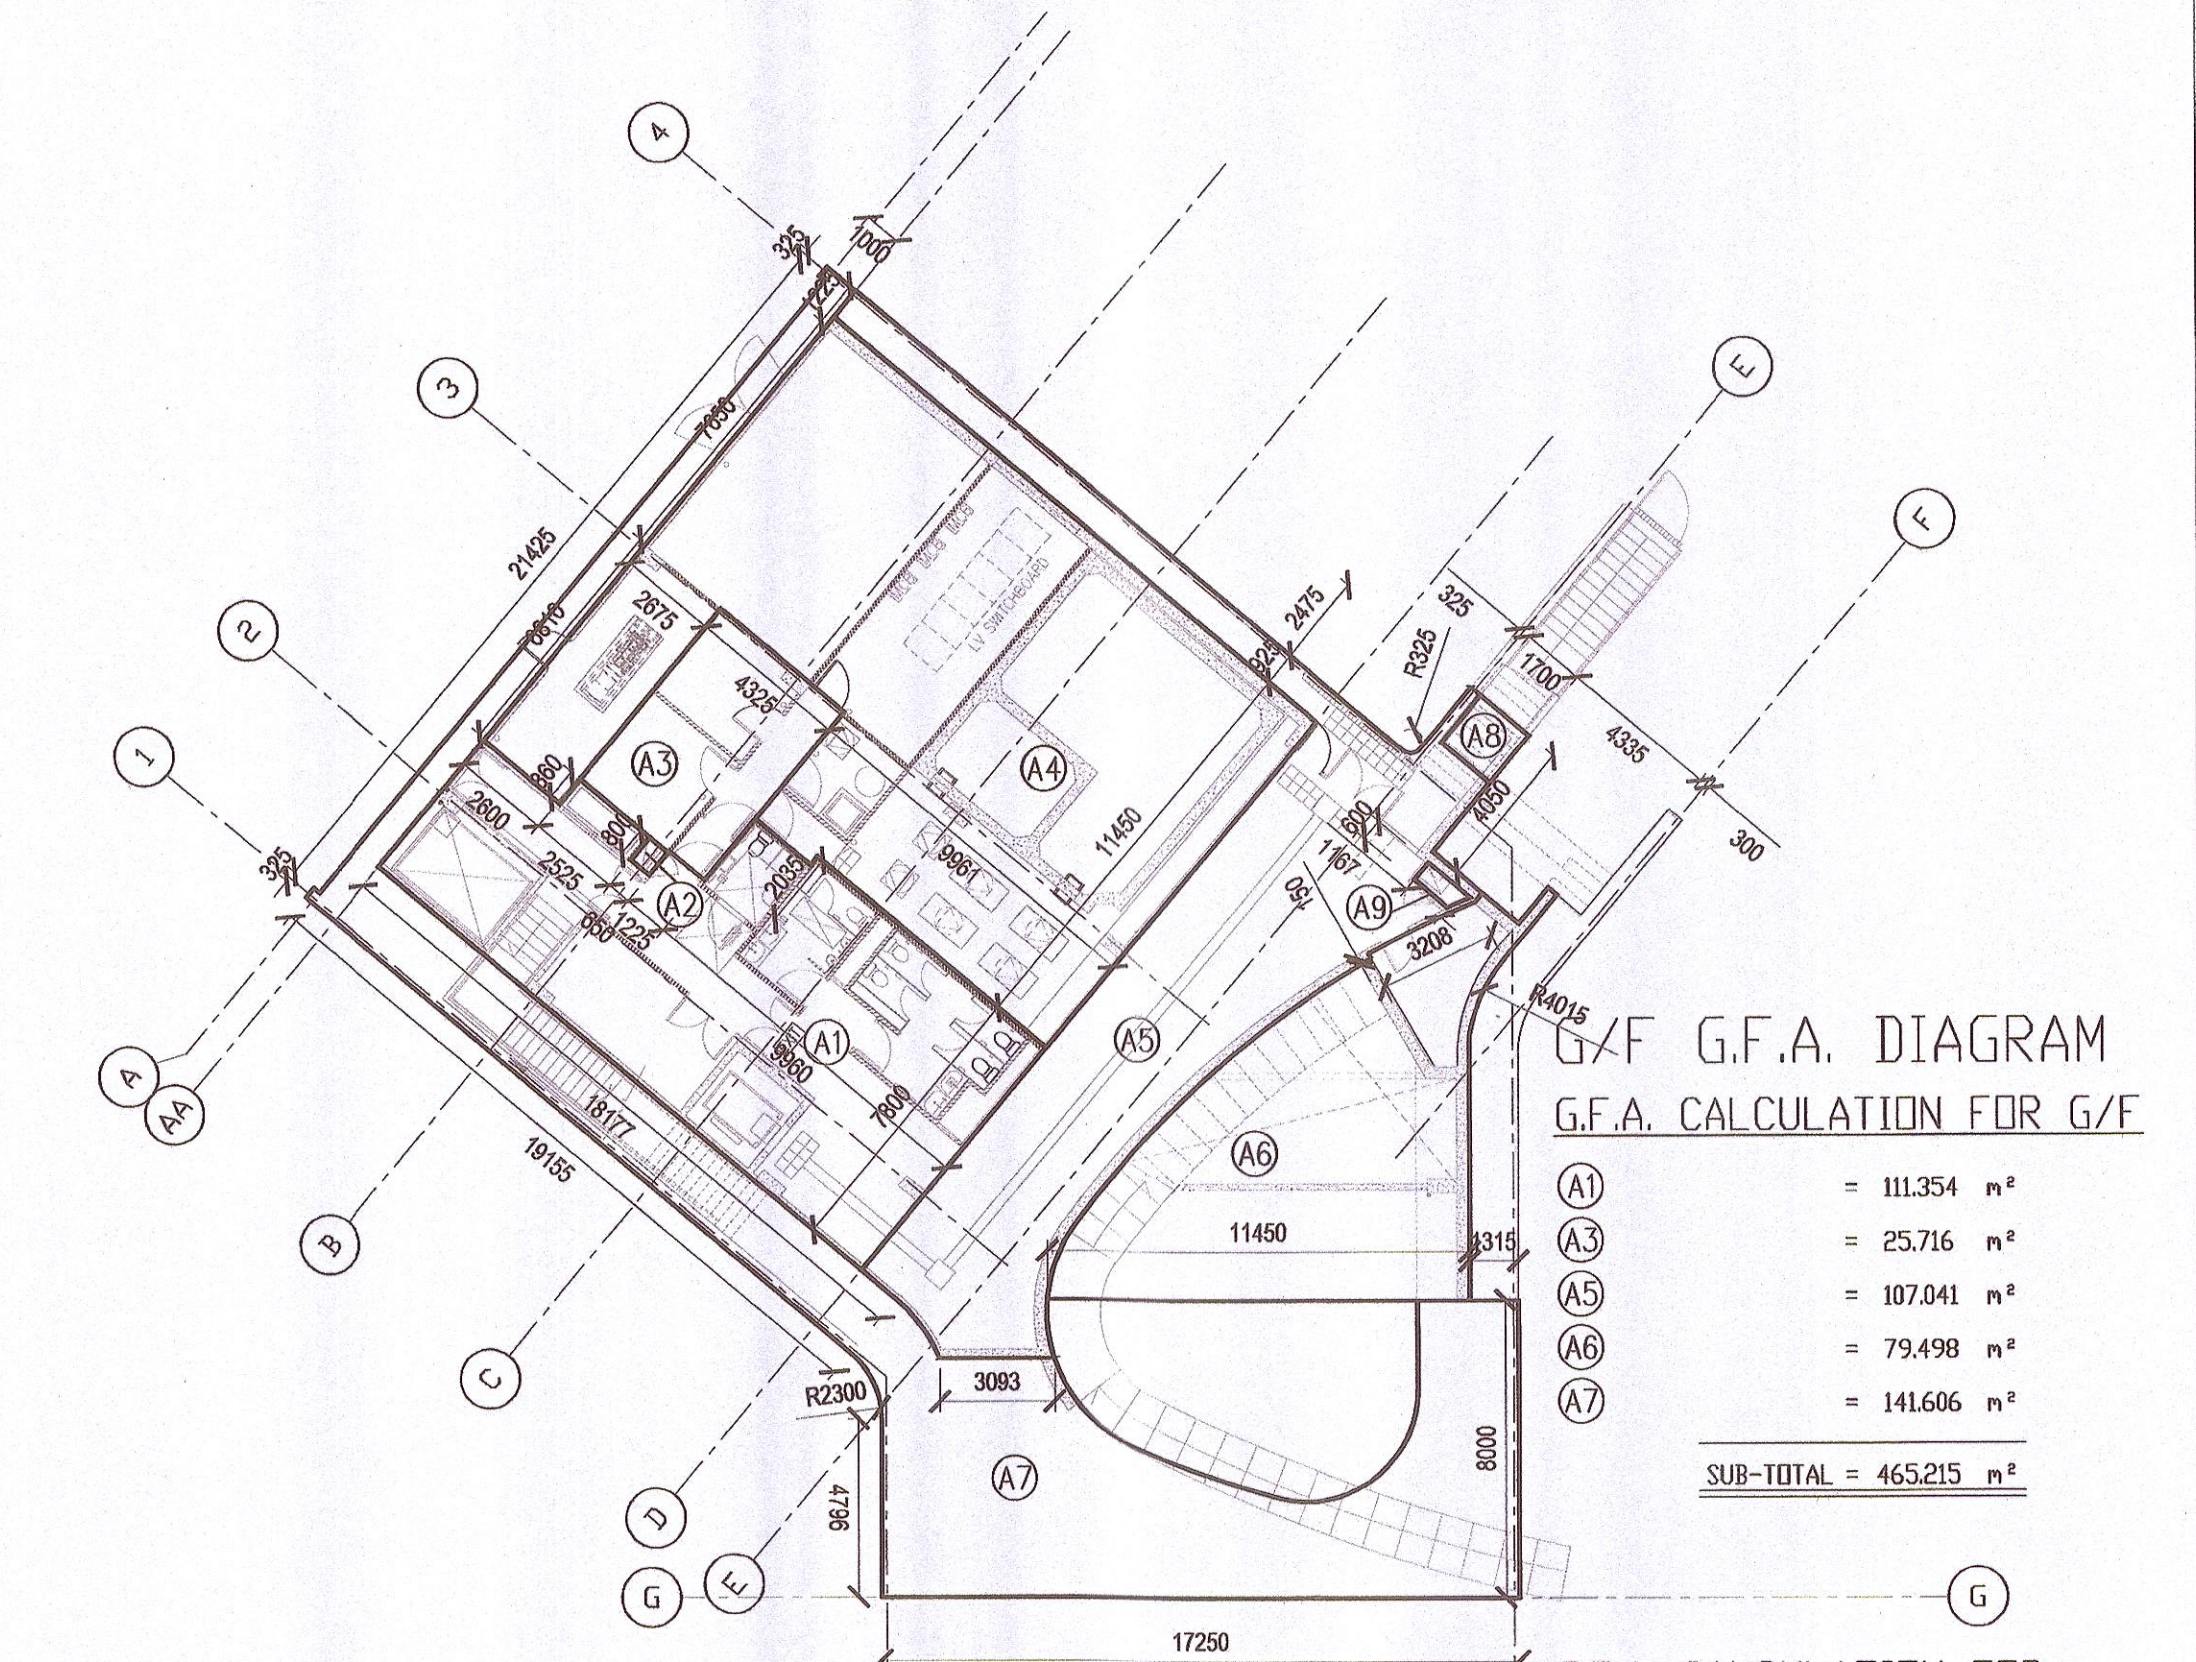

SCHEDULE OF NON-DOMESTIC G.F.A.


FLOOR	NON-DOMESTIC G.F.A.
G/F	464.506
1/F	412.685
TOTAL	877.191

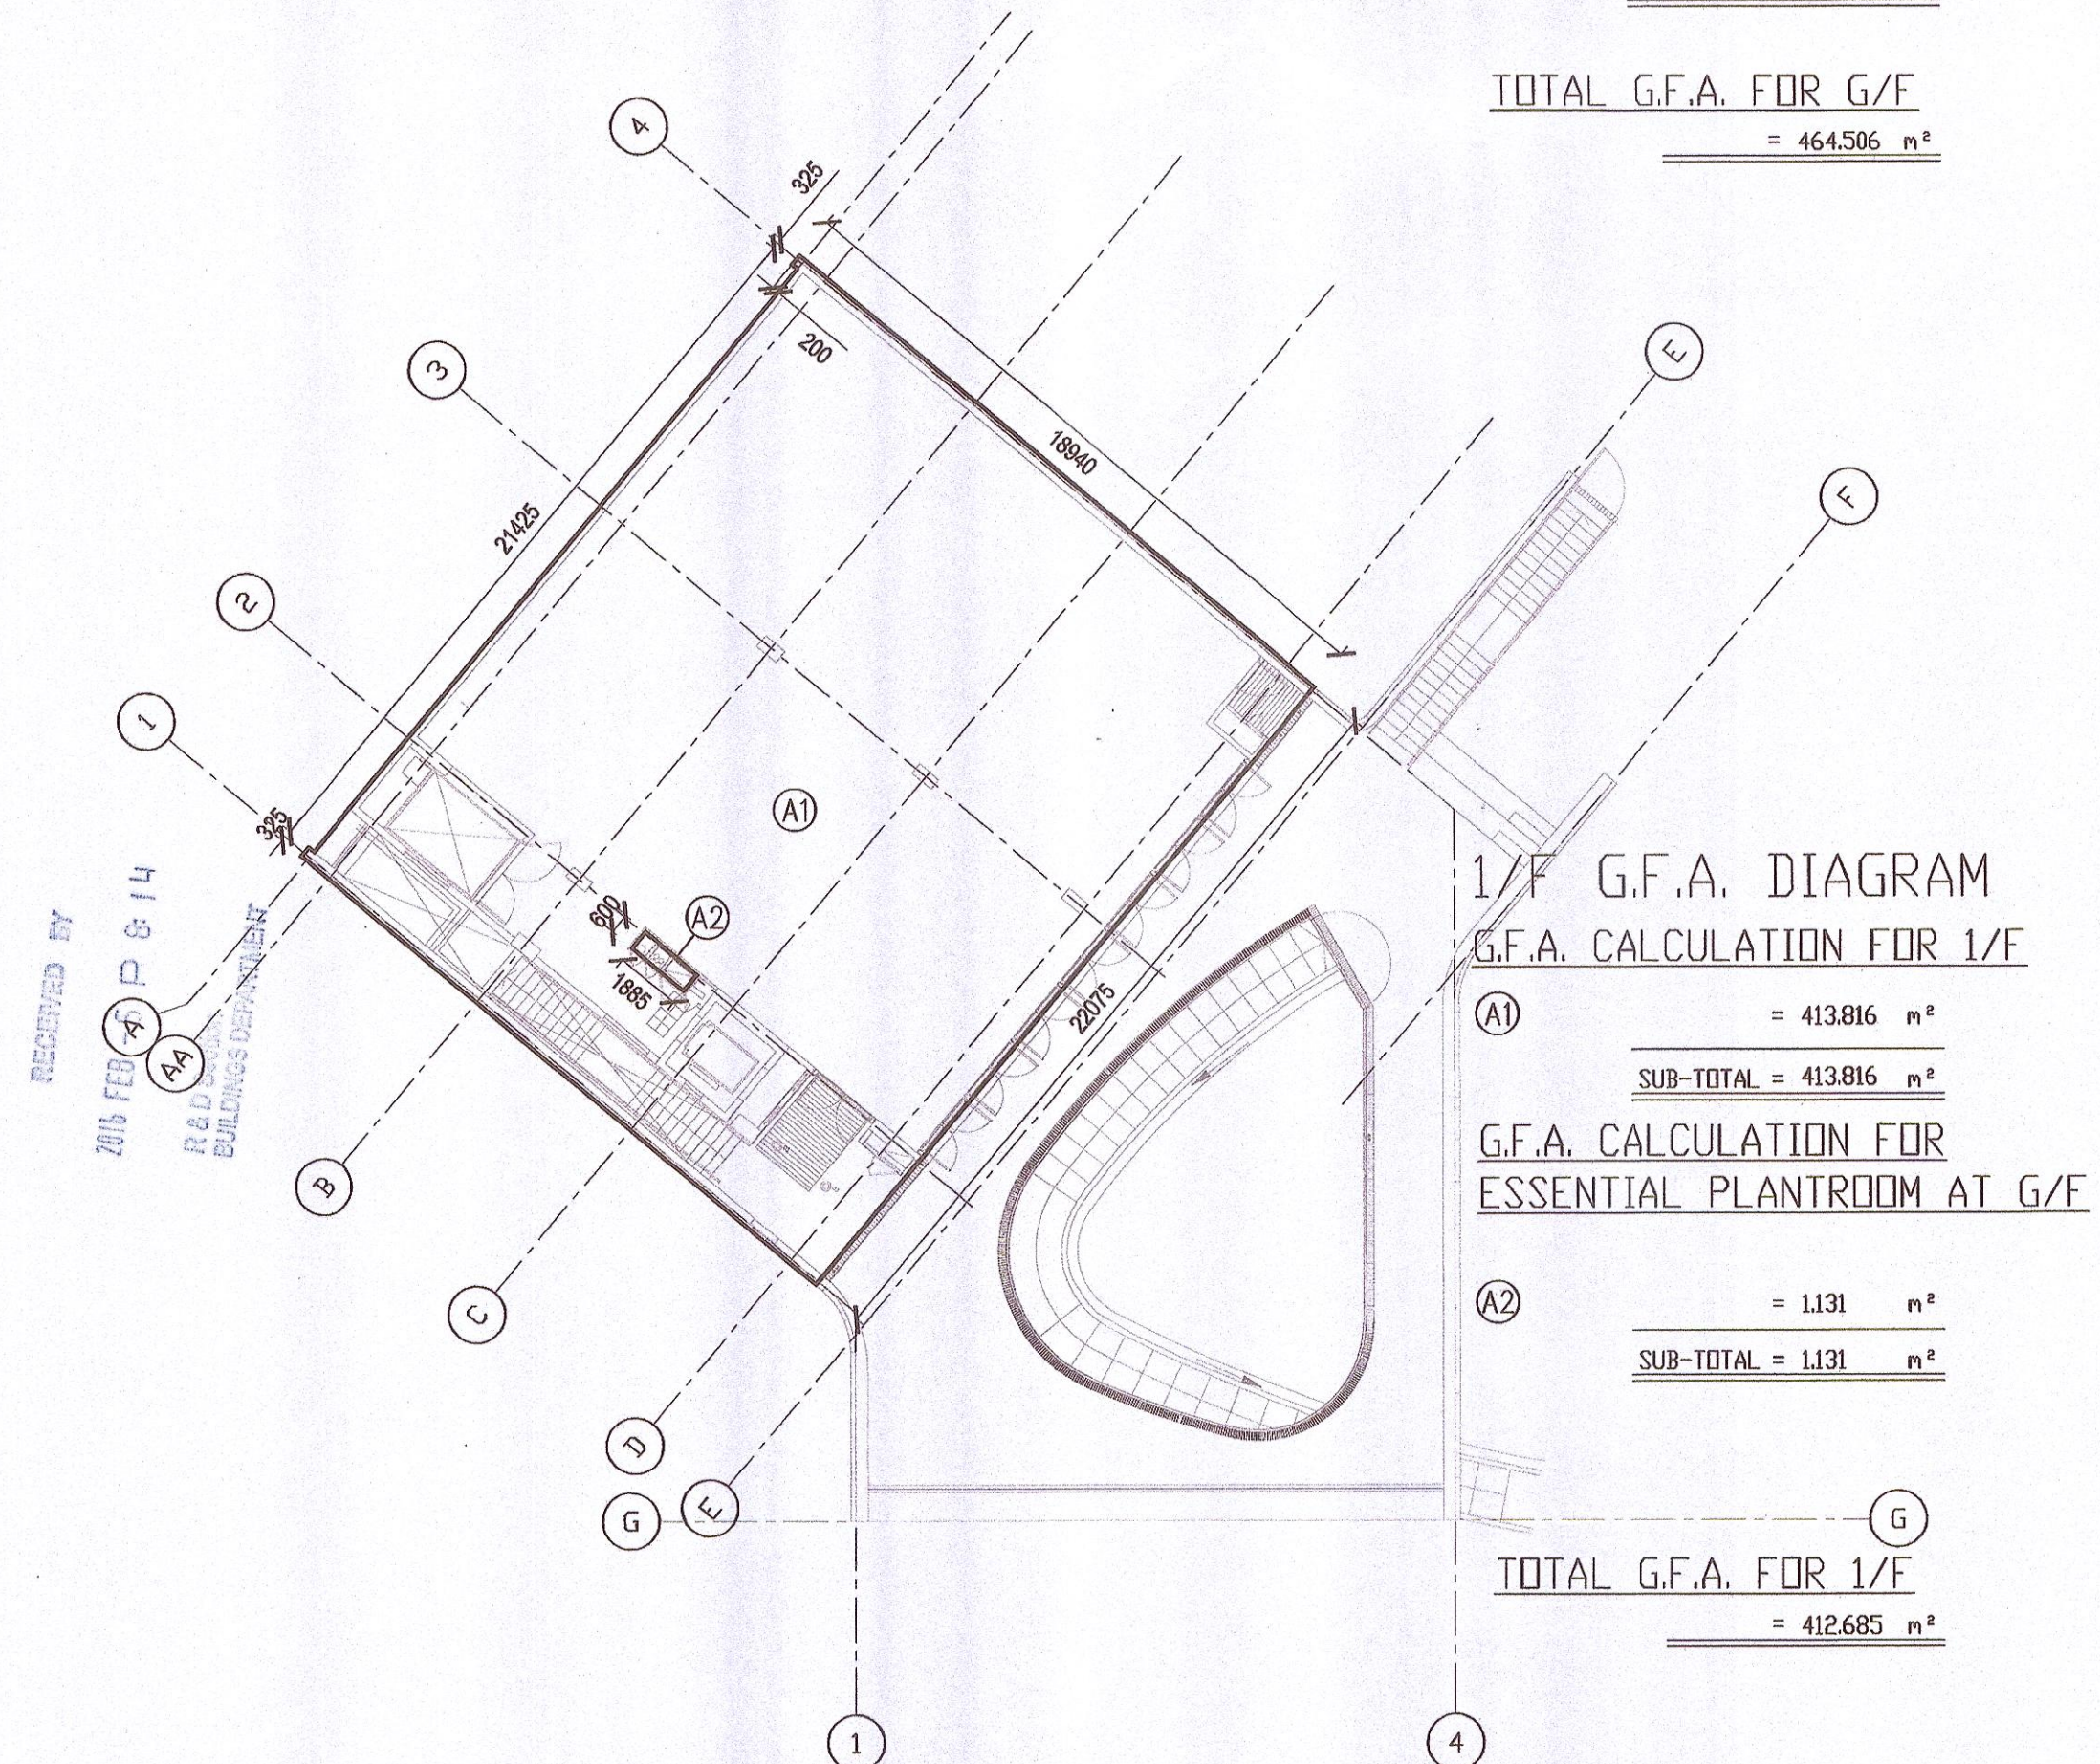

U.F.A. CALCULATION

SCHEDULE OF NON-DOMESTIC U.F.A.

FLOOR	ROOM	U.F.A.
G/F	INFO. COUNTER	3.403 m ²
	OFFICE CUM STORAGE	12.615 m ²
	STORE ROOM	8.380 m ²
1/F	EXHIBITION AREA	326.249 m ²
TOTAL		350.647 m²

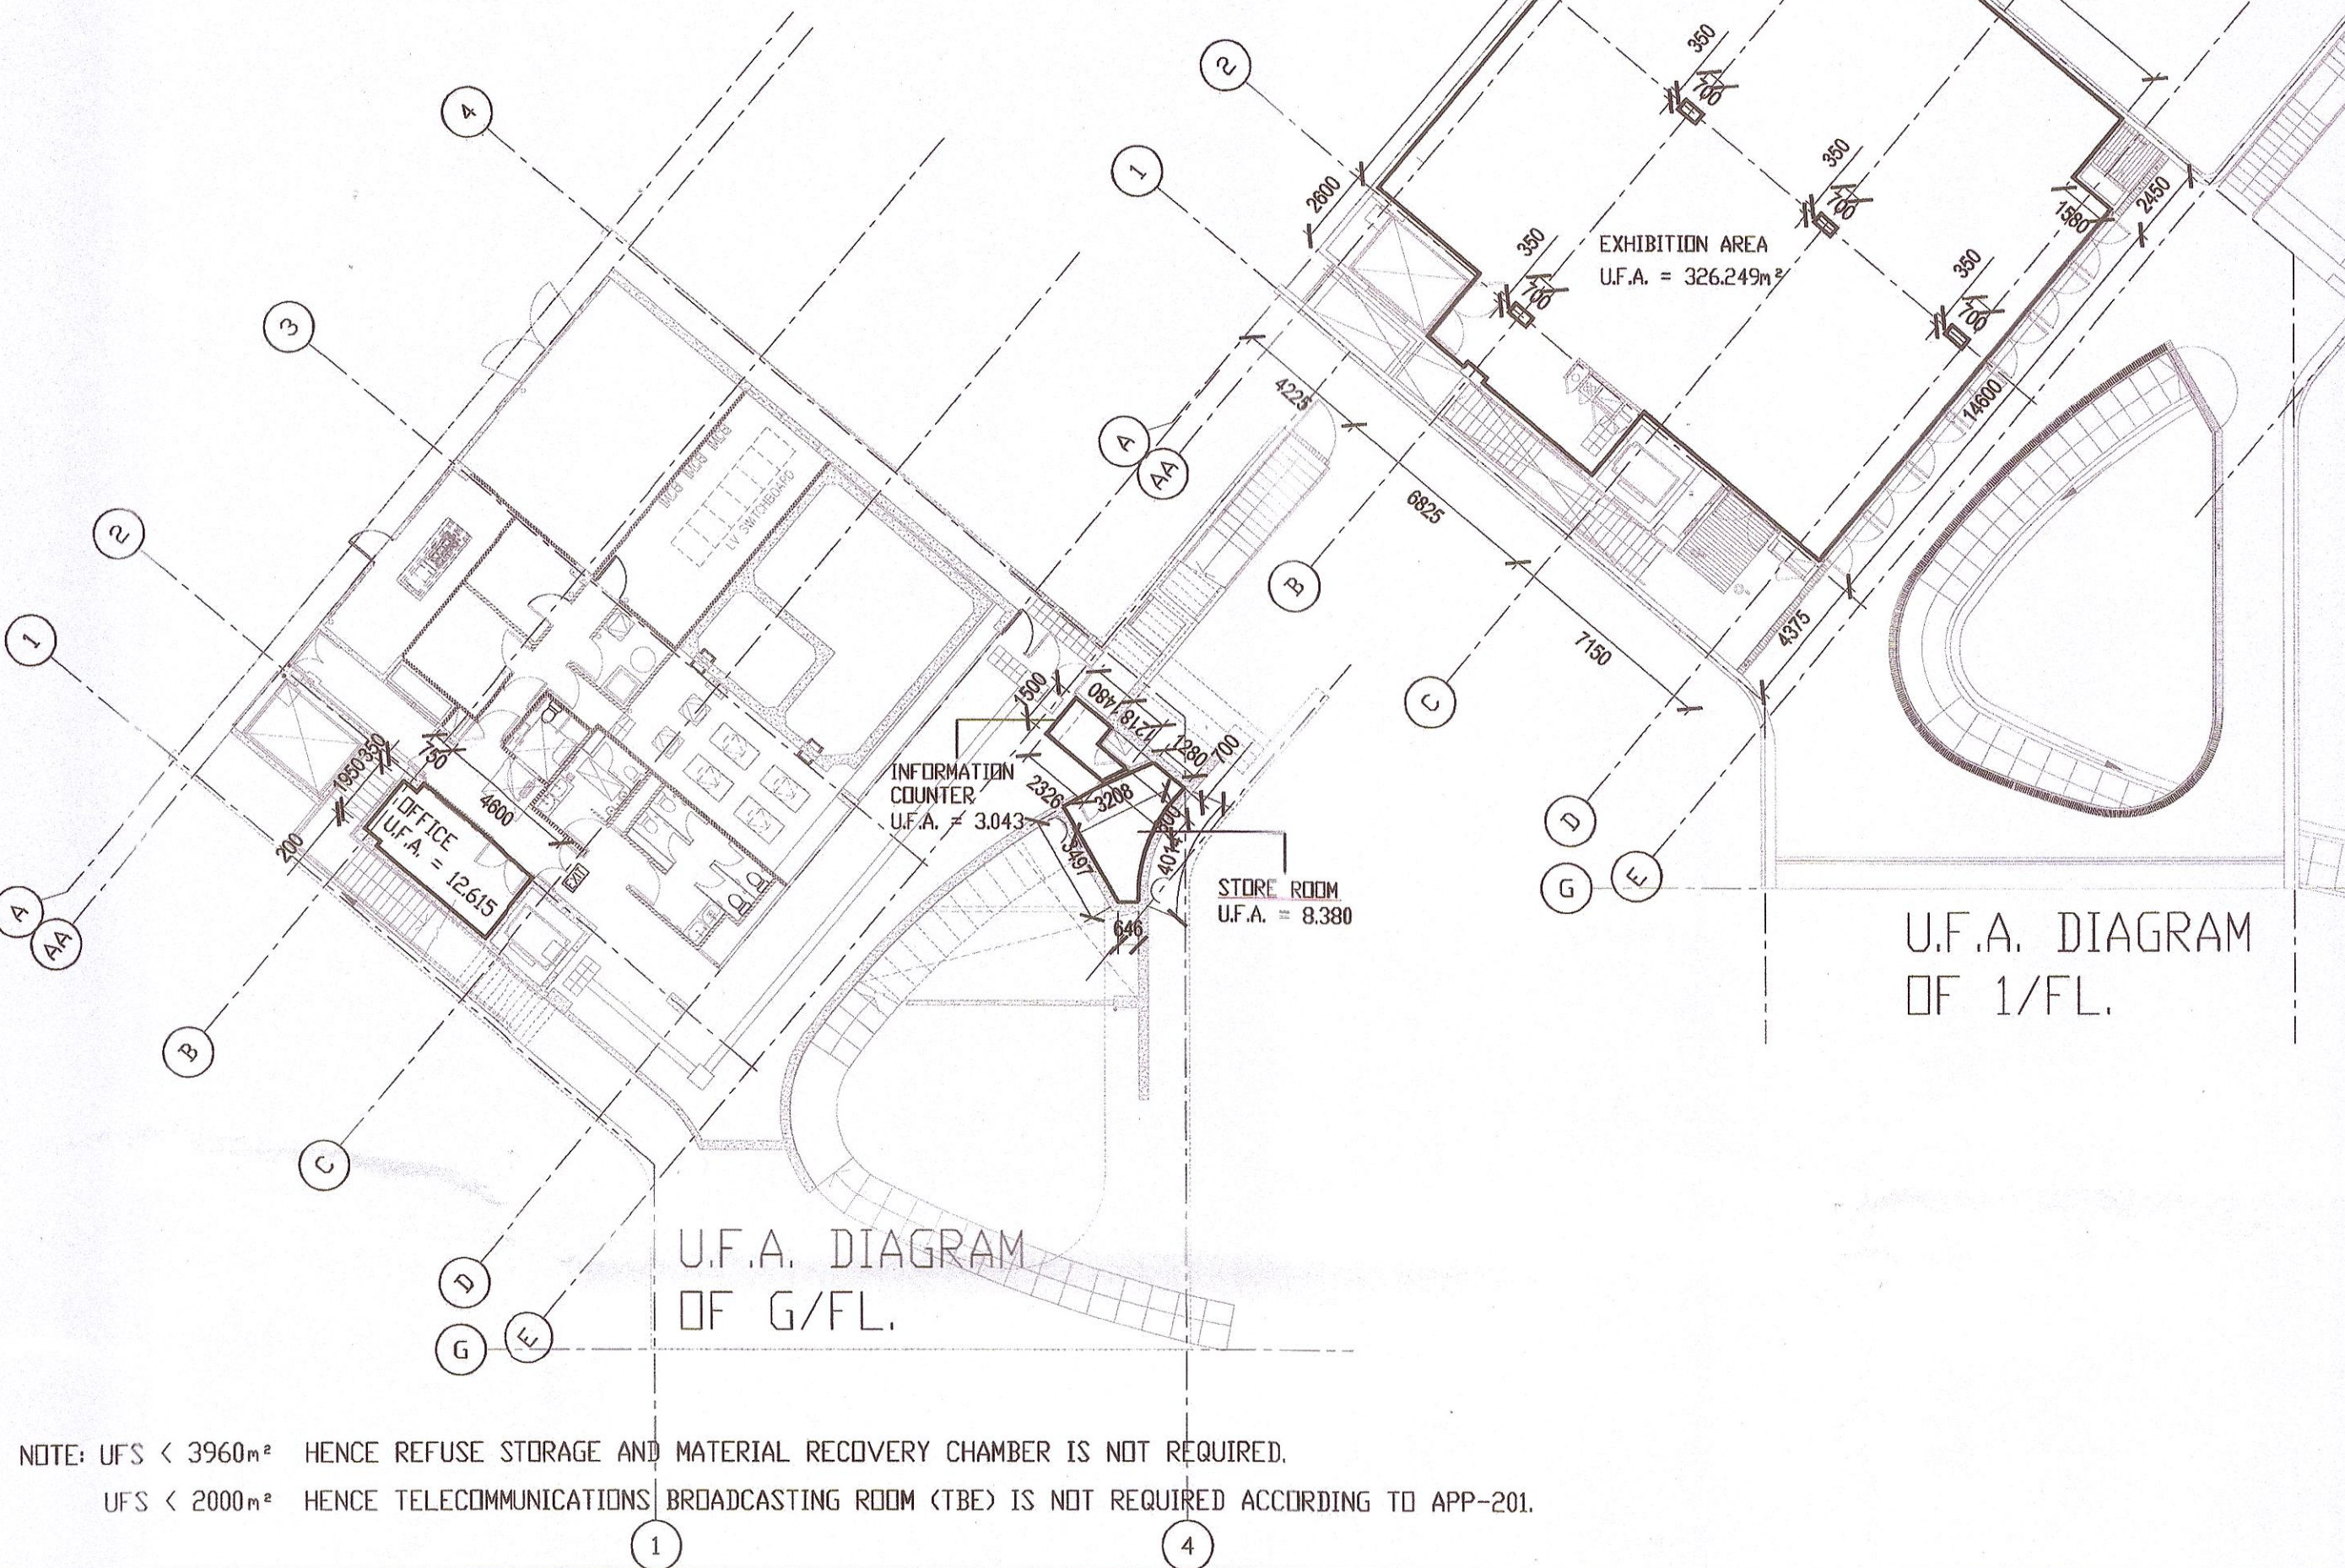

SITE COVERAGE CALCULATION

SITE COVERAGE DIAGRAM

NON-DOMESTIC COVERED AREA	(A1) = 744.516 m ²
TOTAL	= 744.516 m²

B.D. REF: BD 2/4027/14
F.S.D. REF: FP 8/27927 (B)
NOTES:

FINAL AMENDMENT

THE WORKS SHOWN ON THESE PLANS ARE TYPE II WORKS (BUILDING) IN RESPECT OF WHICH THE BUILDING AUTHORITY'S CONSENT IS APPLIED FOR.

AUTHORIZED PERSON :

Dennis W.C. Wong
BSc (Hons), MSc (Eng), MPhil, MRICS, MIMAR, RPS, RPE, Authorized Person Registered Structural Engineer

04	15-01-2015	AMENDMENT C (FINAL AMENDMENT)	IC
03	20-08-2015	AMENDMENT B	HW
02	30-01-2015	AMENDMENT A	ZC
01	25-08-2014	RESUBMISSION	ZC
00	12-06-2014	FIRST SUBMISSION	ZC
REV.	DATE	DESCRIPTION	INITIAL

LEAD ARCHITECT:

VPRANG ARCHITECTS

ARCHITECT:

JET ARCHITECTURE

AUTHORIZED PERSON & REGISTERED STRUCTURAL ENGINEER:

PRUDENTIAL SURVEYORS (H.K.) LTD.
111, 25078333 FAX: 25080576

BUILDING SERVICES ENGINEER:

aurecon

REGISTERED GEOTECHNICAL ENGINEER:

HUNG CHI CONSULTANTS LTD.

LANDSCAPE CONSULTANT:

SOSCAPE LANDSCAPE ARCHITECTURE

JOB TITLE
ARTS PAVILION
AT WEST KOWLOON CULTURAL DISTRICT
LOT NO. STT NO. KX2844

DRAWING TITLE
GFA, UFA AND SITE COVERAGE
DIAGRAM AND CALCULATION

SCALE	1:200 (A1)	PRINTED	15-01-2016
CHECKED	ZC	DATE	15-01-2016
APPROVED	LC	DATE	15-01-2016
DRAWN	ZC	DATE	15-01-2016

CONTRACT NO. PA/2014/3B/051

DRAWING NO. 3B52X-ARC-DWG-P01-L000-0003-GBP-XA

CAD REF NAME: 3B52X-ARC-DWG-P01-L000-0003-GBP-XA

DEVELOPER

westKowloon
西九文化區

Plan Approved
YEUNG Yee-man, Ella
Senior Building Surveyor
for BUILDING AUTHORITY
4 MAR 2016

Note: This plan has been processed on a curtailed check basis under the centralized processing system as promulgated in PHAP ADM-19. The duties of the authorized person, registered structural engineer and/or registered geotechnical engineer concerned as specified under section 4(3)(b) and the provision of section 14(2)(c) of the Buildings Ordinance are of particular relevance in this regard.

DENNIS W. C. WONG
BSc (Hons), C. Eng., MIMAR, MPhil, MRICS, MIMAR, RPS, RPE, R1
Authorized Person
Registered Structural Engineer