

B.D. REF: BD 2/4027/14
F.S.D. REF: FP 8/27927 (B)
NOTES:

FINAL AMENDMENT

THE WORKS SHOWN ON
THESE PLANS ARE TYPE II
WORKS (BUILDING)
IN RESPECT OF WHICH THE
BUILDING AUTHORITY'S
CONSENT IS APPLIED FOR.

AUTHORIZED PERSON:

Dennis W.C. Wong
BS (Eng), MS (Struct), MEng,
MACE, MARS, RPS, RPE,
Authorized Person
Registered Structural Engineer

04	15-01-2015	AMENDMENT C (FINAL AMENDMENT)	IC
03	20-08-2015	AMENDMENT B	HW
02	30-01-2015	AMENDMENT A	ZC
01	25-08-2014	RESUBMISSION	ZC
00	12-06-2014	FIRST SUBMISSION	ZC
REV.	DATE	DESCRIPTION	INITIAL

LEAD ARCHITECT:

VPANG
ARCHITECTS

ARCHITECT:

JET ARCHITECTURE

AUTHORIZED PERSON & REGISTERED STRUCTURAL ENGINEER:

PRINCIPAL SURVEYORS (INT'L) LTD.
TEL: 25078333 FAX: 25088576

BUILDING SERVICES ENGINEER:

aurecon

REGISTERED GEOTECHNICAL ENGINEER:

HUNG CHI CONSULTANTS LTD.

LANDSCAPE CONSULTANT:

SOSCAPE
LANDSCAPE ARCHITECTURE

JOB TITLE

ARTS PAVILION
AT WEST KOWLOON CULTURAL DISTRICT
LOT NO. STT NO. KX2844

DRAWING TITLE

G/F, 1/F & R/F PLAN

SCALE 1:200 (A1) PRINTED 22-08-2015

CHECKED ZC DATE 20-08-2015

APPROVED LC DATE 20-12-2015

DRAWN ZC DATE 10-12-2015


CONTRACT NO. PA/2014/3B/051

DRAWING NO. 3B52X-ARC-DWG-P01-L000-1001-GBP-XA REV. 04

CAD REF NAME: 3B52X-ARC-DWG-P01-L000-1001-GBP-XA

DEVELOPER

westKowloon
西九文化區

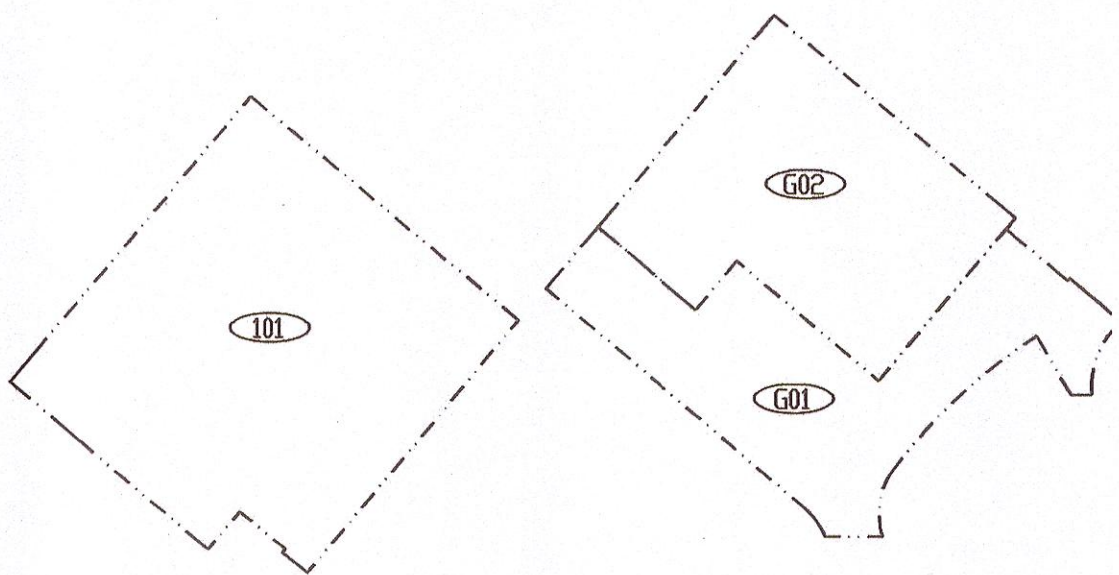

1/F. COMPARTMENTATION DIAGRAM G/F. COMPARTMENTATION DIAGRAM

SCHEDULE OF COMPARTMENTATION

COMPARTMENT	COMPARTMENTATION (AREA)	COMPARTMENTATION (VOLUME)
101	365.388 m ²	365.388 X 4.55MKH = 1662.515 m ³
G01	201.251 m ²	201.251 X 4.55MKH = 915.692 m ³
G02	218.239 m ²	218.239 X 4.55MKH = 992.987 m ³

FIRST FLOOR PLAN

ROOF FLOOR PLAN

GROUND FLOOR PLAN

Plan Approved

YEUNG Yee-man, Ella
Senior Building Surveyor
for BUILDING AUTHORITY
- 4 MAR 2016

Note: This plan has been processed on a
curtailed check basis under the centralized
processing system as promulgated in PNAP
ADM-19. The duties of the authorized person,
registered structural engineer and/or registered
geotechnical engineer concerned as specified
under section 4(3)(b) and the provision of
section 14(2)(c) of the Buildings Ordinance are
of particular relevance in this regard.

DENNIS W. C. WONG
BS (Eng), C. Eng., MEng, MACE,
MARS, MARS, RPS, RPE, M
Authorized Person
Registered Structural Engineer