


B.D. REF: BD 2/4062/14(P)
F.S.D. REF: FP 8/27927(D)/1

KEY PLAN

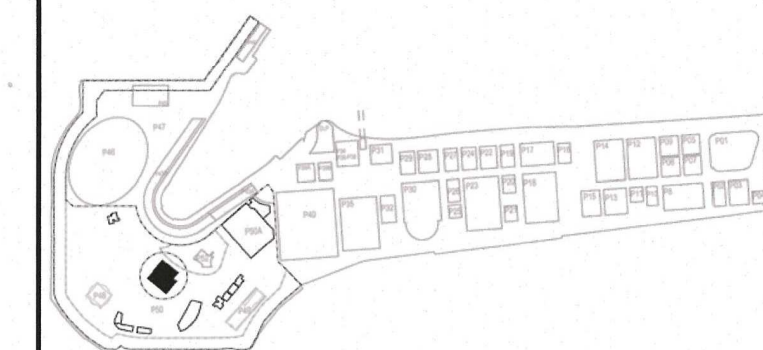

KEY PLAN

NOTES:

LANDSCAPE AREA

Note: This plan has been processed on a curtailed check basis under the centralized processing system as promulgated in PNAP ADM-19. The duties of the authorized person, registered structural engineer and/or registered geotechnical engineer concerned as specified under section 4(3)(b) and the provision of section 14(2)(c) of the Buildings Ordinance are of particular relevance in this regard.

Plan Approved

LI Ming-chun, Gordon
Senior Building Surveyor
for BUILDING AUTHORITY
18 MAR 2019

FOR BD APPROVAL



REV.	DATE	DESCRIPTION	INITIAL
07	13/02/19	FINAL AMENDMENT	R.NG
06	19/12/18	FINAL AMENDMENT	R.NG
05	16/10/18	FINAL AMENDMENT	R.NG
04	25/05/18	FINAL AMENDMENT	R.TANG
03	18/12/17	THIRD AMENDMENT	R.TANG
02	07/06/17	SECOND AMENDMENT	R.TANG
01	22/04/16	FIRST AMENDMENT	R.NG
00	02/12/15	FIRST SUBMISSION	R.NG

LEAD CONSULTANT & ARCHITECT	Dennis Lau & Ng Chun Man Architects & Engineers (HK) Ltd. 48/F, Tower 1, Times Square, Matheson Street Hong Kong
THEATRE PLANNING CONSULTANT	Theatreplan LLP 27 Colonnade, London WC1N 1JA United Kingdom
CIVIL, GEO-TECHNICAL, STRUCTURAL, BUILDING SERVICES & ENVIRONMENTAL ENGINEER	ARCADIS 20/F, AXA Tower Landmark East 100 How Ming Street Kowloon, Kowloon Hong Kong
PROJECT LANDSCAPE ARCHITECT	ACLA Limited 20/F, AXA Tower Landmark East 100 How Ming Street Kowloon, Kowloon Hong Kong
PROJECT QUANTITY SURVEYOR	Rider Levett Bucknall 20th Floor, Eastern Central Plaza, 3 Yu Hing Road, Shaohkwan, Hong Kong

JOB TITLE	THE PARK DEVELOPMENT FOR THE WEST KOWLOON CULTURAL DISTRICT
DRAWING TITLE	FREESPACE FREESPACE - GROUND FLOOR PLAN
SCALE	As indicated
CHECKED	BRUCE LAW
APPROVED	ARTHUR AU
DRAWN	R.TANG
DRAWING NO.	3B51X-ARC-DWG-P00-L000-1001-BGP
CAD REF NAME	3B51X-ARC-BIM-0000-P00-XXXX-WS5_rvt
AUTHORITY	

westKowloon
西九文化區

SECTION F-F
PROTECTED CORRIDOR
IN BETWEEN BOH AREA 2 AND LV.
SWITCH ROOM
SCALE 1:50

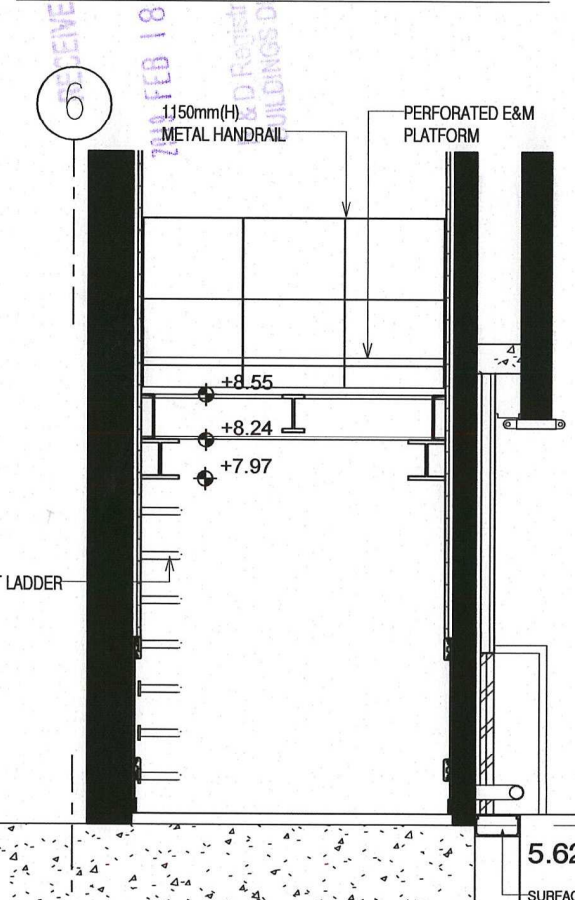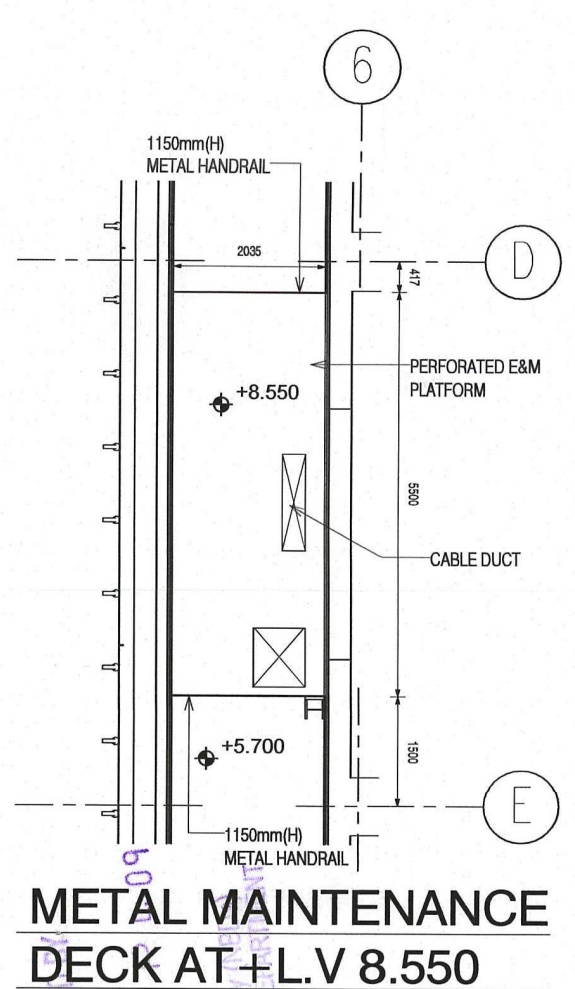

SECTION E-E
METAL MAINTENANCE
DECK
Scale 1:50

Scale 1:200

STATEMENT II: The works shown on these plans are Type II works in respect of which the Building Authority's consent is applied for.

Building (Amendment)