



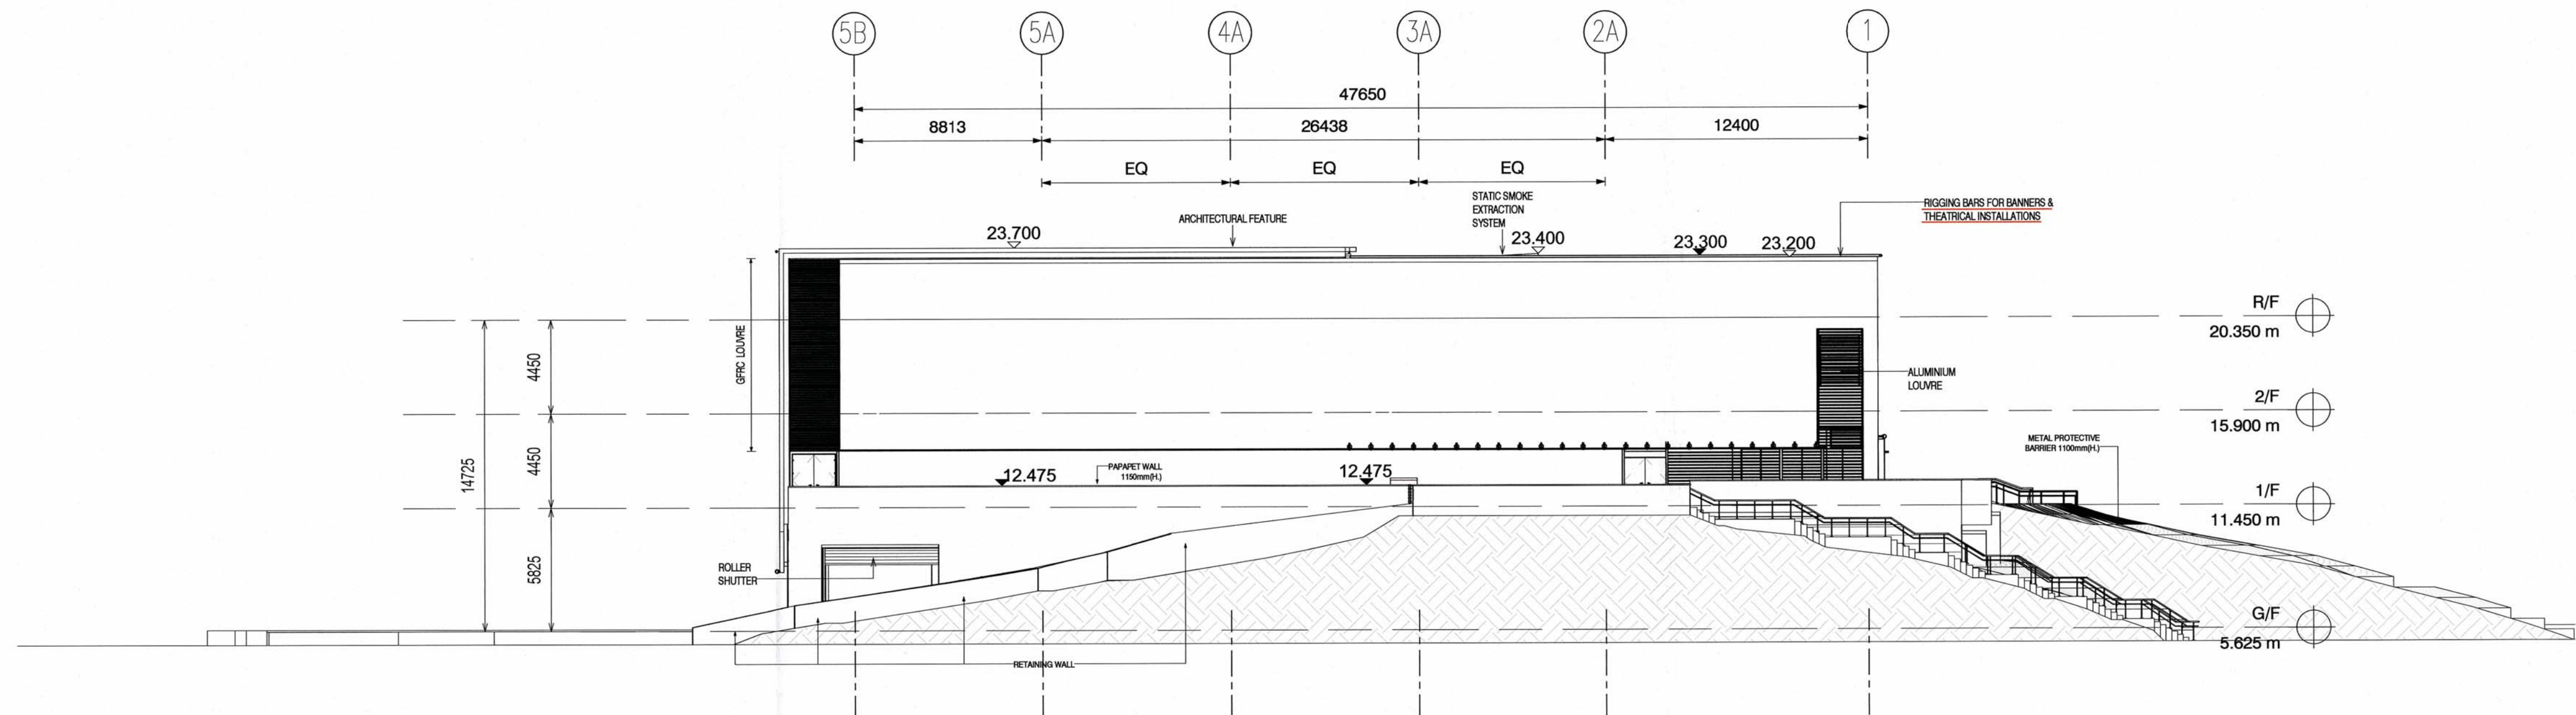


SOUTH ELEVATION

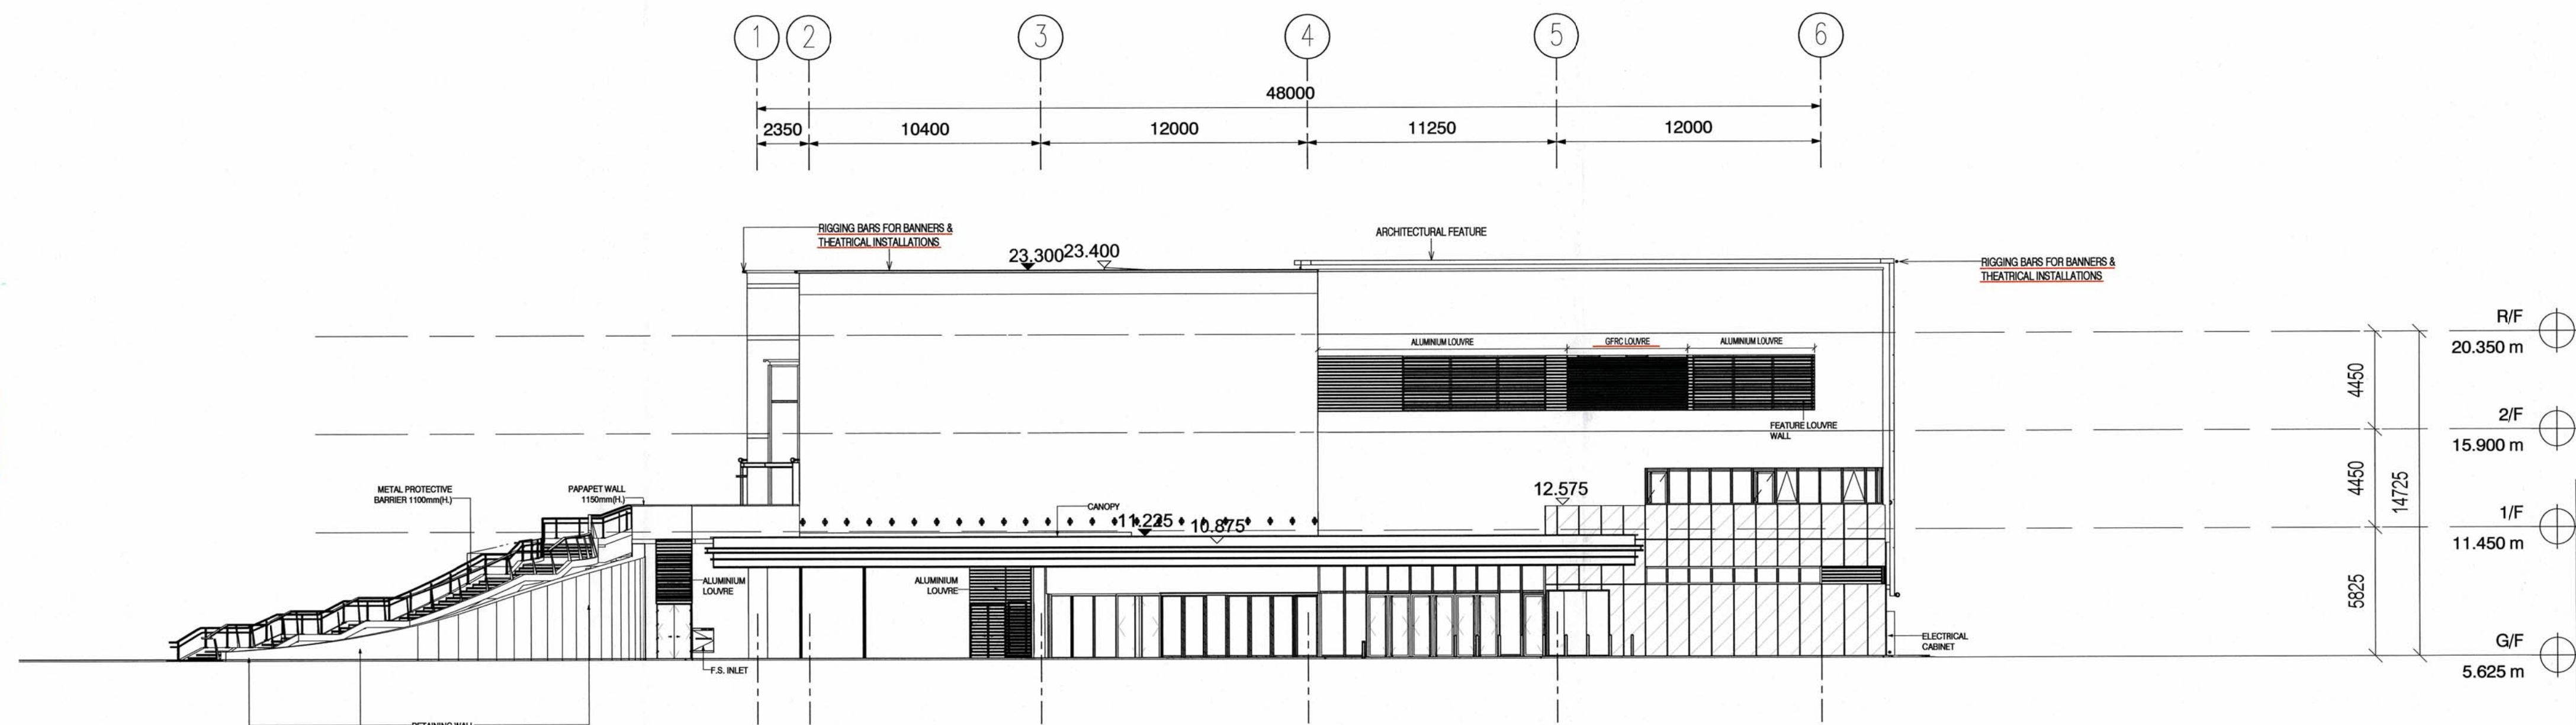

NORTH ELEVATION

B.D. REF: BD 2/4062/14(F)
F.S.D. REF: FP 8/27927(D)/1

KEY PLAN

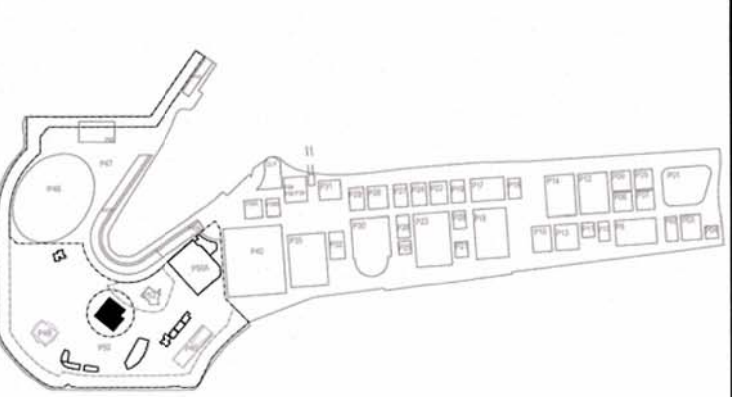

KEY PLAN

NOTES:

ALUMINIUM CLADDING

FOR BD APPROVAL

REV.	DATE	DESCRIPTION	INITIAL
04	25/05/18	FINAL AMENDMENT	R.TANG
03	18/12/17	THIRD AMENDMENT	R.TANG
02	07/06/17	SECOND AMENDMENT	R.TANG
01	22/04/16	FIRST AMENDMENT	R.NG
00	02/12/15	FIRST SUBMISSION	R.NG

LEAD CONSULTANT & ARCHITECT
DLN
Dennis Lau & Ng Chun Man Architects & Engineers (HK) Ltd.
46/F, Tower 1, Times Square,
Matheson Street
Causeway Bay
Hong Kong

THEATRE PLANNING CONSULTANT
theatreplan
Theatreplan LLP
27 Colindale Avenue, London WC1H 1JA
United Kingdom

CIVIL, GEO-TECHNICAL, STRUCTURAL,
BUILDING SERVICES &
ENVIRONMENTAL ENGINEER
ARCADIS
Arcadis Design & Consultancy
for Natural and Built Assets
28/F, AXA Tower Landmark East
100 How Ming Street
Kowloon, Kowloon
Hong Kong

PROJECT LANDSCAPE ARCHITECT
ACLA
ACL Limited
28/F, AXA Tower Landmark East
100 How Ming Street
Kowloon, Kowloon
Hong Kong

PROJECT QUANTITY SURVEYOR
利比 RLB Rider Levett Bucknall
28/F, AXA Tower Landmark East
100 How Ming Street
Kowloon, Kowloon
Hong Kong

JOB TITLE
THE PARK DEVELOPMENT FOR
THE WEST KOWLOON CULTURAL DISTRICT

DRAWING TITLE
FREESPACE
FREESPACE - ELEVATION NORTH AND SOUTH

SCALE	As indicated	PRINTED	A1
CHECKED	BRUCE LAW	DATE	09/04/18
APPROVED	ARTHUR AU	DATE	09/04/18
DRAWN	R.TANG	DATE	09/04/18
DRAWING NO.	3B51X - ARC - DWG - P00 - XXXX - 3500 - GBP	REV.	04
CAD REF NAME:	3B51X-ARC-BIM-0000-P00-XXXX-WS5_rvt		
AUTHORITY			

westKowloon
西九文化區

RECEIVED BY
2018 JUL 13 P 3:32
R&D Registry (R&D)
BUILDINGS DEPARTMENT

Arthur Au Kin-tung
Authorized Person (List of Architects), Registered Architect

STATEMENT II: The works shown on these plans are Type II works
()
in respect of which the Building Authority's consent is applied for.

Note: This plan has been processed on a
curtailed check basis under the centralized
processing system as promulgated in PNAP
ADM-19. The duties of the authorized person,
registered structural engineer and/or registered
geotechnical engineer concerned as specified
under section 4(3)(b) and the provision of
section 14(2)(c) of the Buildings Ordinance are
of particular relevance in this regard.