
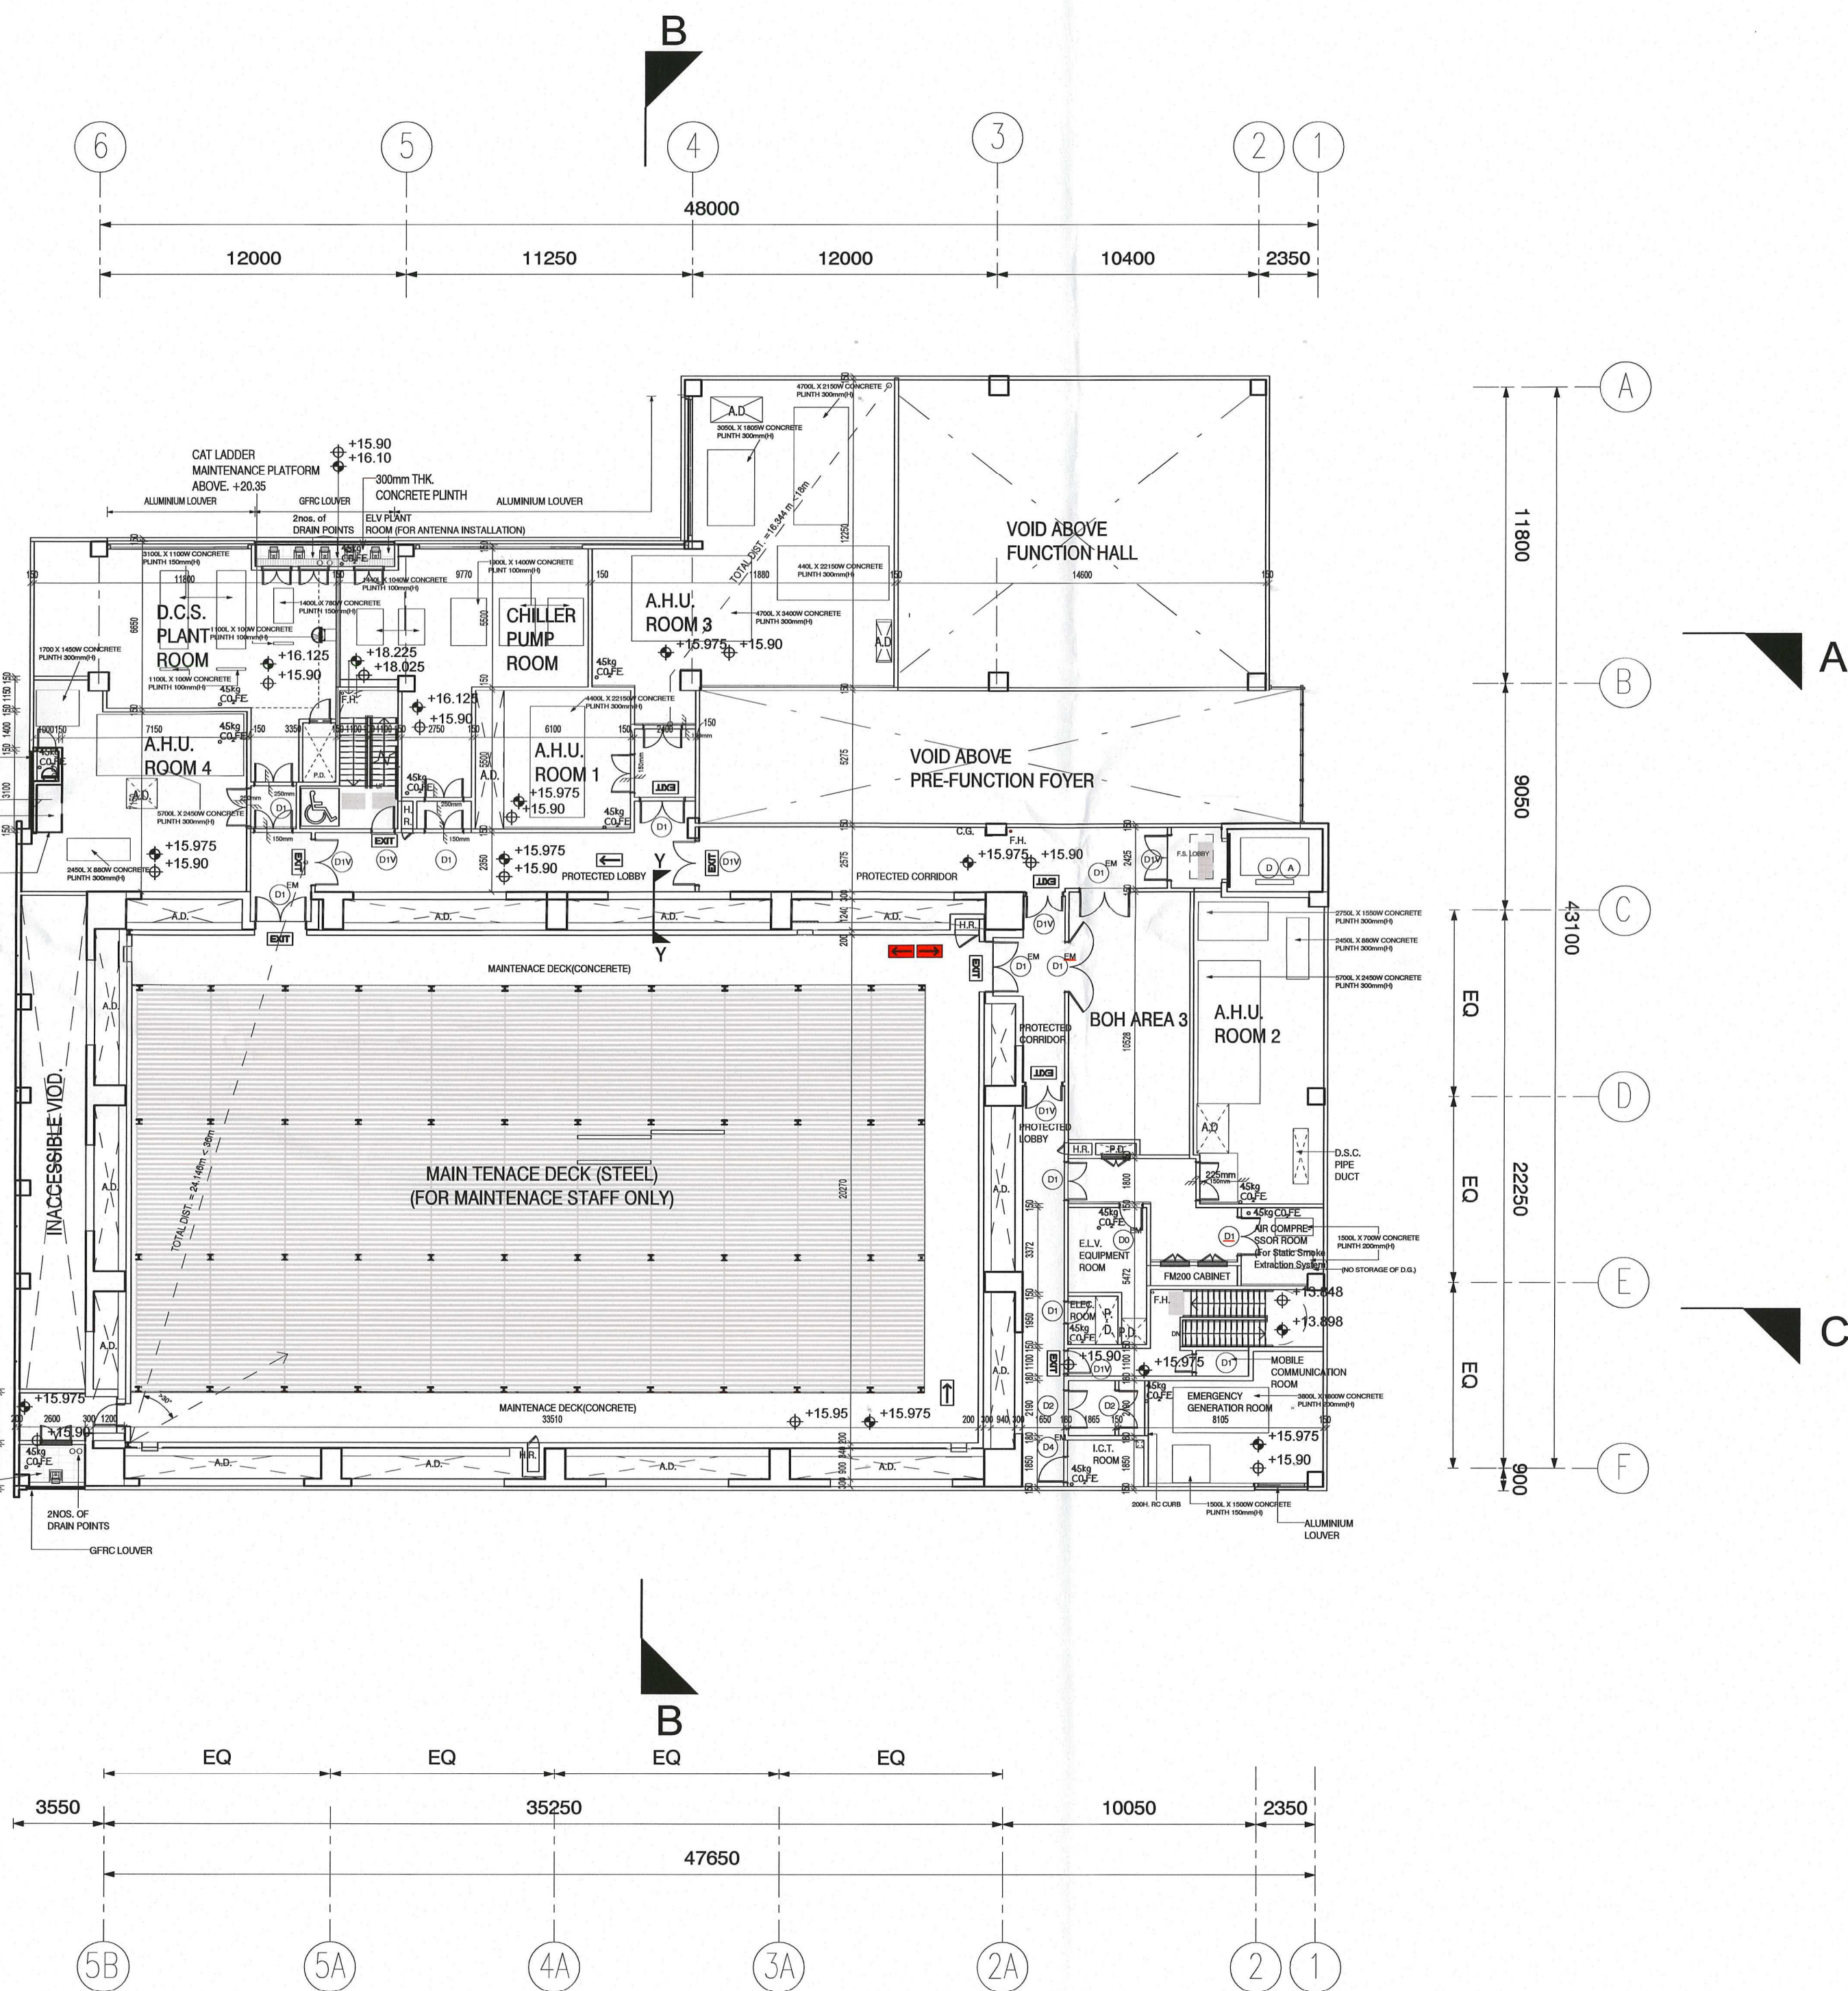


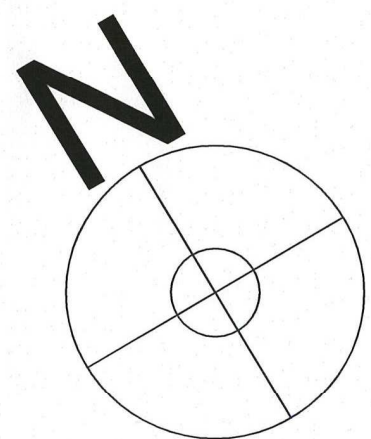


STATEMENT II: The works shown on these plans are Type II works of Building (Ancillary) in respect of which the Building Authority's consent is applied for.

B.D. REF: BD 2/4082/14(P)

F.S.D. REF: FP 8/27927(D)/1

KEY PLAN

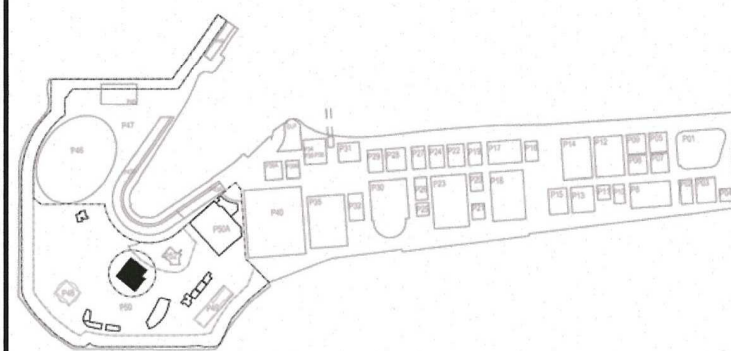

KEY PLAN

NOTES:

Note: This plan has been processed on a centralized check basis under the centralized processing system as promulgated in PNAP ADM-19. The duties of the authorized person, registered structural engineer and/or registered geotechnical engineer concerned as specified under section 4(3)(b) and the provision of section 14(2)(c) of the Buildings Ordinance are of particular relevance in this regard.

Plan Approved

LI Ming-chang Gordon
Senior Building Surveyor
for BUILDING AUTHORITY
18 MAR 2019

FOR BD APPROVAL

REV.	DATE	DESCRIPTION	INITIAL
06	13/02/19	FINAL AMENDMENT	R.NG
05	15/10/18	FINAL AMENDMENT	R.TANG
02	07/06/17	SECOND AMENDMENT	R.TANG
01	22/04/16	FIRST AMENDMENT	R.NG
00	02/12/15	FIRST SUBMISSION	R.NG

LEAD CONSULTANT & ARCHITECT	Dennis Lau & Ng Chun Man Architects & Engineers (HK) Ltd. 48/F, Tower 1, Times Square, Matheson Street Causeway Bay Hong Kong
THEATRE PLANNING CONSULTANT	Theatreplan LLP 27 Colonnade, London WC1N 1JA United Kingdom
CIVIL, GEO-TECHNICAL, STRUCTURAL, BUILDING SERVICES & ENVIRONMENTAL ENGINEER	Arcadis Design & Consultancy for Natural and Built Assets 20/F, AXA Tower Landmark East 100 How Ming Street Kowloon Tong, Kowloon Hong Kong
PROJECT LANDSCAPE ARCHITECT	ACLA Limited 20/F, AXA Tower Landmark East 100 How Ming Street Kowloon Tong, Kowloon Hong Kong
PROJECT QUANTITY SURVEYOR	Rider Levett Bucknall 利比 RLB/Rider Levett Bucknall Shaukeiwan, Hong Kong

JOB TITLE			
THE PARK DEVELOPMENT FOR THE WEST KOWLOON CULTURAL DISTRICT			
DRAWING TITLE			
FREESPACE FREESPACE - SECOND FLOOR PLAN			
SCALE 1 : 200		PRINTED A1	
CHECKED BRUCE LAW		DATE 13/02/19	
APPROVED ARTHUR AU		DATE 13/02/19	
DRAWN R.NG		DATE 13/02/19	
DRAWING NO. 3B51X-ARC-DWG-P00-L002-1003-GBP			REV. 06
CAD REF NAME: 3B51X-ARC-BIM-0000-P00-XXXX-WS5_rvt			
AUTHORITY			

westKowloon
西九文化區

RECEIVED BY
2019 FEB 18 P 11:10
R & D Registry (NEDA)
BUILDINGS DEPARTMENT