


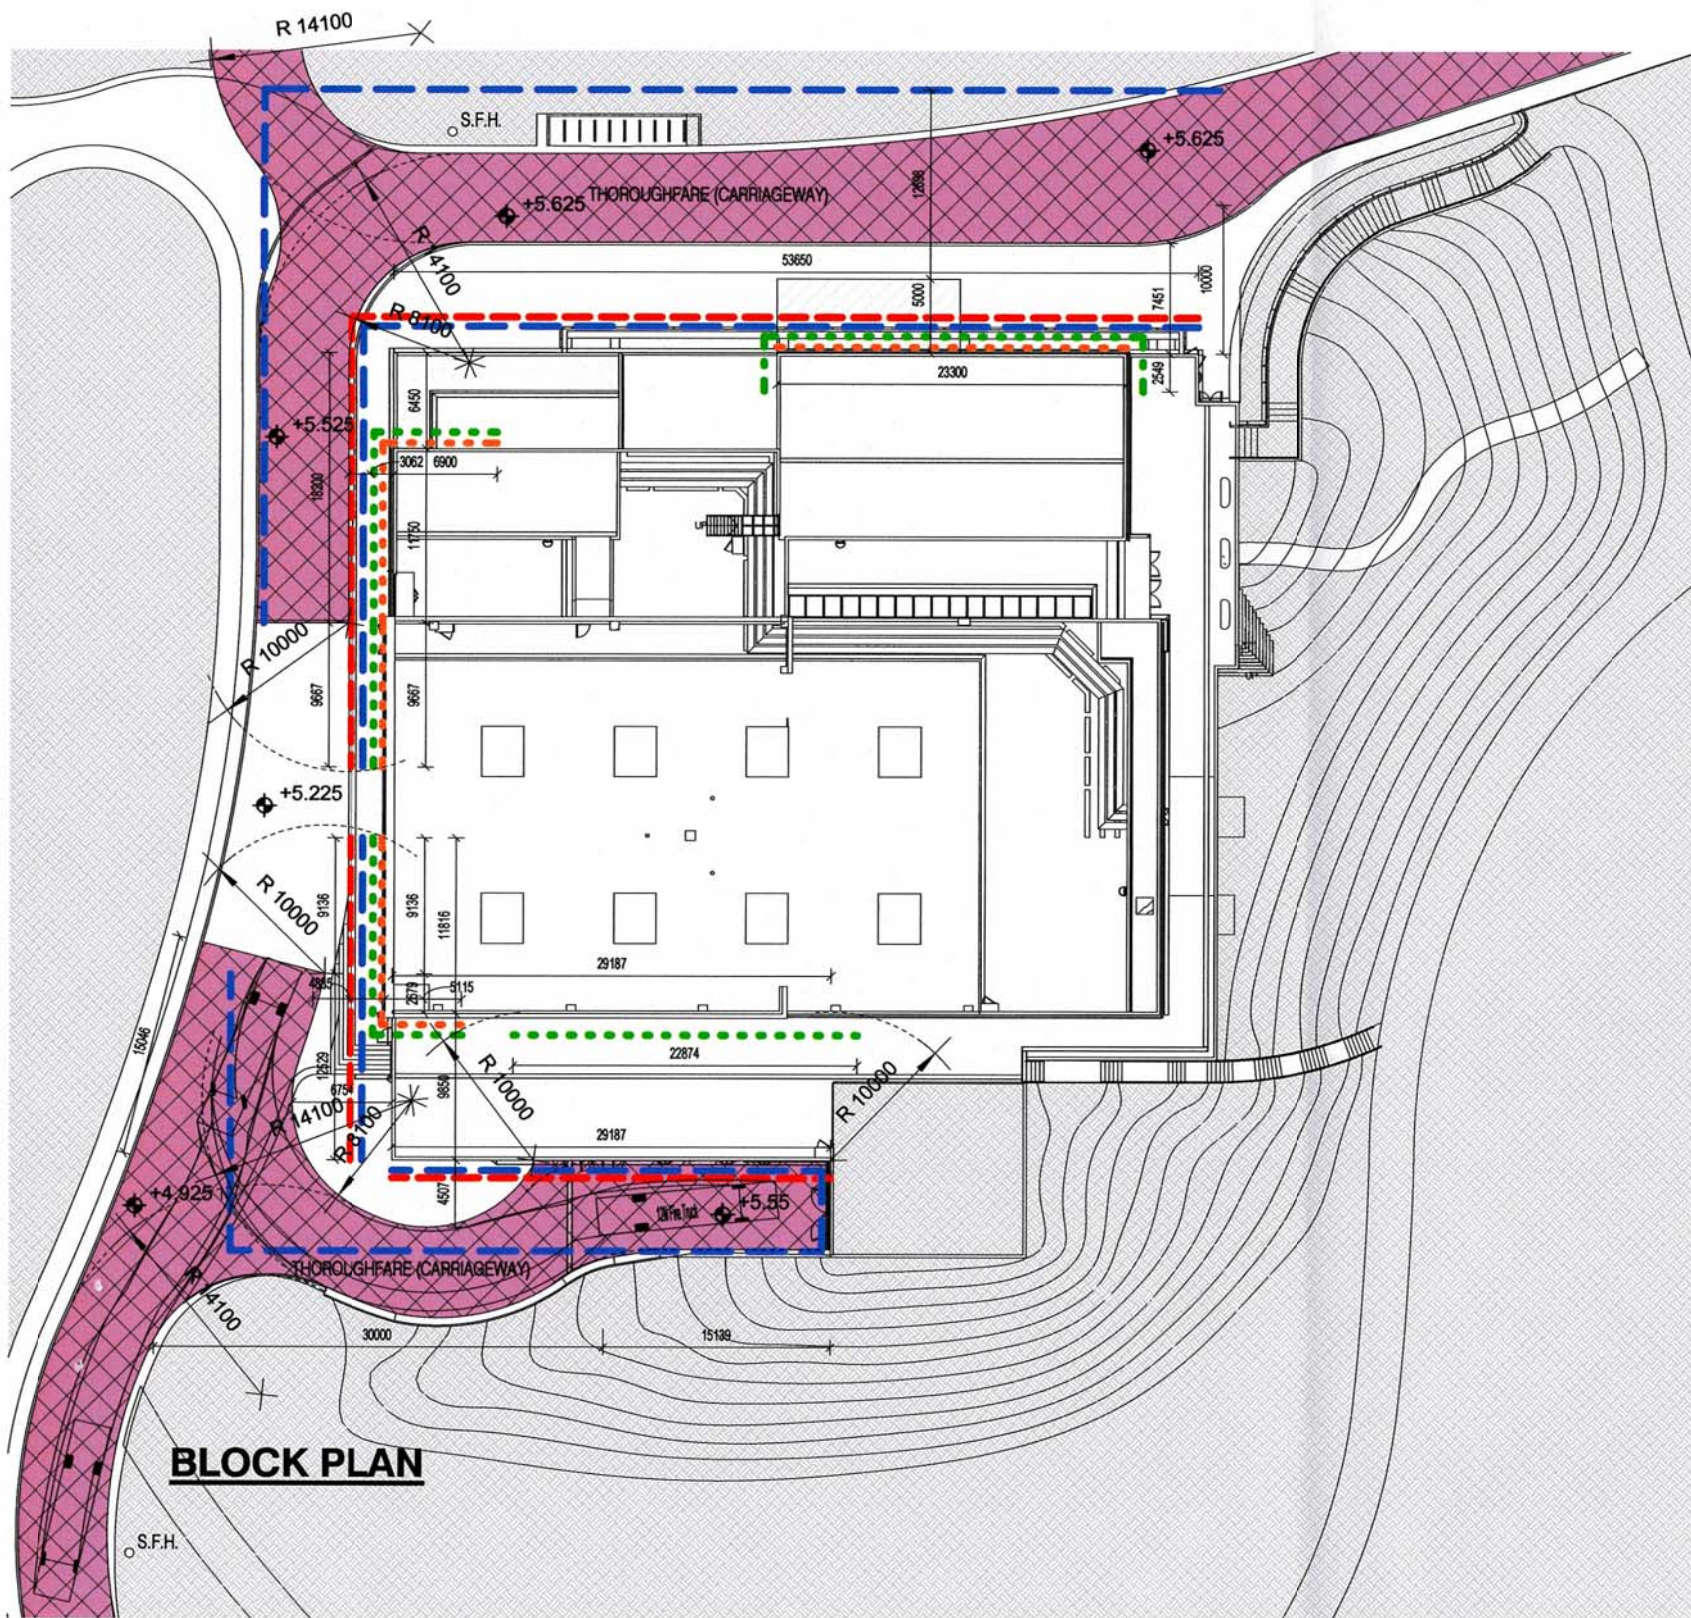

BLOCK PLAN

THOROUGHFARE CALCULATION

G/F TOTAL LENGTH OF PERIMETER WALLS OF THE BUILDING (MAX. PERIMETER)
15.15m + 6.375m + 10.35m + 6.375m + 28.15m + 2.75m + 3.25m + 18.35m + 1.4m + 25.9m + 12.75m + 13.3m + 13.062m + 6.5m + 29.187m + 54.3m
= 247.149m

TOTAL LENGTH OF MAJOR FACADES SERVED THE BUILDING FOR ABUTTING THOROUGHFARE
53.65m + 18.2m + 9.667m + 9.136m + 12.529m + 29.187m + 6m
= 138.369m

% OF MAJOR FACADE OVER THE TOTAL LENGTH OF THE BUILDING FOR ABUTTING THOROUGHFARE
= 138.369m / 247.149m X 100%
= 55.986% > 50%

E.V.A. CALCULATION

G/F TOTAL LENGTH OF PERIMETER WALLS OF THE BUILDING (MAX. PERIMETER)
15.15m + 6.375m + 10.35m + 6.375m + 28.15m + 2.75m + 3.25m + 18.35m + 1.4m + 25.9m + 12.75m + 13.3m + 13.062m + 6.5m + 29.187m + 54.3m
= 247.149m

G/F TOTAL LENGTH OF MAJOR FACADES SERVED BY E.V.A.
53.65m + 18.2m + 9.667m + 9.136m + 12.529m + 29.187m
= 132.369m

G/F % OF E.V.A. MAJOR FACADE OVER THE TOTAL LENGTH OF THE BUILDING
= 132.369m / 247.149m X 100%
= 53.558% > 50%

1/F TOTAL LENGTH OF PERIMETER WALLS OF THE BUILDING (MAX. PERIMETER)
25.5m + 6.45m + 23.3m + 12.4m + 1.325m + 5.65m + 1.025m + 26.4m + 51.65m + 26.4m + 11.6m + 0.5m
= 192.2m

1/F TOTAL LENGTH OF MAJOR FACADES SERVED BY E.V.A.
2.549 + 23.3m + 2.549 + 6.9m + 11.75m + 9.667m + 9.136m + 2.679m + 5.115m + 22.874m
= 96.519m

1/F % OF MAJOR FACADE OVER THE TOTAL LENGTH OF THE BUILDING
= 96.519m / 192.2m X 100%
= 50.218% > 50%

2/F TOTAL LENGTH OF PERIMETER WALLS OF THE BUILDING (MAX. PERIMETER)
23.3m + 6.45m + 25.5m + 38.3m + 1.3m + 51.05m + 26.625m + 24.9m + 5.275m + 22.55m + 12.55m
= 237.8m

2/F TOTAL LENGTH OF MAJOR FACADES SERVED BY E.V.A.
23.3m + 6.9m + 11.75m + 9.667m + 9.136m + 2.679m + 5.115m
= 68.547m


2/F % OF MAJOR FACADE OVER THE TOTAL LENGTH OF THE BUILDING
= 68.547m / 237.8m X 100%
= 28.825% > 25%

FOR COMPARTMENT 1a TO 1c
TOTAL AREA = 656.049m² + 719.081m² + 0m² = 1375.130m²
TOTAL VOLUME = 3,821.485m³ + 2812.738m³ + 308.586m³ = 6942.809m³


FOR COMPARTMENT 2a TO 2c
TOTAL AREA = 992.442m² + 311.799m² + 812.032m² = 2,116.273m²
TOTAL VOLUME = 5,924.880m³ + 3,628.054m³ + 3,451.136m³ = 13,004.070m³

FOR COMPARTMENT 5a TO 5b
TOTAL AREA = 177.897m² + 177.590m² = 355.487m²
TOTAL VOLUME = 791.642m³ + 754.758m³ = 1,546.4m³


STATIC SMOKE VENT CALCULATION FOR COMPARTMENT 2a, 2b & 2c
THE MIN. REQUIRED OPENING AREA:
992.442m² x 2% = 19.849m²
TOTAL FREE AREA FOR METEOR VENTILATOR :
2.829m² x 8 nos. = 22.63m² > 19.849m² (OK)
TOTAL FREE AREA FOR KAMELEON VENTILATOR:
3.421m² x 8nos. = 27.368m² > 19.849m² (OK)

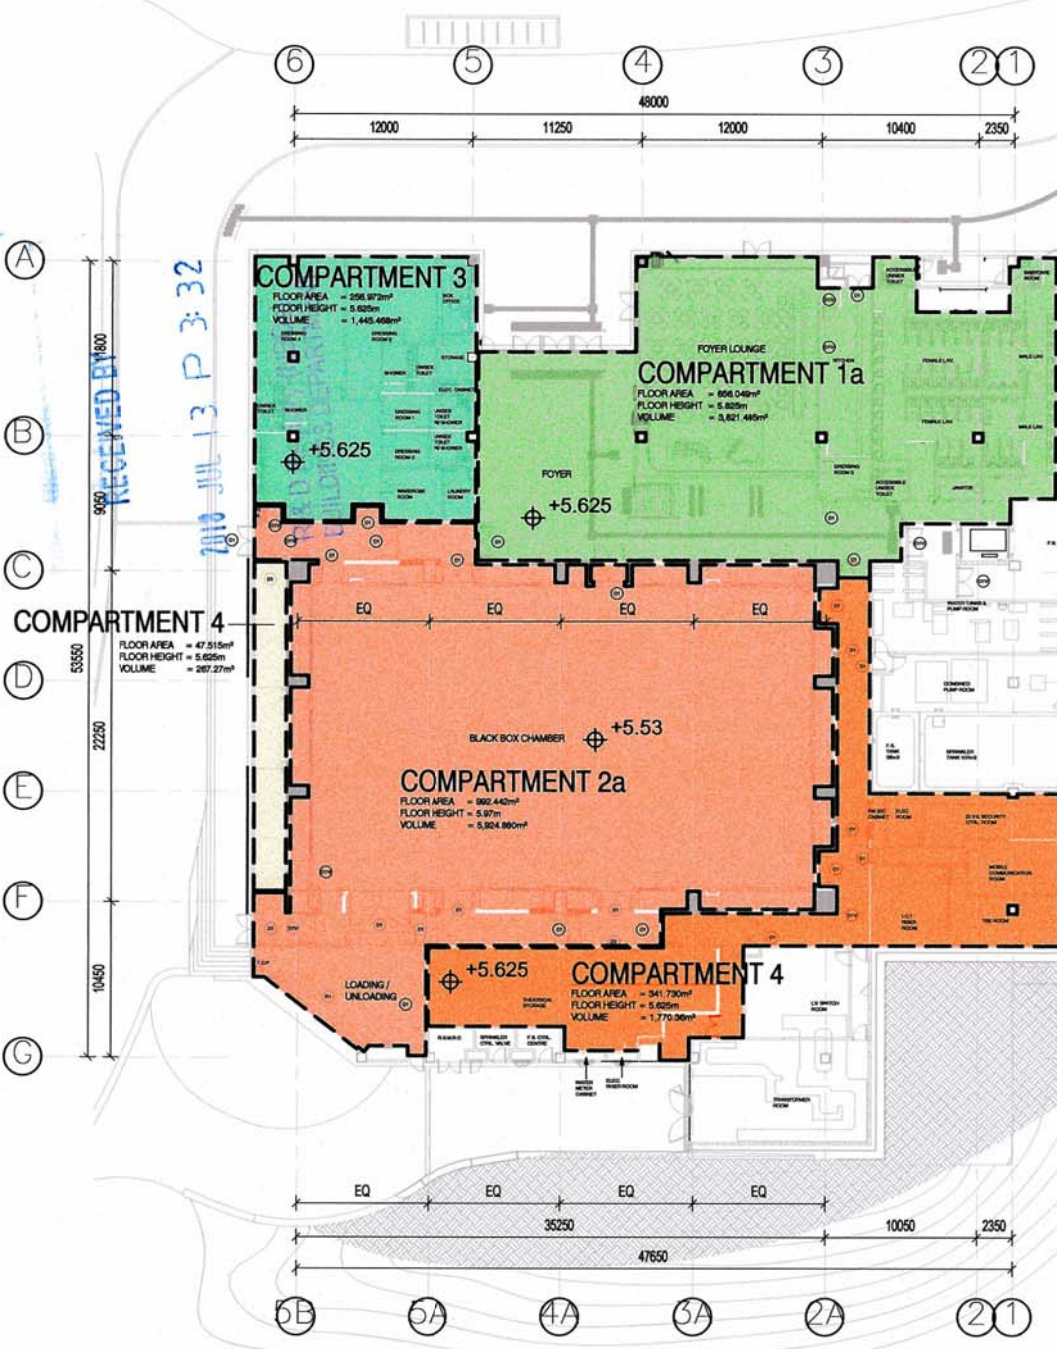



G/F COMPARTMENTATION DIAGRAM

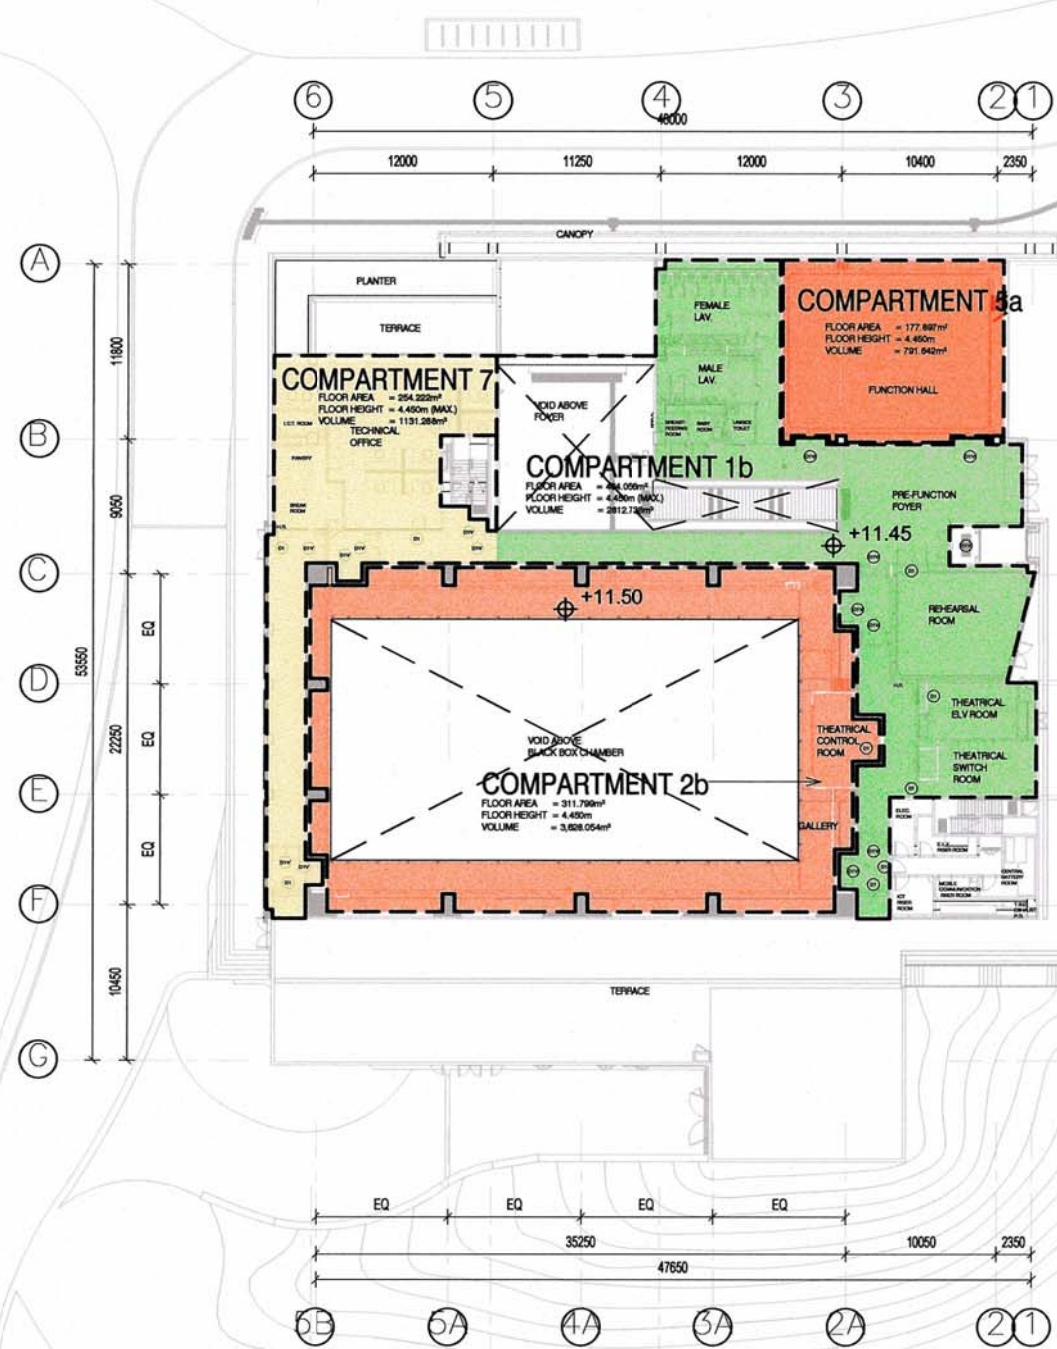

1/F COMPARTMENTATION DIAGRAM

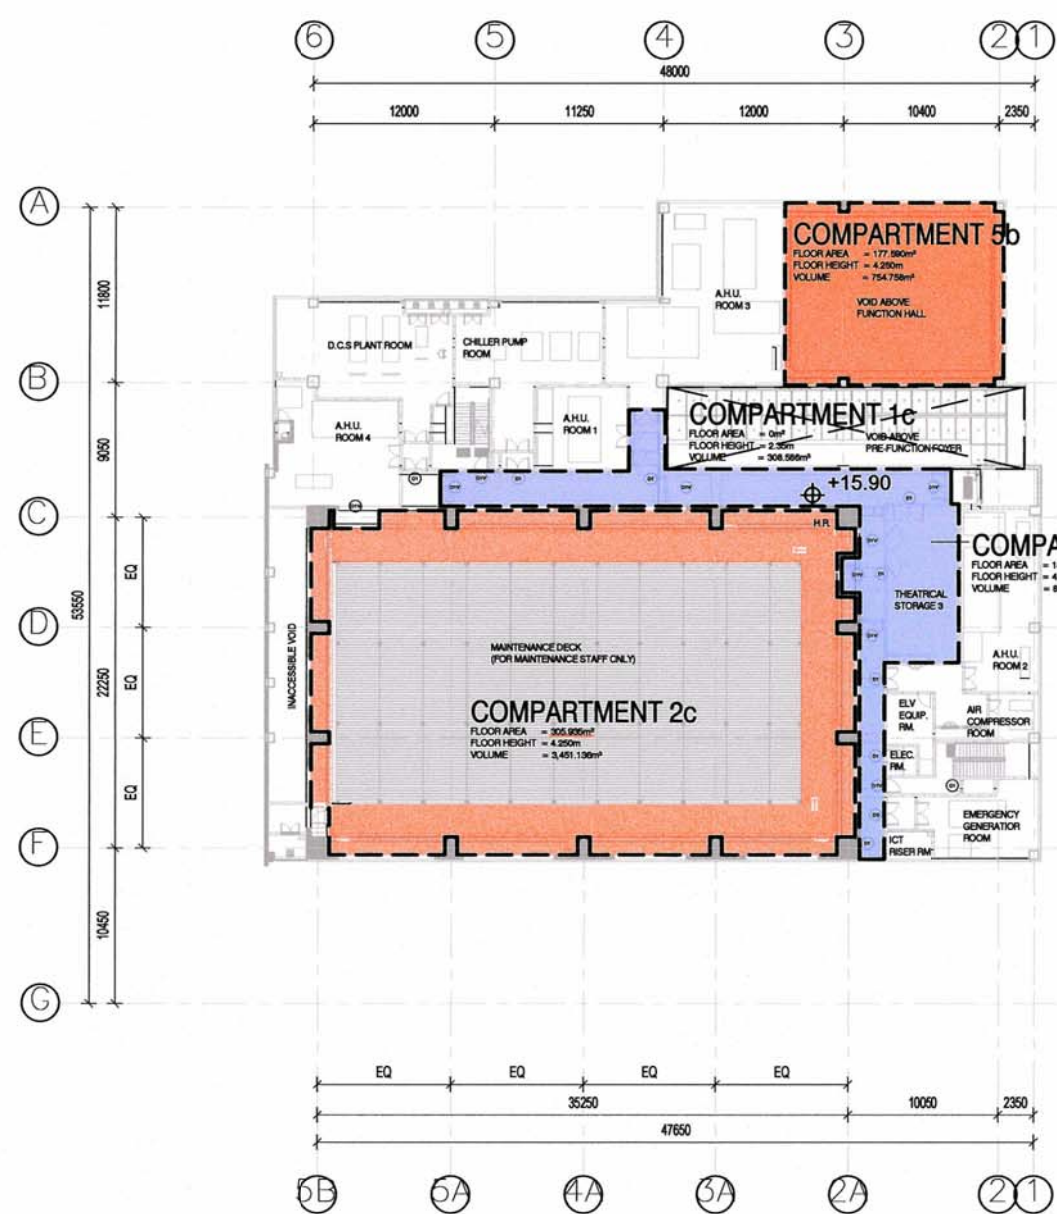

2/F COMPARTMENTATION DIAGRAM

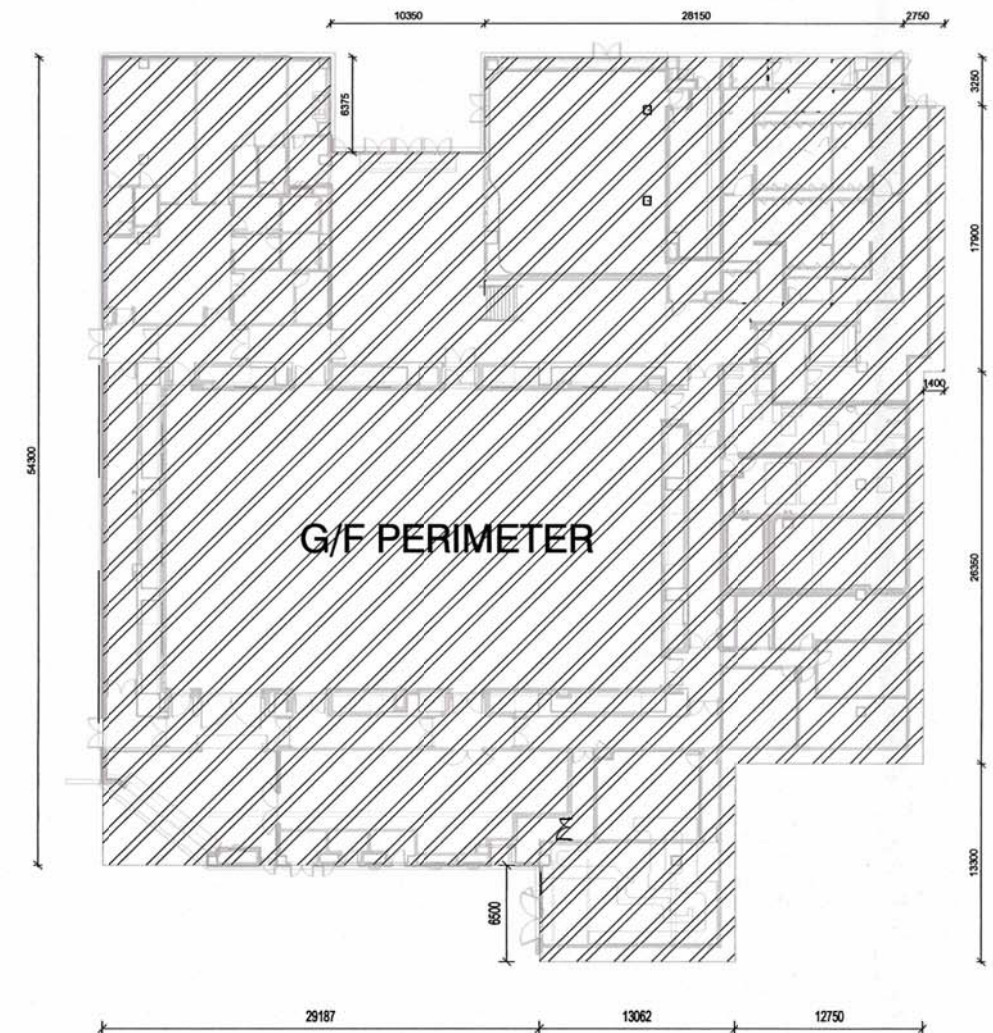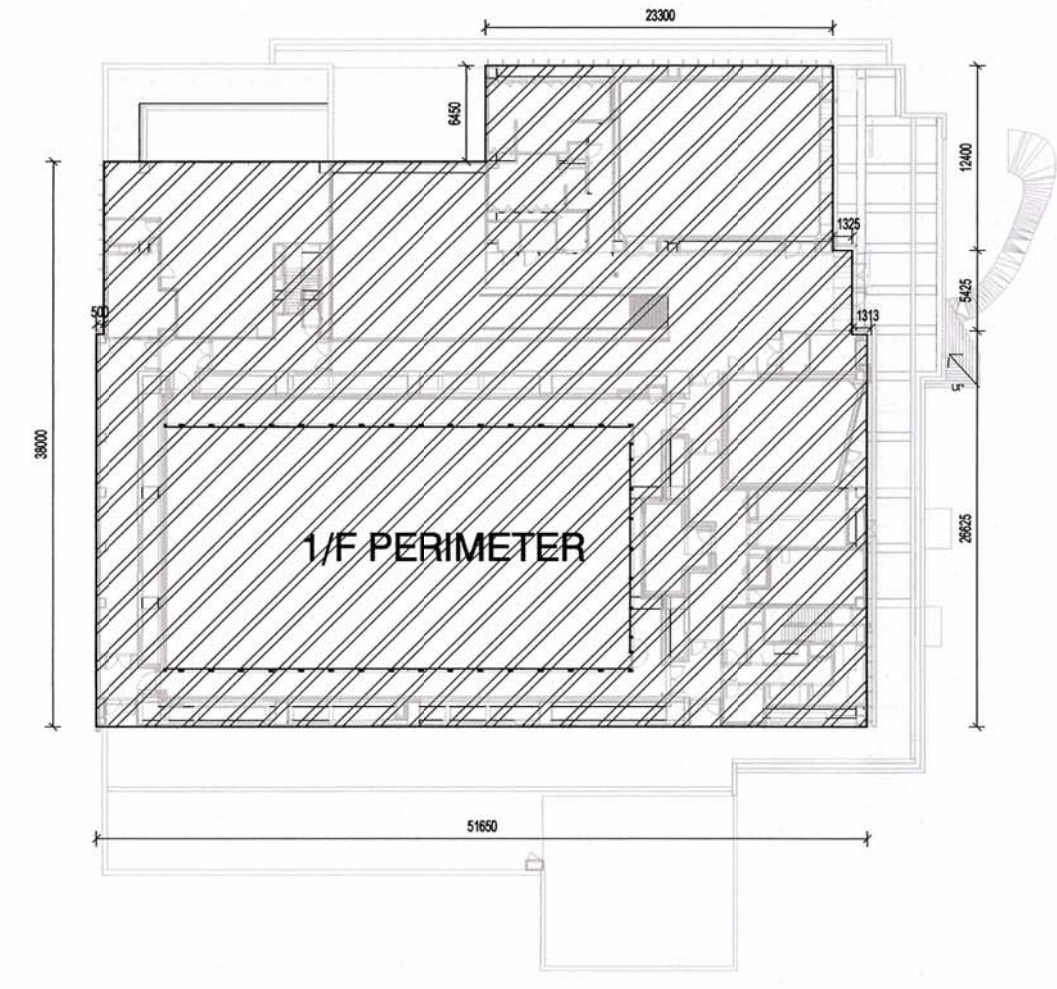

Arthur Ay Kin-tung
Aubacter Person (List of Architects), Registered Architect

STATEMENT II: The works shown on these plans are Type II works
building works
in respect of which the Building Authority's consent is applied for.

FOR OFFICE USE

Plan Approved
LI Ming-chen, Gordon
Senior Building Surveyor
for BUILDING AUTHORITY
23 AUG 2018

Note: This plan has been processed on a curtailed check basis under the centralized processing system as promulgated in PNAP ADM-19. The duties of the authorized person, registered structural engineer and/or registered geotechnical engineer concerned as specified under section 4(3)(b) and the provision of section 14(2)(c) of the Buildings Ordinance are of particular relevance in this report.

BD REF: BD 2/4062/14(P)
F.S.D. REF: FP 8/27927(D)/1
KEY PLAN

NOTES:
LEGEND FOR E.V.A. & THOROUGHFARE:

E.V.A.
-Gross weight 30,000kg

GREENERY AREA

G/F MAJOR FACADE OF THE BUILDING

1/F MAJOR FACADE OF THE BUILDING

2/F MAJOR FACADE OF THE BUILDING

MAJOR FACADE OF THE BUILDING
FOR ABUTTING THOROUGHFARE

FOR BD APPROVAL

REV.	DATE	DESCRIPTION	INITIAL
03	25/05/18	FINAL AMENDMENT	R.TANG
02	07/06/17	SECOND AMENDMENT	R.TANG
01	22/04/16	FIRST AMENDMENT	R.NG
00	02/12/15	FIRST SUBMISSION	R.NG

LEAD CONSULTANT & ARCHITECT

DLN
Dennis Lau & Ng Chun Man
Architects & Engineers (HK) Ltd.
46/F, Tower 1, Times Square,
Matheson Street,
Causeway Bay
Hong Kong

THEATRE PLANNING CONSULTANT

theatreplan
Theatreplan LLP
27 Colomade, London WC1N 1JA
United Kingdom

CIVIL, GEO-TECHNICAL, STRUCTURAL,
BUILDING SERVICES &
ENVIRONMENTAL ENGINEER

ARCADIS
Arcadis Design & Consultancy
for Natural and Built Assets
23/F, AXA Tower Landmark East
100 How Ming Street
Kowloon, Kowloon
Hong Kong

PROJECT LANDSCAPE ARCHITECT

ACLA
ACLA Limited
23/F, AXA Tower Landmark East
100 How Ming Street
Kowloon, Kowloon
Hong Kong

PROJECT QUANTITY SURVEYOR

利比 RLB Rider Levett Bucknall
Rider Levett Bucknall
20th Floor,
Eastern Central Plaza,
3 Yau Hong Road,
Shaohkwan, Hong Kong

JOB TITLE

THE PARK DEVELOPMENT FOR
THE WEST KOWLOON CULTURAL DISTRICT

DRAWING TITLE

FREESPACE
FREESPACE - DIAGRAMS AND CALCULATION 1

SCALE	1:300	PRINTED	A1
CHECKED	BRUCE LAW	DATE	09/04/18
APPROVED	ARTHUR AU	DATE	09/04/18
DRAWN	R.TANG	DATE	09/04/18

DRAWING NO.

3B51X-ARC-DWG-P00-XXXX-5000-GBP

REV.

03

CAD REF NAME: 3B51X-ARC-BIM-0000-P00-XXXX-WSS_rvt

AUTHORITY

westKowloon

西九文化區