


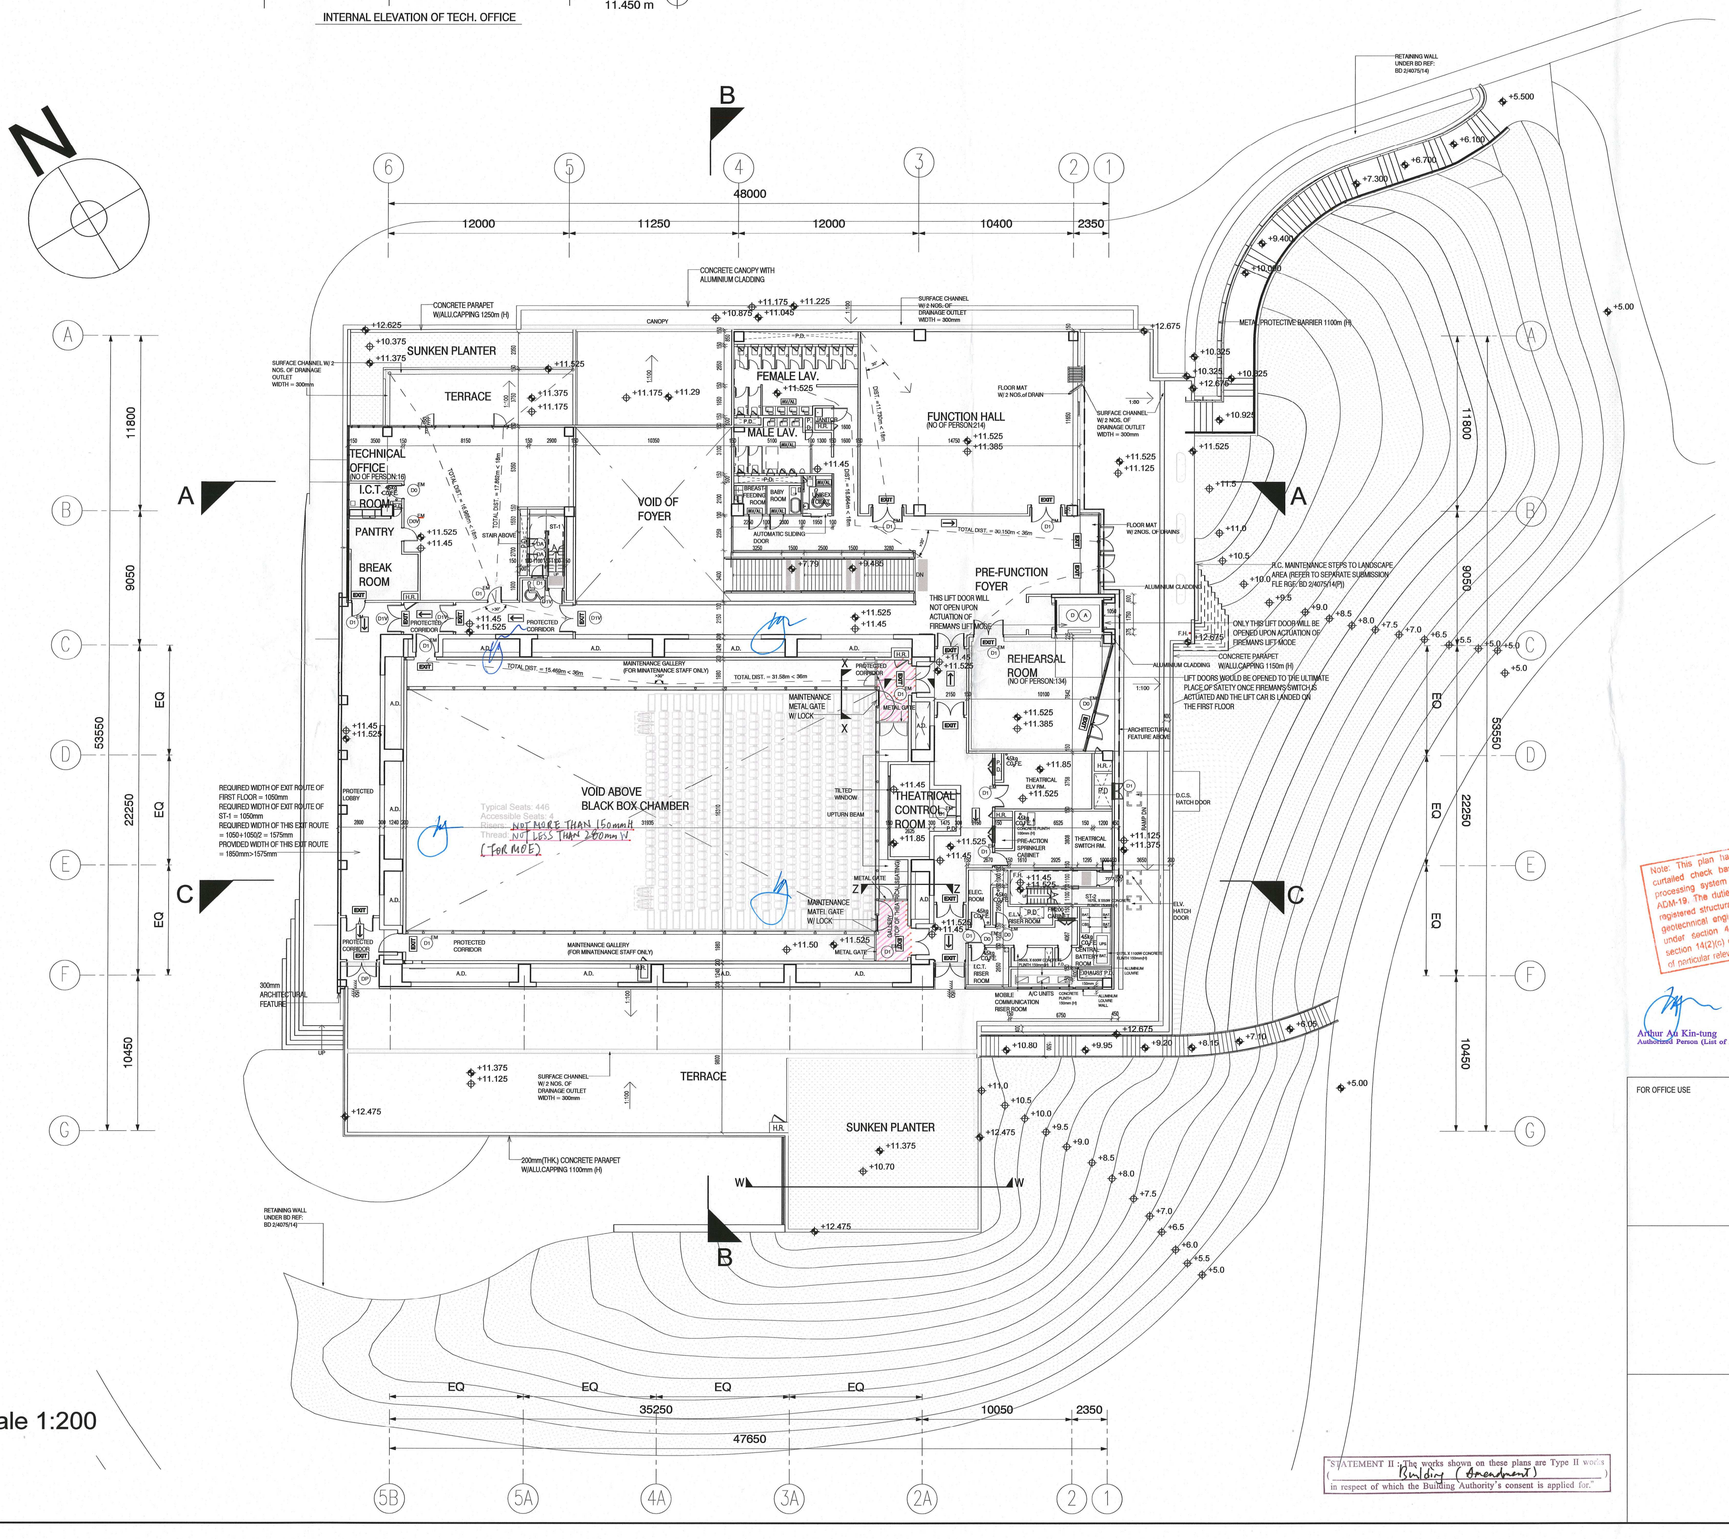


Scale 1:200

RECEIVED BY
2019 FEB 18 P 4:10
R&D Planning (GBD)
BUILDINGS DEPARTMENT

B.D. REF:	BD 2/4062/14(P)
F.S.D. REF:	FP 8/27927(D)/1

KEY PLAN

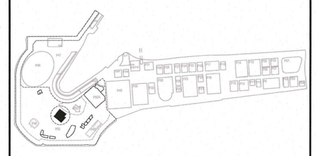

KEY PLAN

NOTES:

LANDSCAPE AREA

THE HATCHED AREA WITH PINK STRIPES IS LEVELLED WITH THE LAST STEP FOR SEATING ARRANGEMENT OPTION A (DRAWING NO.: 3B51X-ARC-DWG-P00-L000-6000-GBP REFERS) AND REG. 8 OF BUILDING (CONSTRUCTION) REGULATIONS IS NOT APPLICABLE.

Plan Approved
LI Ming-cham, Gordon
Senior Building Surveyor
for BUILDING AUTHORITY
18 MAR 2019

FOR BD APPROVAL

REV.	DATE	DESCRIPTION	INITIAL
06	13/02/19	FINAL AMENDMENT	R.NG
05	18/10/18	FINAL AMENDMENT	R.TANG
03	18/12/17	THIRD AMENDMENT	R.TANG
02	07/06/17	SECOND AMENDMENT	R.TANG
01	22/04/16	FIRST AMENDMENT	R.NG
00	02/12/15	FIRST SUBMISSION	R.NG

Note: This plan has been processed on a curtailed check basis under the centralized processing system as promulgated in PNAP ADM-19. The duties of the authorized person, registered structural engineer and/or registered geotechnical engineer concerned as specified under section 4(3)(b) and the provision of section 14(2)(c) of the Buildings Ordinance are of nonicular relevance in this regard.

Arthur Au Kin-tung
Authorised Persons (List of Architects). Registered Architect

"STATEMENT II : The works shown on these plans are Type II works (Building (Amendment)) in respect of which the Building Authority's consent is applied for."

FOR OFFICE USE

LEAD CONSULTANT & ARCHITECT	DLN	Dennis Lau & Ng Chun Man Architects & Engineers (HK) Ltd. 46/F, Tower 1, Times Square, Matheson Street Causeway Bay Hong Kong	
THEATRE PLANNING CONSULTANT	theatreplan	Theatreplan LLP 27 Colonnade, London WC1N 1JA United Kingdom	
CIVIL, GEO-TECHNICAL, STRUCTURAL, BUILDING SERVICES & ENVIRONMENTAL ENGINEER	ARCADIS	Arcadis Design & Consultancy for Natural and Built Assets 20/F, AXA Tower,Landmark East 100 How Ming Street Kwun Tong, Kowloon Hong Kong	
PROJECT LANDSCAPE ARCHITECT	ACLA	ACLA Limited 20/F, AXA Tower,Landmark East 100 How Ming Street Kwun Tong, Kowloon Hong Kong	
PROJECT QUANTITY SURVEYOR	利比 RLB \| Rider Levett Bucknall	Rider Levett Bucknall 20th Floor, Eastern Central Plaza, 3 Yiu Hing Road, Shaukeiwan, Hong Kong	

JOB TITLE
THE PARK DEVELOPMENT FOR THE WEST KOWLOON CULTURAL DISTRICT

DRAWING TITLE
FREESPACE
FREESPACE - FIRST FLOOR PLAN

SCALE	1:200	PRINTED	A1
CHECKED	BRUCE LAW	DATE	13/02/19
APPROVED	ARTHUR AU	DATE	13/02/19
DRAWN	R.NG	DATE	13/02/19

DRAWING NO. 3B51X - ARC - DWG - P00 - L001 - 1002 - GBP
REV. 06

CAD REF NAME: 3B51X-ARC-BIM-0000-P00-XXXX-WS5_.rvt

AUTHORITY

westKowloon
西九文化區