

NOTES

NOT 1)	STATUTORY REQUIREMENT ACCORDING TO APPROVED WEST KOWLOON CULTURAL DISTRICT DEVELOPMENT PLAN NO. SKW/DMO/2004 AND REVISED SECTION 16 APPLICATION NO. AKO/2012.	AGF	ARTS & CULTURAL FACILITIES
	1. ITEM 6: ITEM 1+2+3+4+5	ACF	TRIST SQUARE TOWER
	2. ITEM 15: INCLUDED IN ITEM 15	MPRP	BUILDING PLANNING REGULATIONS
	3. ITEM 15: ITEM 6+9+10+11+12+13+14	CCF	CORE ARTS & CULTURAL FACILITIES (FORM PART OF ARTS & CULTURAL FACILITIES)
	4. ITEM 16: INCLUDED IN ITEM 15	CSF	CONSERVATION & STORAGE FACILITY
	5. ITEM 17: INCLUDED IN ITEM 16	DP	DEVELOPMENT PLAN OF WACO
		DR	NATIONAL DRAINAGE REGULATE

(NOTE 2) PACKAGE AREA IS THE AREA OF DEVELOPMENT WITHIN WEST KOWLOON CULTURAL DISTRICT EXCLUDING ROAD AREAS. VOID AREA OF LINK DECK (REFER TO GROUND FLOOR CONTROL PLAN DRAWING NO. 003-1-00000) EXCLUDED PACKAGE AREA SHALL BE USED AS SUBTOTAL TO BE USED FOR REGIONAL AND DISTRICT

(NOTE 5)	TO CORRELATE THE PROVISION OF GREENERY AREAS FOR THE PURPOSE OF PNAP APP-152 WITH THE CONSTRUCTION PROGRESS OF THE TOPSIDE DEVELOPMENTS REQUIRED COVERAGE OF GREENERY IS CALCULATED IN A PRO-RATA BASIS IN PROPORTION TO THE DEVELOPED SITE AREA OF EACH PACKAGE	HOR HOTEL OFFICE & RESIDENTIAL OACF OTHER ARTS & CULTURAL FACILITIES (FORM PART OF ARTS & CULTURAL FACILITIES) PA PERFORMANCE ART VENUE PMO PARK MANAGEMENT OFFICE & ANCILLARY BUILDINGS ROE RETAIL, DINING & ENTERTAINMENT
----------	--	---

(NOTE 4) BASED ON ONE SITE CONCEPT REQUIRED COVERAGE GREENERY IS DISTRIBUTED IN DIFFERENT AREAS NOT NECESSARILY WITHIN THE PACKAGE AREA BUT WOULD BE ACCESSIBLE TO OCCUPANT OF THE

(NOTE 5) GFA FOR "ARTS & CULTURAL FACILITIES (ACF)" WOULD INCLUDE FACILITIES, AMONG OTHERS, A HOST HOTEL FOR VISITING ARTISTS, REHEARSAL FACILITIES/OFFICES FOR ARTS GROUPS AND CREATIVE SPACES.

(NOTE 6) PURSUANT TO CONDITIONS OF GRANT NO 20369 OF KIL 11260 DATED 2 APRIL 2020, THE SITE AREA OF WEST KOWLOON CULTURAL DISTRICT IS 395,488m². WKC VENTILATION BUILDING, AIRPORT RAILWAY VENTILATION & TRACTION SUBSTATION BUILDING, AND CLP ELECTRICITY SUBSTATION ARE OUTSIDE KIL 11260.

MAX TOTAL GFA FOR RESIDENTIAL	170,280 m ²
MIN PROVISION OF OPEN SPACE	21.98 ha

OVERALL DEVELOPMENT PLANNING PARAMETERS
(UNDER DEVELOPMENT PLAN (DP))

CLASS OF SITE:	"A"
LOCATION & LOT NO.:	WEST KOWLOON CULTURAL DISTRICT, HONG KONG
SITE AREA (NOTE 1):	40.91 ha. (ABOUT)
MAX. TOTAL GROSS FLOOR AREA (NOTE 1):	851400 m ² (ABOUT)

HEIGHT OF BUILDING:	BUILDING HEIGHT RESTRICTIONS RANGING FROM 50m ABOVE PRINCIPLE DATUM (m P.D.) TO 100m P.D. (3-STORY AT THE PARK)		
MEAN STREET LEVEL AT AUSTIN ROAD WEST	HIGHEST MEAN STREET LEVEL	+	LOWEST MEAN STREET LEVEL
		2	
	8.841 m P.D.	+	4.770 m P.D.
		2	
	+ 6.71 m P.D.		
MEAN STREET LEVEL AT CANTON ROAD WEST	HIGHEST MEAN STREET LEVEL	+	LOWEST MEAN STREET LEVEL
		2	
	4.400 m P.D.	+	3.900 m P.D.
		2	
	+ 4.15 m P.D.		
AVERAGE MEAN STREET LEVEL:			5.43 m P.D.
MAXIMUM ALLOWED BUILDING HEIGHT:			100.00 m P.D.

ITEM	LAND-USE ZONING ON DEVELOPMENT PLAN NO. SK20/WKCD2	LAND-USE ZONING ON DEVELOPMENT PLAN (NOTE 1) NO. SK20/WKCD2 (MAXIMUM GFA, m²)
1	OU (ACEQU) 1	77,045
2	OU (ACEQU) 2	191,602
3	OU (ACEQU) 3	61,204
4	OU (ACEQU) 4	18,608
5	OU (ACEQU) 5	28,360
6	OU (ACEQU) 1 to 5 - TOTAL	376,839 (NOTE 1)
7	OU (ACEQU) 1 to 5 - HOTEL / OFFICE	43,023 (NOTE 1)
8	OU (MU) 1	87,960
9	OU (MU) 2	65,411 (RESIDENTIAL NOT MORE THAN 12,695)
10	OU (MU) 3	118,027 (RESIDENTIAL NOT MORE THAN 66,350)
11	OU (MU) 4	105,796 (RESIDENTIAL NOT MORE THAN 52,863)
12	OU (MU) 5	49,535 (RESIDENTIAL NOT MORE THAN 25,309)
13	OU (MU) 6	26,445 (RESIDENTIAL NOT MORE THAN 8,704)
14	OU (MU) 7	4,789 (RESIDENTIAL NOT MORE THAN 3,759)
15	OU (MU) 1 to 7 - TOTAL	457,975 (NOTE1)
16	OU (MU) 1 to 7 - HOR	323,597 (NOTE1)
17	OU (MU) 1 to 7 - RESIDENTIAL	170,289 (NOTE1)
18	LAND DESIGNATED "OPEN SPACE (2)" OR "O2"	300
19	LAND DESIGNATED "OPEN SPACE (1)" OR "O1"	12,788
20	O (VESS)	3400 (NOTE 6)

GREEN COVERAGE PROVISION (NOTE 1)	
TOTAL GREEN COVERAGE % OF THE SITE:	NOT LESS THAN 30%
TOTAL GREEN COVERAGE % IN THE PARK OF TOTAL GREEN COVERAGE OF THE SITE:	NOT LESS THAN 60%

PROVISION OF PUBLIC OPEN SPACE	
(NOTE 1) PUBLIC OPEN SPACES (TOTAL):	23 ha. (NOT LESS THAN)
(NOTE 1) TOTAL PUBLIC OPEN SPACES ON "OUJAEUJUI" TO "OUJAEUJUS":	57700 m ² (NOT LESS THAN)
(NOTE 1) PIAZZA AREAS (AS PART OF PUBLIC OPEN SPACES):	3 ha. (NOT LESS THAN)
(NOTE 1) TERRACE GARDEN (AS PART OF PUBLIC OPEN SPACES):	5 ha. (NOT MORE THAN)

OVERALL DEVELOPMENT DESIGN PARAMETERS
(UNDER BUILDING (PLANNING) REGULATIONS (B(P)R))

1. MAXIMUM BUILDING HEIGHT (FOR CONSIDERATION OF SCHEDULE 1 OF B(P) = 100.00 m.P.D. - 5.43 m.P.D. = 94.57 m.P.D. OR OVER 61m.P.D.

2. SITE COVERAGE (SC) CALCULATION

ACTUAL DOMESTIC SITE COVERAGE AREA		=	$\frac{17,089}{36,489}$ x 100%	SITE AREA
		=	46.84% (DOMESTIC)	
PERMITTED DOMESTIC SITE COVERAGE	: SCD _d	=	60.00% (NON-DOMESTIC)	"A"
PERMITTED NON-DOMESTIC SITE COVERAGE	: SCD _n	=	33.33% (DOMESTIC)	
ACTUAL PERMITTED NON-DOMESTIC SITE COVERAGE	: SCD _a	=	(SCD _i - SCD _d) x $\frac{SCD_n}{SCD_d}$	
		=	(33.33% - 46.84%) x $\frac{60.00\%}{46.84\%}$	
		=	-13.51% (NON-DOMESTIC) < 33.33% (PERMITTED)	
ACTUAL PERMITTED NON-DOMESTIC SITE COVERAGE (L) UNDER MASTER REGISTER		=	$\frac{54,373}{210,132}$ x 100%	ACTUAL NON-DOMESTIC SITE AREA
		=	25.87% (NON-DOMESTIC)	
PERMITTED NON-DOMESTIC SITE COVERAGE (L) UNDER MASTER REGISTER		=	$\frac{136,570}{36,489}$ x 100%	SITE AREA
		=	374.33% (NON-DOMESTIC)	
ACTUAL PERMITTED NON-DOMESTIC SITE COVERAGE (L) UNDER MASTER REGISTER		=	$\frac{54,373}{136,570}$ x 100%	ACTUAL PERMITTED
		=	39.83% (NON-DOMESTIC)	

3. PLOT RATIO (PR) AND GROSS FLOOR AREA (GFA) CALCULATION

ACTUAL PERMITTED PLOT RATIO	=	Prad	=	15	(NON-DOMESTIC)	
		Prd	=	8	(DOMESTIC)	
ACTUAL GROSS FLOOR AREA (DOMESTIC)	=			<u>188,939</u>	m ²	(DOMESTIC) (REFER NOTE-1)
ACTUAL DOMESTIC PLOT RATIO (Prad)	=	Prad	=	ACTUAL DOMESTIC GFA		
			=	SITE AREA		x 100%
	=			<u>188,939</u>	m ²	
	=			<u>389,498</u>	m ²	
	=			<u>0.437</u>	(NON-DOMESTIC) < 8	(ACTUAL PERMITTED)
ACTUAL PERMITTED NON-DOMESTIC PLOT RATIO	=	(Prd - Prad) x Prnd				
	=	(8 - <u>0.437</u>) x $\frac{Prnd}{15}$				
	=	<u>14.180</u>		(NON-DOMESTIC) < 15	(PERMITTED)	
ACTUAL PERMITTED GROSS FLOOR AREA (NON-DOMESTIC)	=	<u>389,498</u> m ² x $\frac{14.180}{15}$				
	=	<u>5,440,559.375</u>		m ²	(NON-DOMESTIC)	
ACTUAL PERMITTED GROSS FLOOR AREA (TOTAL)	=	<u>188,939</u> m ² + <u>5,440,559.375</u>				
	=	<u>5,640,498.375</u>		m ²		

4. ESTIMATED GROSS FLOOR AREA OF EXISTING OR WORK IN PROGRESS BUILDINGS WITHIN THE SITE

EXISTING FIRE STATION *	= 5,738,000 m ² (NON-DOMESTIC)
	= 13,562,000 m ² (DOMESTIC)
EXISTING WATER SUPPLIES DEPARTMENT SALT WATER PUMPING (WSD) STATION **	= 1,240,000 m ² (NON-DOMESTIC)
WEST KOWLOON TERMINUS (WKT)***	= 4,632,100 m ² (NON-DOMESTIC)

Notes:

- * EXISTING FIRE STATION IS LOCATED MAINLY ON PACKAGE 02, WHERE MAX. GFA ALLOWED IS HIGHER THAN EXISTING FIRE STATION'S, HENCE, THE EXISTING GFA IS ALREADY INCLUDED WITHIN PACKAGE 02, TOTAL GFA FOR PACKAGE 00, 02 AND 24B WILL BE AMENDED BY THE CORRESPONDING GFA OF EXISTING TSM SHAT SUI FIRE STATION IF RE-LOCATION OF THE FIRE STATION CANNOT BE MATERIALISED EVENTUALLY.
- * EXISTING WSD STATION IS LOCATED MAINLY ON PACKAGE 21, WHERE MAX. GFA ALLOWED IS HIGHER THAN EXISTING WSD STATION'S, HENCE, THE EXISTING GFA IS ALREADY INCLUDED WITHIN PACKAGE 21.

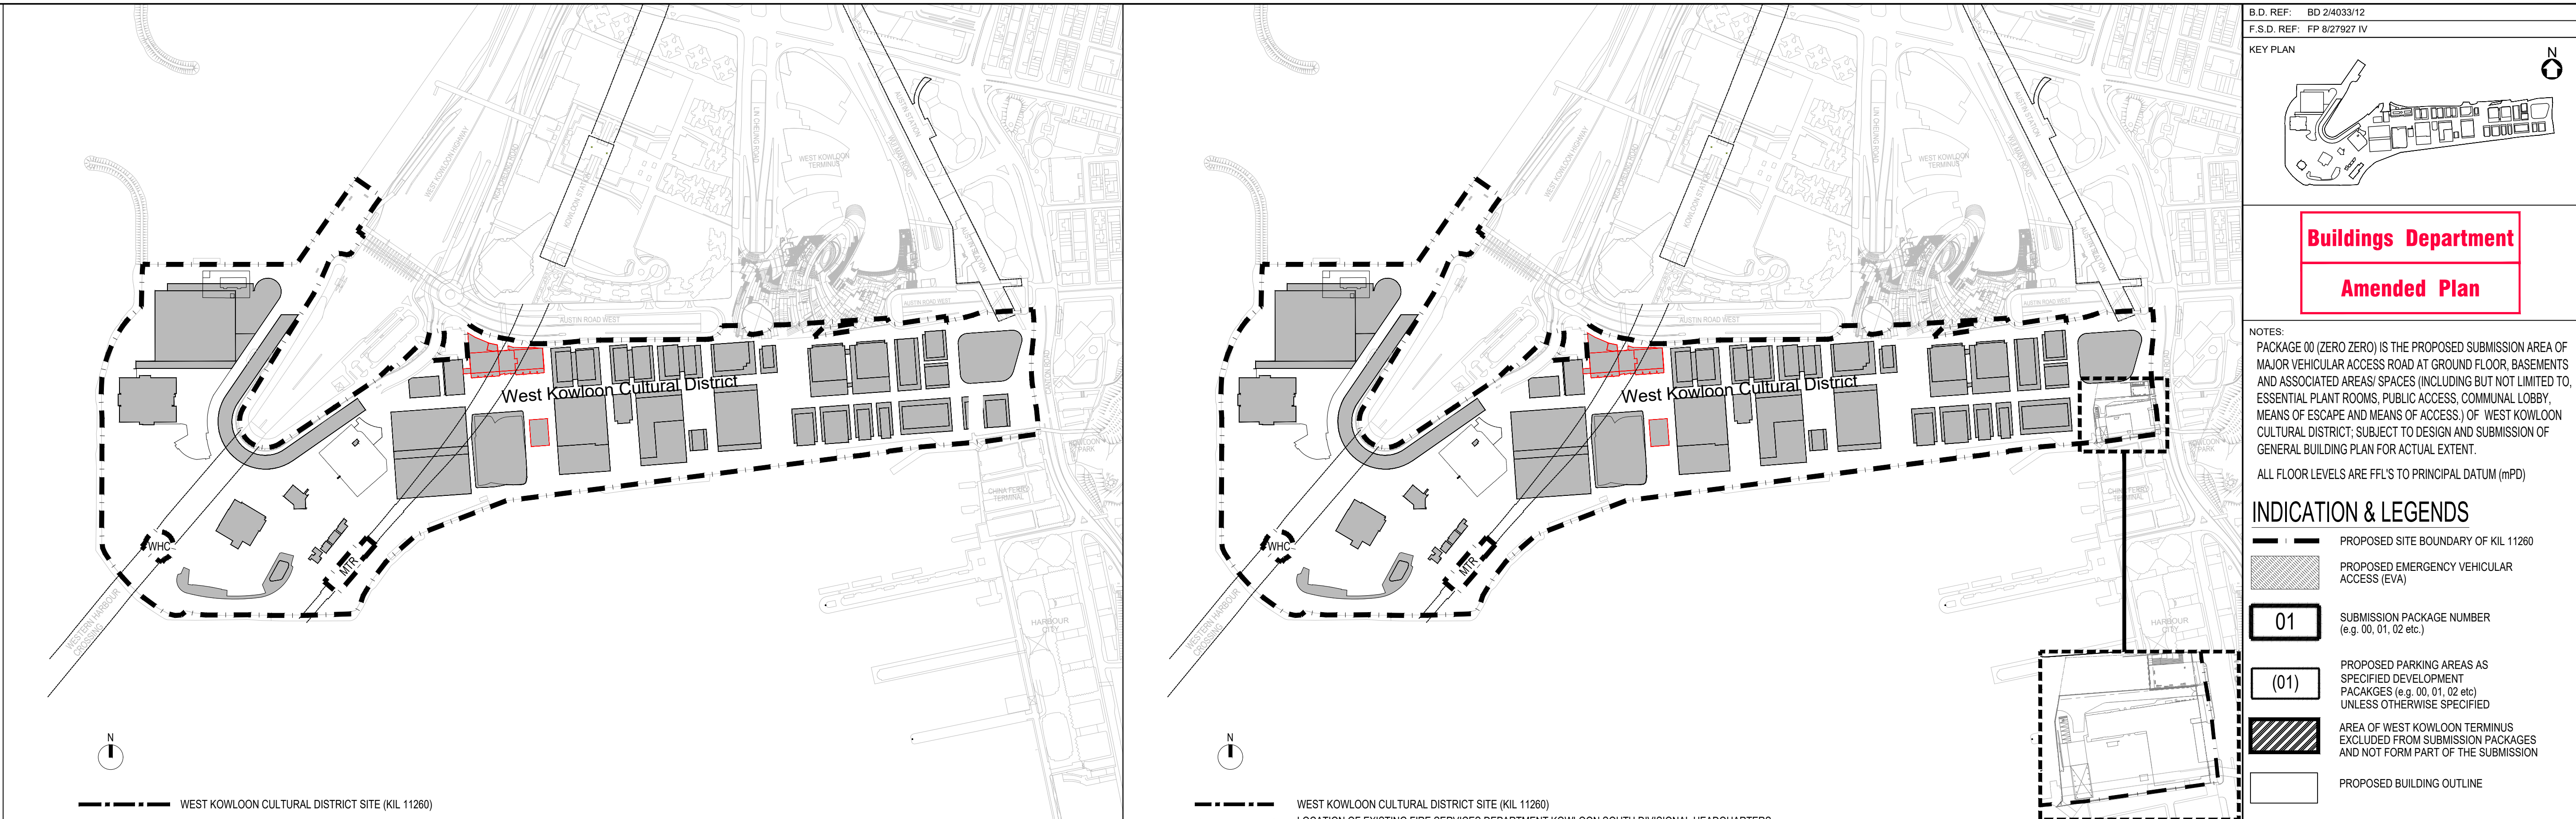
GROSS FLOOR AREA CALCULATION			
TOTAL GROSS FLOOR AREA	=	EXISTING GFA (REFER NOTE "E" NOTE"*)	+ 821,262.000 m ²
	=	4,632.100 +	821,262.000
	=	825,894.100 m ²	< 5,649,498.375 m ² (ACTUAL MAX. TOTAL GFA)

ABBREVIATION

ACF	ARTS & CULTURAL FACILITIES
ART	ARTIST SQUARE TOWER
BUPR	BUILDING (PLANNING) REGULATIONS
CACF	CORE ARTS & CULTURAL FACILITIES (FORM PART OF ARTS & CULTURAL FACILITIES)
CSC	CONSERVATION & ST. GEORGE FACILITY
CP	DEVELOPMENT PLAN OF IWCH
DB	NATIONAL DANCE RESERVE
FR	NOTIONAL FOOTPATH
GFA	GROSS FLOOR AREA
GOVERNMENT	GOVERNMENT INSTITUTION & COMMUNITY
HPHM	HONG KONG PLAZA MUSEUM
HO	HOTEL OFFICE RESIDENTIAL
IA	OTHER ARTS & CULTURAL FACILITIES (FORM PART OF ARTS & CULTURAL FACILITIES)
JOE	PERFORMANCE ART VENUE
PMD	PARK MANAGEMENT OFFICE & ANCIALLY BUILDINGS
ROE	RETAIL DINING & ENTERTAINMENT
TSC	TO BE CONFIRMED
SN	NOTIONAL SUBWAY
WHC	WESTERN HARBOR CROSSING
	NOTIONAL WATER RESERVE

OVERALL DEVELOPMENT PLANNING PARAMETERS
(UNDER CONDITIONS OF GRANT NO. 20359 OF KIL 11260)

LOT NO.	KL 11290
SITE AREA (NOTES)	356,488 m ²
MAX TOTAL GFA PERMITTED	848,000 m ²
MAX TOTAL GFA FOR HOR	368,620 m ²
MAX TOTAL GFA FOR RESIDENTIAL	170,280 m ²
MIN PROVISION OF OPEN SPACE	21.96 ha

WEST KOWLOON CULTURAL DISTRICT LOCATION PLAN
(UNDER PROSECUTION OF DEFERRED PROSECUTION AREA)

Scale 1 : 5000

WEST KOWLOON CULTURAL DISTRICT LOCATION PLAN Scale 1 : 5000

(EXISTING FIRE SERVICES DEPARTMENT KOWLOON SOUTH DIVISIONAL HEADQUARTERS & TSIM SHA TSUI FIRE STATION LOCATION) Scale 1 : 2000

[illegible]