



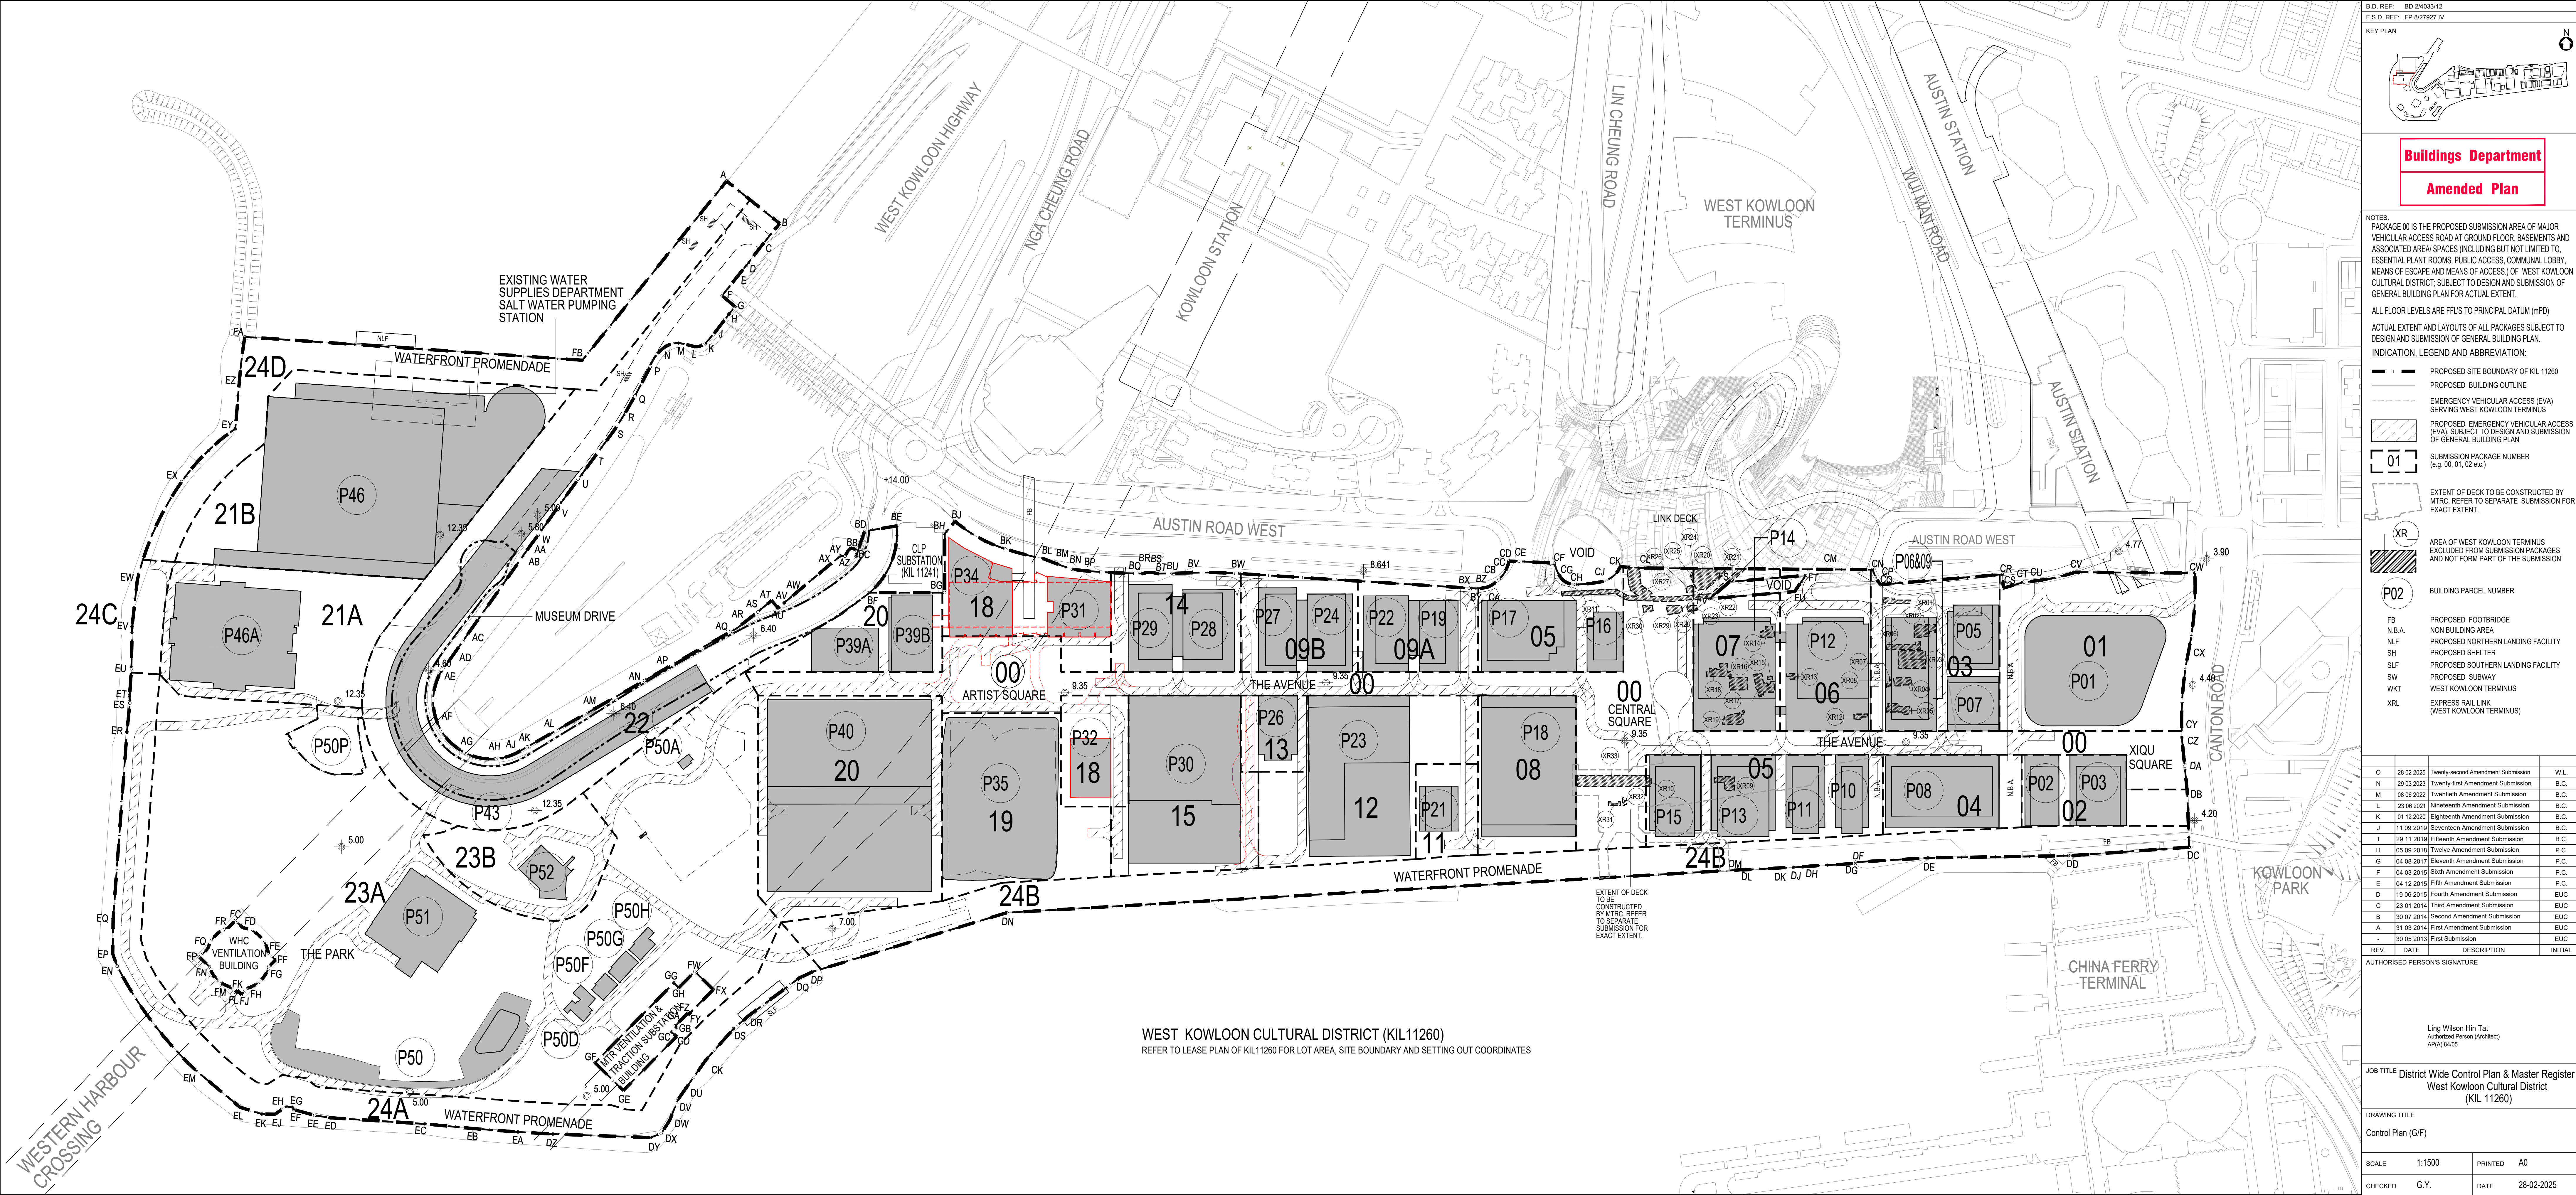

XRL ESTIMATED GROSS FLOOR AREA CALCULATION AT WKCD SITE
(EXACT XRL GFA AND LAYOUTS REFER TO SEPARATE SUBMISSION
FOR WEST KOWLOON TERMINUS)

1. GROUND FLOOR:	
ESTIMATION OF XRL FLOOR AREAS AT WKCD SITE "OU (MU) ZONE"	ESTIMATION OF XRL FLOOR AREAS AT WKCD SITE "OU (ACECU) ZONE"
PORTION	G.F.A. (m ²)
XR01	52.3
XR02	103.9
XR03	221.1
XR04	62.3
XR05	85.8
XR06	81.7
XR07	2.5
XR08	5.9
XR09	88.1
XR10	24.3
XR11	127.5
SUB-TOTAL [1]	854.5
PORTION	G.F.A. (m ²)
XR12	27.5
XR13	24.2
XR14	52.1
XR15	8.1
XR16	101.6
XR17	118.3
XR18	94.9
XR19	89.7
XR20	218.9
XR21	103.7
XR22	0.4
XR23	8.8
SUB-TOTAL [2]	849.2
PORTION	G.F.A. (m ²)
XR24	0.1
XR25	8.2
XR26	18.7
XR27	32.6
XR28	15.7
XR29	55.1
XR30	25.9
XR31	14.7
XR32	10.7
XR33	348.4
SUB-TOTAL [3]	622.1

2. GROUND FLOOR + BASEMENT 1 (REFER TO DWG P00-A-CP003)	
NOTE 7:	
XRL FLOOR AREAS AT GROUND FLOOR AND BASEMENT 1 OF WKCD SITE ARE ASSUMED AS ANY FLOOR SPACE THAT IS CONSTRUCTED OR INTENDED FOR USE SOLELY AS ABOVE-GROUND VENT SHAFTS FOR THE EXPRESS RAIL LINK AS STATED IN DEVELOPMENT PLAN (NOTE 1). ALSO, XRL FLOOR AREA = GROSS FLOOR AREA OF ANY FOR ESTIMATED XRL GFA CALCULATION UNDER MASTER REGISTER, EXACT XRL GFA REFER TO SEPARATE SUBMISSION FOR WEST KOWLOON TERMINUS.	
TOTAL XRL GFA (NOTE 7):	
XRL GFA AT:	
"OU (MU) ZONE" OF GROUND FLOOR	= [1] = 855 m ² 4400 (NOTE 7) i.e. NOT COUNTED
"OU (ACECU) ZONE" OF GROUND FLOOR	= [2] = 849 m ² 3600 (NOTE 8) i.e. NOT COUNTED
"O ZONE" OF GROUND FLOOR & BASEMENT 1	= [3] + [4] = 822 + 804 = 1,626 m ²
"OU (MU) ZONE" OF BASEMENT 1	= [4] = 2,131 m ²
"OU (ACECU) ZONE" OF BASEMENT 1	= [5] = 875 m ²
OVERALL COUNTED GFA = [3] + [4] + [5] =	4,632 m ²

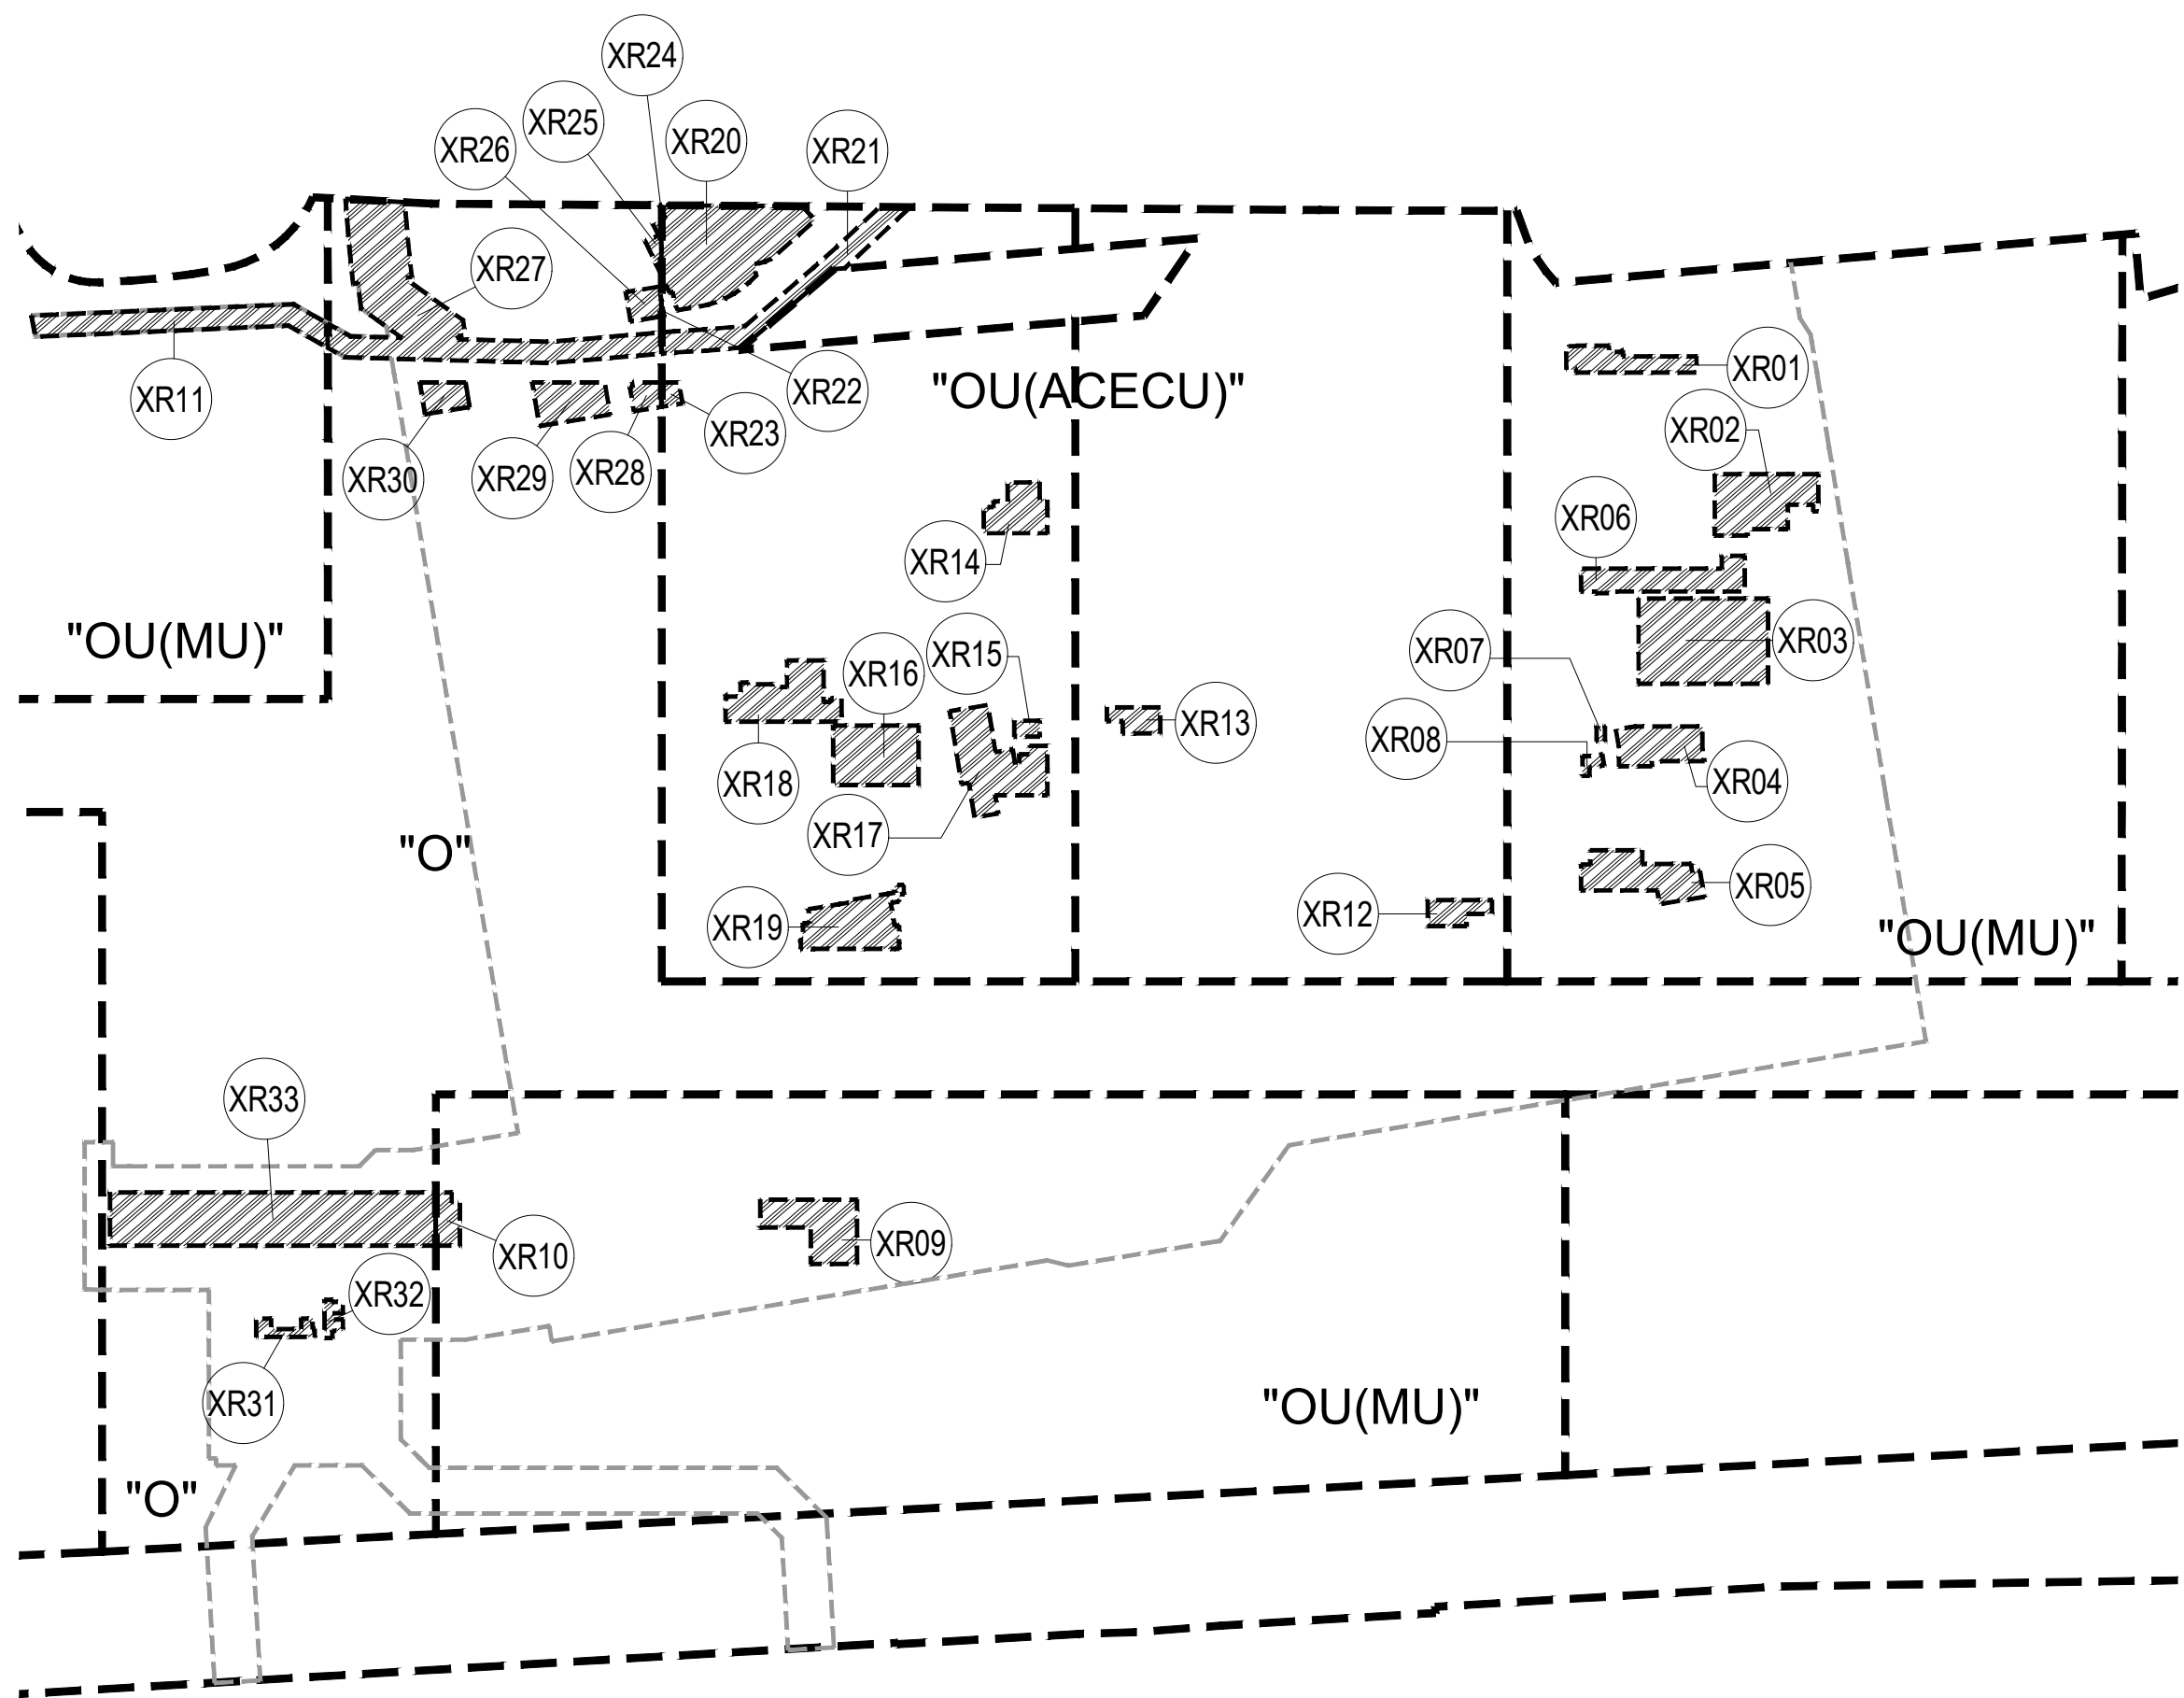

B.D. REF: BD 2403312
F.S.D. REF: FP 627927 IV
KEY PLAN

Buildings Department

Amended Plan

NOTES:

PACKAGE 01 IS THE PROPOSED SUBMISSION AREA OF MAJOR VEHICULAR ACCESS ROAD AT GROUND FLOOR, BASEMENTS AND ASSOCIATED AREA SPACES (INCLUDING BUT NOT LIMITED TO, ESSENTIAL PLANT ROOMS, PUBLIC ACCESS, COMMUNAL LOBBY, MEANS OF ESCAPE AND MEANS OF ACCESS) OF WEST KOWLOON CULTURAL DISTRICT, SUBJECT TO DESIGN AND SUBMISSION OF GENERAL BUILDING PLAN FOR ACTUAL EXTENT.

ALL FLOOR LEVELS ARE FFL'S TO PRINCIPAL DATUM (mPD)

ACTUAL EXTENT AND LAYOUTS OF ALL PACKAGES SUBJECT TO DESIGN AND SUBMISSION OF GENERAL BUILDING PLAN.

INDICATION, LEGEND AND ABBREVIATION:

- PROPOSED SITE BOUNDARY OF KIL 11260
- PROPOSED BUILDING OUTLINE
- EMERGENCY VEHICULAR ACCESS (EVA) SERVING WEST KOWLOON TERMINUS
- PROPOSED EMERGENCY VEHICULAR ACCESS (EVA) SUBJECT TO DESIGN AND SUBMISSION OF GENERAL BUILDING PLAN
- SUBMISSION PACKAGE NUMBER (e.g. 01, 02, etc.)
- EXTENT OF DECK TO BE CONSTRUCTED BY MTRC, REFER TO SEPARATE SUBMISSION FOR EXACT EXTENT.
- XR: AREA OF WEST KOWLOON TERMINUS EXCLUDED FROM SUBMISSION PACKAGES AND NOT FORM PART OF THE SUBMISSION
- P02: BUILDING PARCEL NUMBER
- FB: PROPOSED FOOTBRIDGE
- N.B.A.: NON BUILDING AREA
- N.L.F.: PROPOSED NORTHERN LANDING FACILITY
- SH: PROPOSED SHELTER
- SLW: PROPOSED SOUTHERN LANDING FACILITY
- SW: PROPOSED SUBWAY
- WKT: WEST KOWLOON TERMINUS
- XRL: EXPRESS RAIL LINK (WEST KOWLOON TERMINUS)

O	28-02-2025	Twenty-second Amendment Submission	W.L.
N	29-03-2025	Twenty-first Amendment Submission	B.C.
M	08-06-2025	Twentieth Amendment Submission	B.C.
L	20-08-2025	Nineteenth Amendment Submission	B.C.
K	01-12-2020	Eighteenth Amendment Submission	B.C.
J	11-09-2019	Seventeen Amendment Submission	B.C.
I	29-11-2018	Fifteenth Amendment Submission	B.C.
H	05-09-2018	Twelve Amendment Submission	P.C.
G	04-08-2017	Eleventh Amendment Submission	P.C.
F	04-03-2014	Sixth Amendment Submission	P.C.
E	04-12-2015	Fifth Amendment Submission	P.C.
D	19-05-2015	Fourth Amendment Submission	EUC
C	23-01-2014	Third Amendment Submission	EUC
B	30-07-2014	Second Amendment Submission	EUC
A	31-03-2014	First Submission	EUC
REV.	DATE	DESCRIPTION	INITIAL

AUTHORISED PERSON'S SIGNATURE

Ling Wilson Hin Tat
Authorized Person (Architect)
AP/04/1409

JOB TITLE: District Wide Control Plan & Master Register
West Kowloon Cultural District
(KIL 11260)

DRAWING TITLE
Control Plan (Gf)

SCALE	1:1500	PRINTED	A0
CHECKED	G.Y.	DATE	28-02-2025
APPROVED	W.L.	DATE	28-02-2025
DRAWN	TTY	DATE	28-02-2025

CONTRACT NO.:

ZONING NO.:

DRAWING NO.:

P00-A-CP002

CAD REF NAME: P00-A-CP002.dwg

EMPLOYER

westK
西九文化區

BDS OFFICIAL USE