

SITE COVERAGE OF GREENERY
SCALE 1 : 2000

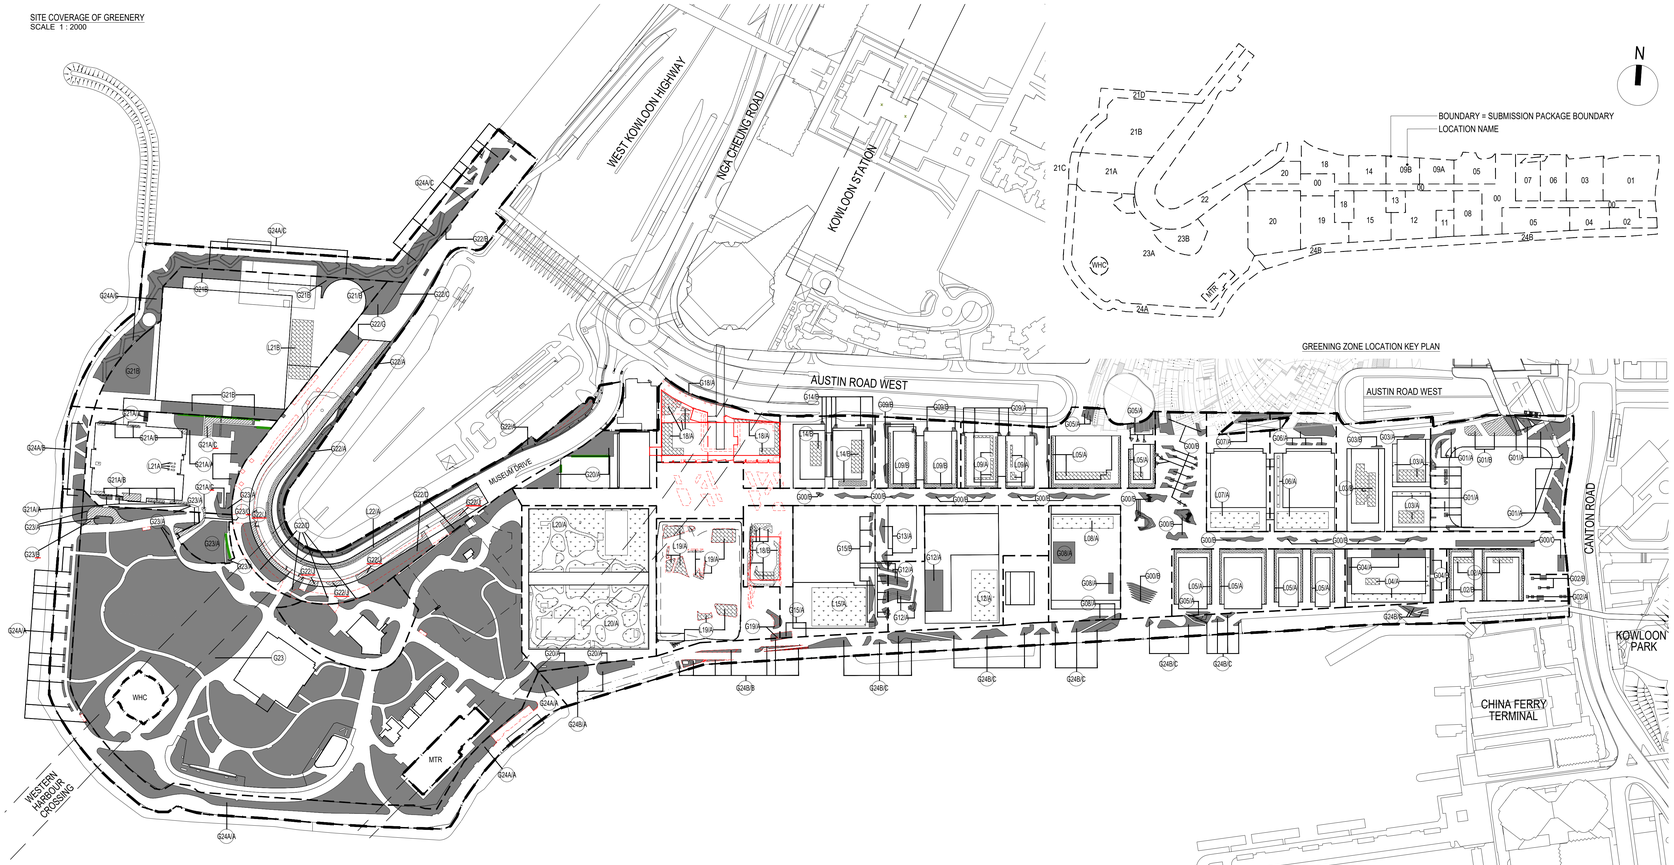

GREENING ZONE LOCATION KEY PLAN


DOMESTIC BUILDING FOOTPRINT & ROOF AREA
SCALE 1 : 3000

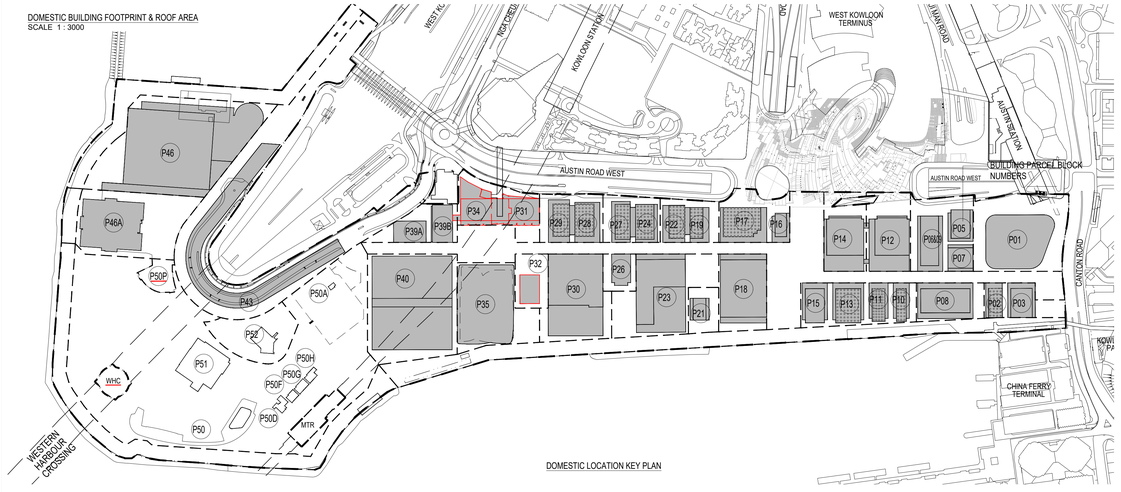


DOMESTIC LOCATION KEY PLAN

SITE COVERAGE OF GREENERY - CALCULATION
SCALE 1 : 2000

LEGEND FOR GREENERY SYMBOL :

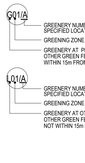


LEGEND FOR TYPE OF GREENERY :

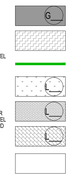

= GREENERY AREA AT PRIMARY ZONE (UNDER PNAP APP-152 PARA. 10 TABLE 2)
= OTHER GREENING FEATURES (COVERED GREENERY AREA / WATER FEATURE) AT PRIMARY ZONE (UNDER PNAP APP-152 APPENDIX D PARA 3)
= VERTICAL GREENING
= TERRACE GREENING (NOT WITHIN 15M FROM GROUND)
= SET BACK GREENING (NOT WITHIN 15M FROM GROUND)
= ROOF GREENING (NOT WITHIN 15M FROM GROUND)
= PROPOSED BUILDING OUTLINE
OTHER GREENING FEATURES
= GREENERY AREA AT OTHER LOCATION (NON-PRIMARY ZONE)

DOMESTIC BUILDING FOOTPRINT AREA
SCALE 1 : 2000

= DOMESTIC BLOCK FOORPRINT
= BUILDING OUTLINE
P02 : BUILDING PARCEL NUMBER

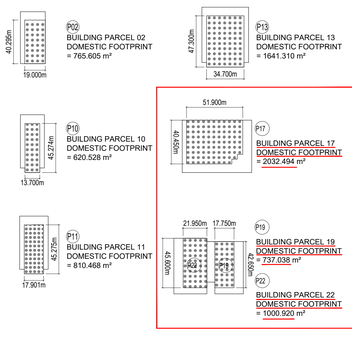

DOMESTIC BLOCK FOOTPRINT AND ROOF AREA

PARCEL 02	=	765.605 m²
PARCEL 10	=	620.528 m²
PARCEL 11	=	810.468 m²
PARCEL 13	=	1641.310 m²
PARCEL 17	=	2032.494 m²
PARCEL 19	=	737.038 m²
PARCEL 22	=	1000.920 m²
PARCEL 24	=	1242.595 m²
PARCEL 27	=	1010.515 m²
PARCEL 28	=	1197.251 m²
PARCEL 29	=	1031.029 m²
Total	=	12089.753 m²

(1.) OTHER GREENING	PACKAGE NUMBER	(1.) PRIMARY ZONE GREENERY AREA	TOTAL	(2.) GREENERY AREA AT OTHER LOCATION (NON-PRIMARY ZONE)	TOTAL	TOTAL
		GREENERY AREA AT PRIMARY ZONE + GREENING WITHIN 15m FROM GROUND LEVEL		GREENERY AREA ON TERRACE / GREENERY AREA AT OTHER		
(1A.) OTHER GREENING FEATURES AT PRIMARY ZONE		G/PA AREA = 0 m²				
SC AREA = m² (A LEVEL WITHIN 15m OF THE GROUND: YES / NO)		G/P2 AREA = 2,148 m²				
ACCOUNTABLE = m² (WATER FEATURES REDUCTION FACTOR: 50%)		G/P3 AREA = 502 m²				
SC AREA = m² (A LEVEL WITHIN 15m OF THE GROUND: YES / NO)	00		2,650 m²			2,650 m²
ACCOUNTABLE = m² (WATER FEATURES REDUCTION FACTOR: 50%)						
SUB-TOTAL = 0.000 m²						
(1B.) OTHER GREENING FEATURES AT OTHER LOCATION	01	G/1A AREA = 1,726 m²	1,947 m²			1,947 m² *
		G/1B WATER FEATURE = 443 x 50% = 221 m²				
SC AREA = m² (A LEVEL WITHIN 15m OF THE GROUND: YES / NO)	02	G/2A AREA = 50 m²	94 m²	G/2A AREA = 185 m²	648 m²	742 m²
ACCOUNTABLE = m² (WATER FEATURES REDUCTION FACTOR: 50%)		G/2B AREA = 44 m²		G/2B AREA = 463 m²		
	03	G/3A AREA = 73 m²	86 m²	G/3A AREA = 262 m² AREA = 523 m²	1,360 m²	1,446 m²
SC AREA = m² (A LEVEL WITHIN 15m OF THE GROUND: YES / NO)		VERTICAL GREENING = 0 m²				
ACCOUNTABLE = m² (WATER FEATURES REDUCTION FACTOR: 50%)		G/3B AREA = 13 m²		G/3B AREA = 0 m² AREA = 575 m²		
		VERTICAL GREENING = 0 m²				
SC AREA = m² (A LEVEL WITHIN 15m OF THE GROUND: YES / NO)	04	G/4A AREA = 450 m²	587 m²	G/4A AREA = 585 m² AREA = 78 m²	638 m²	1,225 m²
		G/4B AREA = 137 m²		G/4B AREA = 0 m² AREA = 0 m²		
ACCOUNTABLE = m² (WATER FEATURES REDUCTION FACTOR: 50%)	05	G/5A AREA = 400 m²	400 m²	G/5A AREA = 0 m² AREA = 2,308 m²	2,308 m²	2,708 m²
		VERTICAL GREENING = 0 m²				
SC AREA = m² (A LEVEL WITHIN 15m OF THE GROUND: YES / NO)	06	G/6A AREA = 534 m²	534 m²	G/6A AREA = 872 m² AREA = 0 m²	872 m²	1,406 m²
		VERTICAL GREENING = 0 m²				
ACCOUNTABLE = m² (FEATURES REDUCTION FACTOR: % NOT APPLICABLE)	07	G/7A AREA = 187 m²	187 m²	G/7A AREA = 676 m² AREA = 0 m²	676 m²	863 m²
		VERTICAL GREENING = 0 m²				
	08	G/8A AREA = 589 m²	589 m²	G/8A AREA = 611 m² AREA = 0 m²	611 m²	1,200 m²
SC AREA = m² (A LEVEL WITHIN 15m OF THE GROUND: YES / NO)	09A	G/9A AREA = 92 m²	92 m²	G/9A AREA = 0 m² AREA = 548 m²	548 m²	640 m²
		VERTICAL GREENING = 0 m²				
ACCOUNTABLE = m² (FEATURES REDUCTION FACTOR: % NOT APPLICABLE)	09B	G/9B AREA = 139 m²	139 m²	G/9B AREA = 0 m² AREA = 572 m²	572 m²	711 m²
		VERTICAL GREENING = 0 m²				
	10	G/10A AREA = 0 m²	0 m²	G/10A AREA = 0 m² AREA = 0 m²	0 m²	0 m²
SUB-TOTAL = m²	11	G/11A AREA = 0 m²	0 m²	G/11A AREA = 0 m² AREA = 0 m²	0 m²	0 m²
	12	G/12A AREA = 1,054 m²	1,054 m²	G/12A AREA = 1,714 m² AREA = 0 m²	1,714 m²	2,768 m²
	13	G/13A AREA = 111 m²	111 m²	G/13A AREA = 0 m² AREA = 0 m²	0 m²	111 m²
	14	G/14A AREA = 0 m²	262 m²	G/14A AREA = 0 m² AREA = 0 m²	703 m²	965 m²
		G/14B AREA = 262 m²		G/14B AREA = 0 m² AREA = 703 m²		
		VERTICAL GREENING = 0 m²				
	15	G/15A AREA = 26 m²	460 m²	G/15A AREA = 0 m² AREA = 0 m²	1,763 m²	2,223 m²
		G/15B AREA = 434 m²		G/15B AREA = 1,763 m² AREA = 0 m²		
	18	G/18A AREA = 129 m²	129 m²	G/18A AREA = 0 m² AREA = 933 m²	1,437 m²	1,566 m²
		VERTICAL GREENING = 0 m²				
		G/18B AREA = 0 m²		G/18B AREA = 0 m² AREA = 504 m²		
	19	G/19A AREA = 88 m²	88 m²	G/19A AREA = 0 m² AREA = 955 m²	955 m²	1,043 m²
	20	G/20A AREA = 1,287 m²	1,787 m²	G/20A AREA = 7,215 m² AREA = 0 m²	7,215 m²	9,002 m² *
		VERTICAL GREENING = 500 m²				
	21A	G/21A AREA = 1,501 m²	2,581 m²	G/21A AREA = 20 m² AREA = 0 m²	20 m²	2,601 m² *
		G/21B COVERED GREENERY = 300 x 50% = 150 m²				
		G/21C WATER FEATURE = 304 x 50% = 144 m²				
		VERTICAL GREENING = 376 m²				
	21B	G/21B AREA = 3,641 m²	3,641 m²	G/21B AREA = 0 m² AREA = 0 m²	0 m²	3,641 m²
	22	G/22A AREA = 3,597 m²	6,650 m²	G/22A AREA = 0 m² AREA = 1,981 m²	1,981 m²	8,631 m²
		G/22B AREA = 60 m²		G/22B AREA = 0 m² AREA = 0 m²		
		G/22C AREA = 254 m²				
		G/22D AREA = 2,696 m²				
		G/22E AREA = 343 m²				
		G/22F AREA = 813 m²				
		G/22G COVERED GREENERY = 756 x 50% = 368 m²				
	23	G/23A AREA = 52,728 m²	55,369 m²			55,369 m²
		VERTICAL GREENING FOR PARK = 0 m²				
		G/23B AREA = 2,285 m²				
		G/23C COVERED GREENERY = 0 x 50% = 0 m²				
		G/23D WATER FEATURE = 882 x 50% = 240 m²				
		VERTICAL GREENING FOR PARK RAMP = 42 m²				
	24A	G/24A AREA = 4,692 m²	4,692 m²			4,692 m²
	24C	G/24C AREA = 467 m²	467 m²			467 m² *
	24D	G/24D AREA = 4,642 m²	5,091 m²			5,091 m²
		VERTICAL GREENING = 449 m²				
	24B	G/24B AREA = 917 m²	3,312 m²			3,312 m²
		G/24E AREA = 330 m²				
		G/24F AREA = 2,065 m²				
SUB-TOTAL		42,942 m²		13,093 m² 10,338 m² 23,431 m²		114,368 m²

(1.) OTHER GREENING FEATURES
COVERED GREENERY AREA / WATER FEATURE
(G/1A + G/1B + G/2A + G/2B + G/3A + G/3B + G/4A + G/4B + G/5A + G/6A + G/6B + G/7A + G/8A + G/9A + G/9B + G/10A + G/11A + G/12A + G/12B + G/13A + G/14A + G/14B + G/15A + G/15B + G/18A + G/18B + G/19A + G/20A + G/21A + G/21B + G/21C + G/22A + G/22B + G/22C + G/22D + G/22E + G/22F + G/22G + G/23A + G/23B + G/23C + G/23D + G/24A + G/24B + G/24C + G/24D + G/24E + G/24F) = 1,736 m²
VERTICAL GREENING (VG)
(G/1A + G/2A + G/3A + G/4A + G/5A + G/6A + G/7A + G/8A + G/9A + G/9B + G/10A + G/11A + G/12A + G/12B + G/13A + G/14A + G/14B + G/15A + G/15B + G/18A + G/18B + G/19A + G/20A + G/21A + G/21B + G/22A + G/22B + G/22C + G/22D + G/22E + G/22F + G/23A + G/23B + G/23C + G/24A + G/24B + G/24C + G/24D + G/24E + G/24F) = 1367 m²

OVERALL TOTAL PRIMARY ZONE GREENERY AREA
TOTAL = 52,942 m² > 57,973 m² (REQUIRED) i.e. OK
(MINIMUM = 386,488 m² x 15% = 57,973 m² (ABOUT))

* COMPLETED GREENERY (UNDER SEPARATE SUBMISSION)

(1D.) OVERALL OTHER GREENING FEATURES TOTAL
TOTAL = 0.000 m²

DELETED

PART 1 UNDER SBDG (REQUIRED)

(1) SITE COVERAGE OF GREENERY AT PRIMARY ZONE
(UNDER PNAP APP-152 PARA. 10 TABLE 2)
= SITE AREA = 386,488 m² > 20,000 m²
MINIMUM SITE COVERAGE OF GREENERY AT PRIMARY ZONE
= NOT LESS THAN 15% OF SITE AREA
= 386,488 m² x 15% = 57,973 m² (ABOUT)
HENCE,
(OTHER GREENING FEATURES + GREENERY AREA) AT PRIMARY ZONE > 57,973 m²
= 0 + AREA AT PRIMARY ZONE > 57,973 m²
= GREENERY AREA AT PRIMARY ZONE > 57,973 m²

(2) SITE COVERAGE OF GREENERY AT OTHER LOCATION (NON-PRIMARY ZONE)

(3) PERCENTAGE OF TOTAL ACCOUNTABLE OTHER GREENING FEATURES
(UNDER PNAP APP-152 APPENDIX D PARA 3)
OTHER GREENING FEATURES x REDUCTION FACTOR < 30% OF TOTAL REQUIRED GREENERY AREA (115,946 m²)
HENCE, MAXIMUM AREA FOR OTHER AREA FEATURES x REDUCTION FACTOR < 34,784 m²

(4) OVERALL SITE COVERAGE OF GREENERY
(UNDER PNAP APP-152 PARA 10 TABLE 2)
= GREENERY AREA AT PRIMARY ZONE + GREENERY AT OTHER LOCATION > 30% OF SITE AREA
= GREENERY AREA AT PRIMARY ZONE + GREENERY AT OTHER LOCATION > 30% x 386,488 m² OR 115,946 m²

PART 2 DEVELOPMENT PLAN (UNDER PLANNING DEPARTMENT) (REQUIRED)
MIN. GREEN COVERAGE FOR THE WHOLE #WCD (REQUIRED UNDER DEVELOPMENT PLAN)
= 30% OF SITE AREA
= 30% x 386,488 m² OR 115,946 m²
THE PARK AREA
= PACKAGE 23 AREA
= 80,458,721 m² = 6,467,562 m² = 86,926 m²
MIN. GREEN COVERAGE FOR THE PARK (REQUIRED UNDER DEVELOPMENT PLAN)
= 60% OF THE PARK AREA
= 60% x 86,926 m² OR 52,156 m²

PART 1 UNDER SBDG (PROPOSED)

(1) SITE COVERAGE OF GREENERY AT PRIMARY ZONE
(UNDER PNAP APP-152 PARA 10 TABLE 2)
= GREENERY AREA AT PRIMARY ZONE + COVERED GREENERY + WATER FEATURE + VERTICAL GREENING / SITE AREA x 100%
= 52,947 m² / 386,488 m² x 100%
= 24.03% (PROPOSED) > 15% (REQUIRED UNDER SBD GUIDLINE) i.e. OK

(2) SITE COVERAGE OF GREENERY AT OTHER LOCATION (NON-PRIMARY ZONE)
= 23,421 m²


(3) PERCENTAGE OF TOTAL ACCOUNTABLE OTHER GREENING FEATURES
(UNDER PNAP APP-152 APPENDIX D PARA 3)
= WATER FEATURES (GRASS PAVER/GREEN ROOF/COVERED PLANTER x REDUCTION FACTOR + VERTICAL GREENING / TOTAL REQUIRED GREENERY AREA x 100%
= 1,136 m² + 1,367 m² (VG) / 386,488 m² x 30% x 100%
= 2503 m² / 115,946 m² (ABOUT) x 100%
= 2.16% (PROPOSED) < 30% OF THE TOTAL REQUIRED GREENERY AREAS i.e. OK

(4) OVERALL SITE COVERAGE OF GREENERY
(UNDER PNAP APP-152 PARA 10 TABLE 2)
= (1) GREENERY AREA AT PRIMARY ZONE + (2) GREENERY AREA AT OTHER LOCATION (NON-PRIMARY ZONE) / SITE AREA x 100%
= 52,947 m² + 23,421 m² / 386,488 m² x 100%
= 30.11% (PROPOSED) > 30% (REQUIRED) i.e. OK

PART 2 DEVELOPMENT PLAN (UNDER PLANNING DEPARTMENT) (PROPOSED)
GREEN COVERAGE FOR THE WHOLE #WCD (PROPOSED)
= (1) SITE COVERAGE OF GREENERY PRIMARY ZONE + (2) SITE COVERAGE OF GREENERY AT OTHER LOCATION (NON-PRIMARY ZONE) / SITE AREA x 100%
= 52,947 m² + 23,421 m² x 100% / 386,488 m²
= 30.11% (PROPOSED) > 30% (REQUIRED) i.e. OK
GREEN COVERAGE FOR THE PARK (PROPOSED)
= GREENERY AT PACKAGE 23 / PACKAGE 23 AREA x 100%
= 55,369 m² / 86,926 m² x 100%
= 63.70% (PROPOSED) > 60% i.e. OK

B.D. REF: BD 2/4033/12
F.S.D. REF: FP 8/27927 IV

KEY PLAN

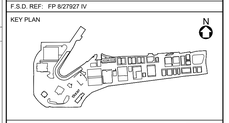

Buildings Department
Amended Plan

NOTES:

ACTUAL EXTENT AND LAYOUTS OF ALL PACKAGES SUBJECT TO DESIGN AND SUBMISSION OF GENERAL BUILDING PLAN.

REV.	DATE	DESCRIPTION	INITIAL
O	28.02.2025	Twenty-second Amendment Submission	W.L.
N	29.03.2023	Twenty-first Amendment Submission	B.C.
M	23.06.2021	Nineteen Amendment Submission	B.C.
L	01.12.2020	Eighteenth Amendment Submission	B.C.
K	11.09.2020	Seventeen Amendment Submission	B.C.
J	29.11.2019	Fifteenth Amendment Submission	B.C.
I	16.01.2019	Thirteenth Amendment Submission	P.C.
H	05.09.2018	Twelve Amendment Submission	P.C.
G	04.08.2017	Eleventh Amendment Submission	P.C.
F	04.03.2016	Sixth Amendment Submission	P.C.
E	04.12.2015	Fifth Amendment Submission	EUC
D	19.06.2015	Fourth Amendment Submission	EUC
C	23.01.2014	Third Amendment Submission	EUC
B	30.07.2014	Second Amendment Submission	EUC
A	31.03.2014	First Amendment Submission	EUC
	30.05.2013	First Submission	EUC

AUTHORISED PERSON'S SIGNATURE

Ling Wilson Hin Tat
Authorized Person (Architect)
AP(A) 84/05

JOB TITLE: District Wide Control Plan & Master Register
West Kowloon Cultural District
(KIL 11260)

DRAWING TITLE:
SBDG Compliance (6) -
Site Coverage of Greenery & Domestic Building Footprint & Roof Area

SCALE	AS SHOWN	PRINTED	A0
CHECKED	G.Y.	DATE	28-02-2025
APPROVED	W.L.	DATE	28-02-2025
DRAWN	TTY	DATE	28-02-2025

CONTRACT NO. -

ZONING NO.

DRAWING NO. P00-A-CP010 REV. O

CAD REF NAME: P00-A-CP010.dwg

EMPLOYER

westK
西九文化區

BD'S OFFICIAL USE