

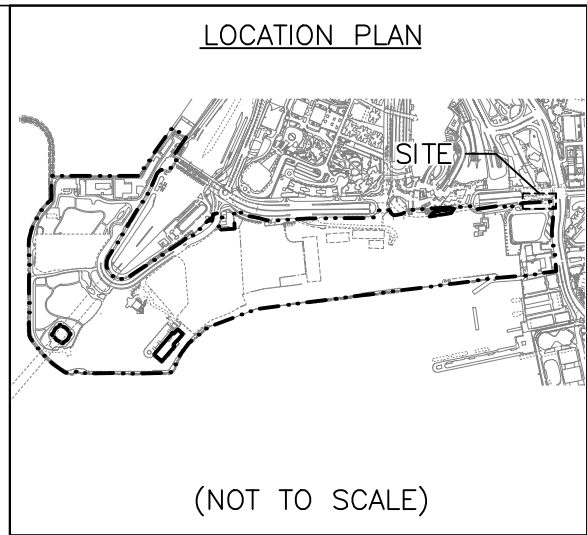
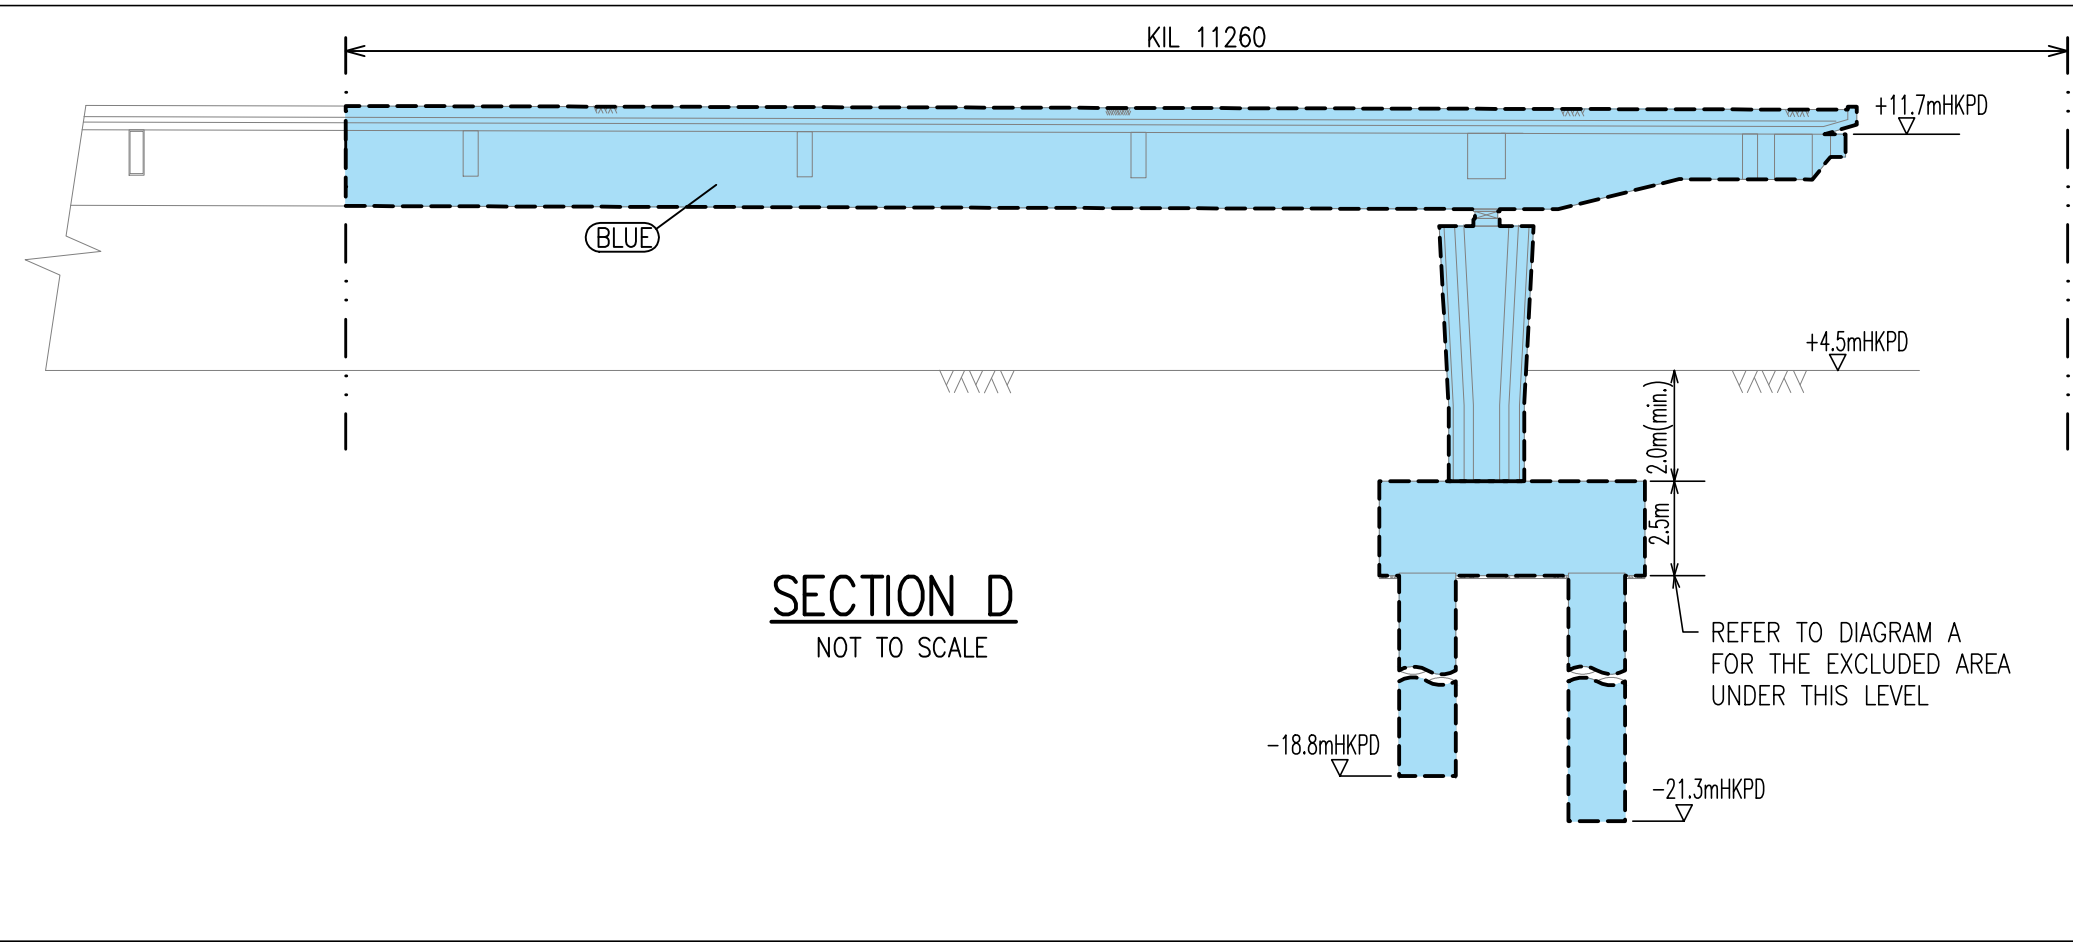
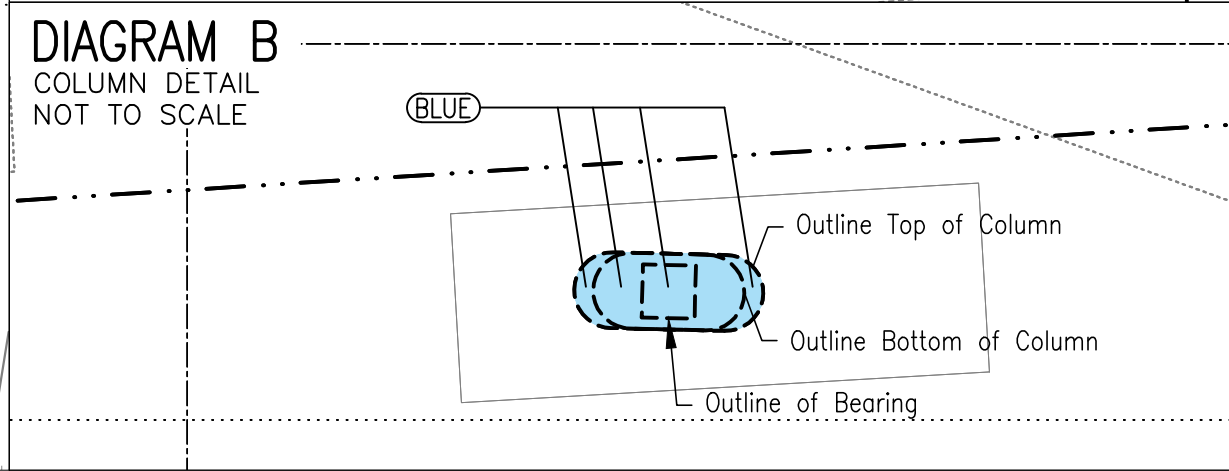
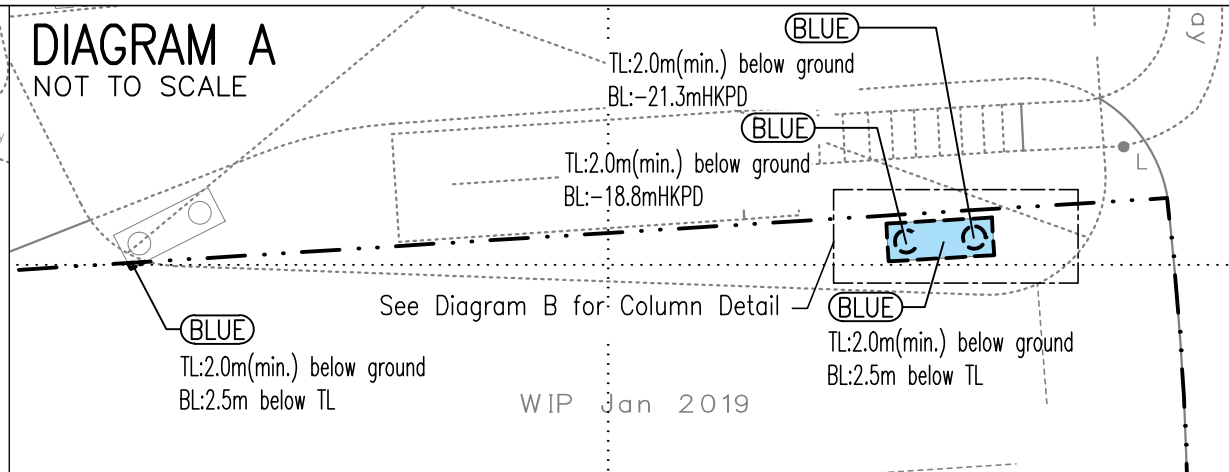
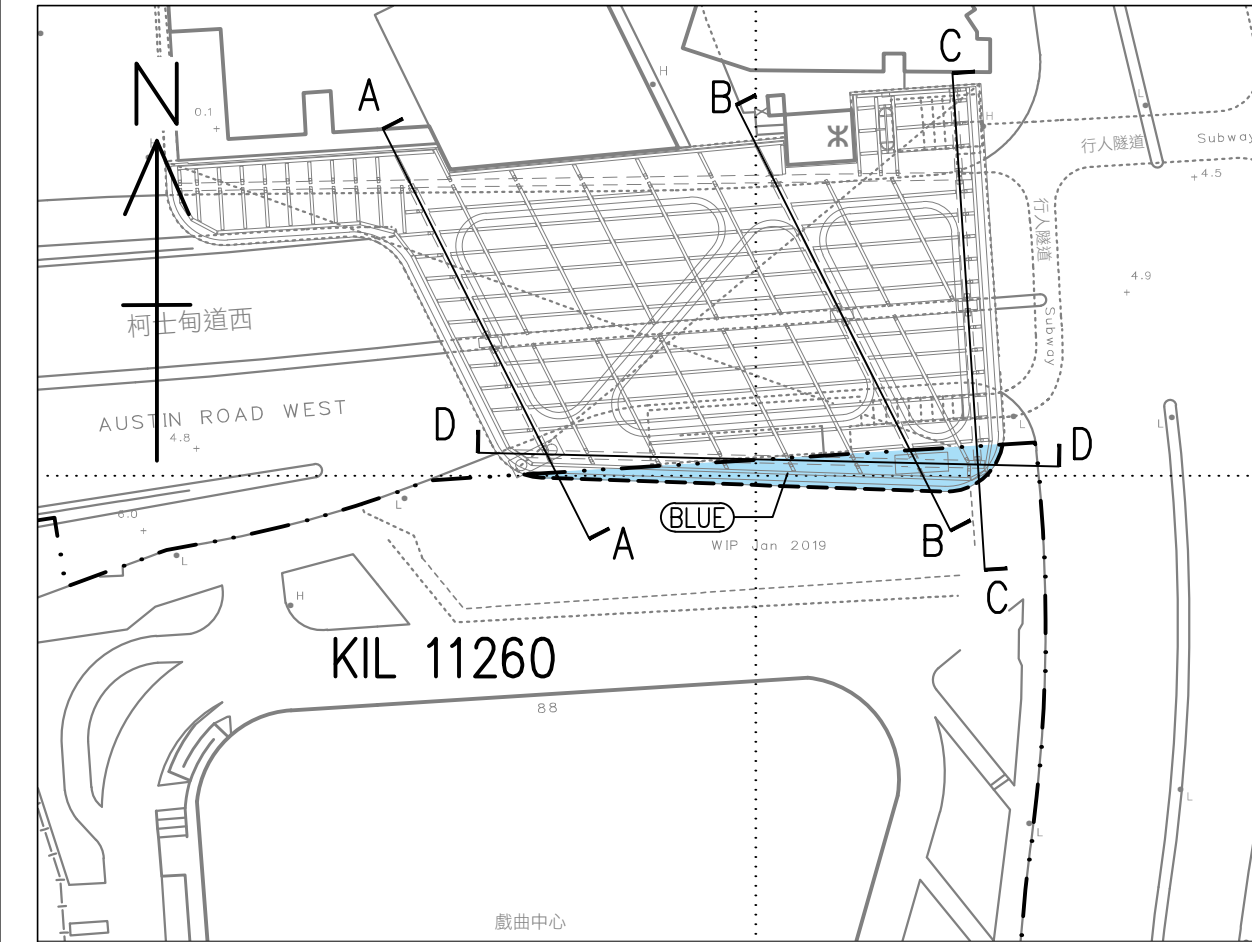
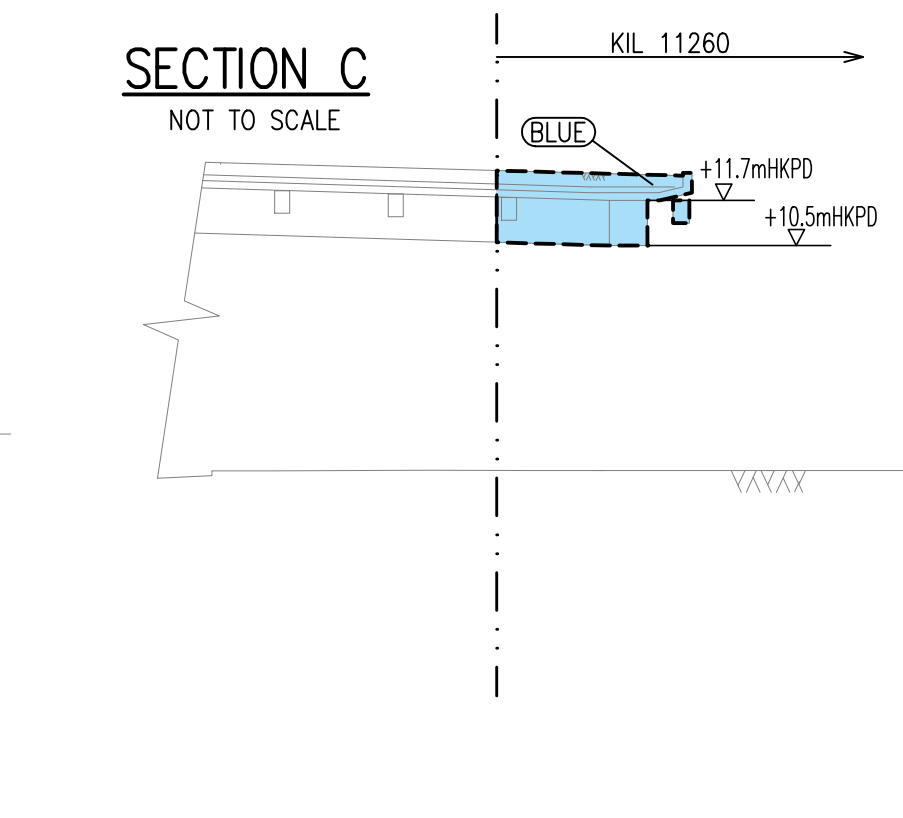


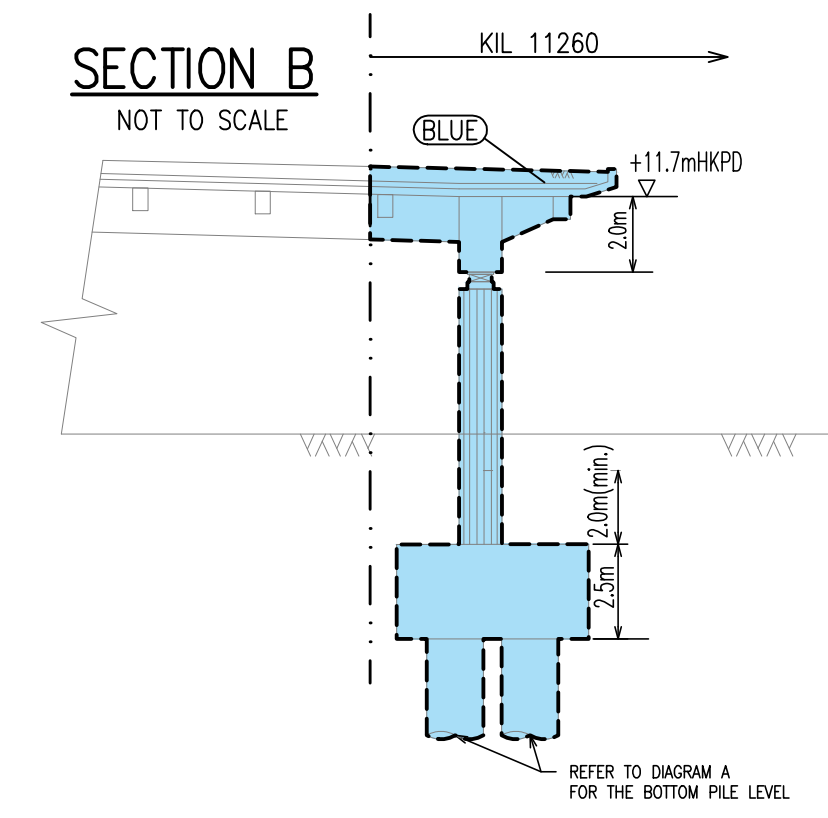

LEGEND

---	BOUNDARY OF KIL 11260
---	OUTLINE OF EXCLUDED AREA
---	OUTLINE OF FEATURE
---	STRATUM OF EXCLUDED AREA
mHKPD	HONG KONG PRINCIPAL DATUM (APPROXIMATE IN METRE)
TL	TOP LEVEL
BL	BOTTOM LEVEL
min.	minimum

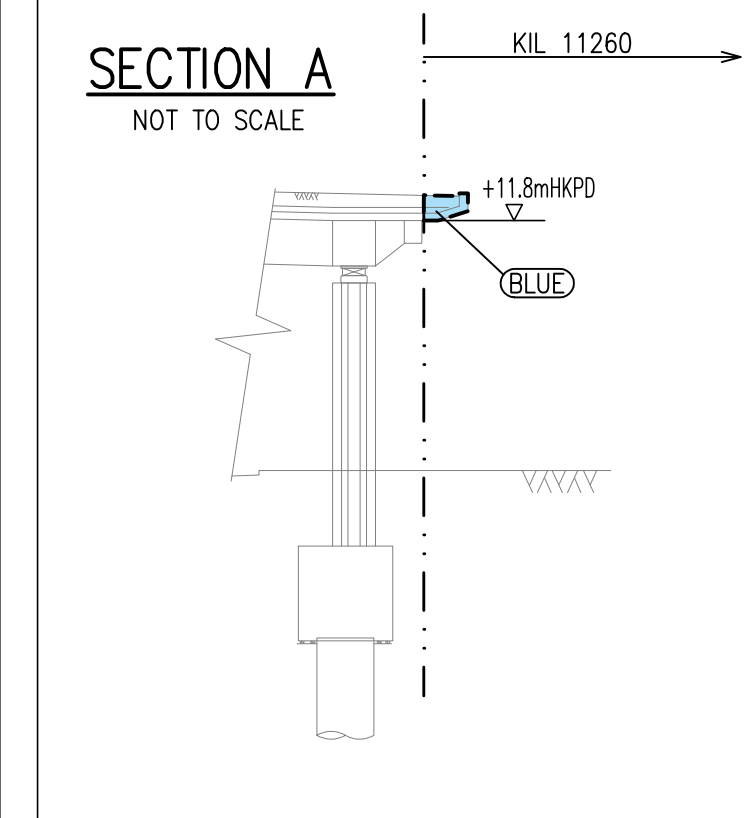

LAND MARKER (1980) H.K. Co., LTD.
標誌測量(1980)香港有限公司

Survey District : KOWLOON

Survey Sheet : 11-NW-24D

Plan No.: 4192-EA02

KOWLOON INLAND LOT No. 11260
EXCLUDED AREA FOR NOISE MITIGATION DECK

SIGNED BY

JOSEPH Y C WONG
AUTHORIZED LAND SURVEYOR FHKIS MRICS RPS(LS)