
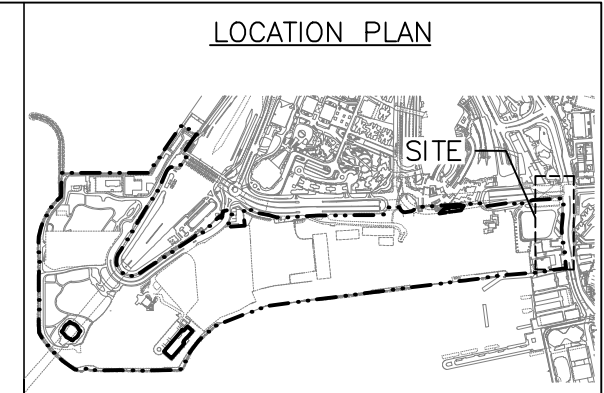
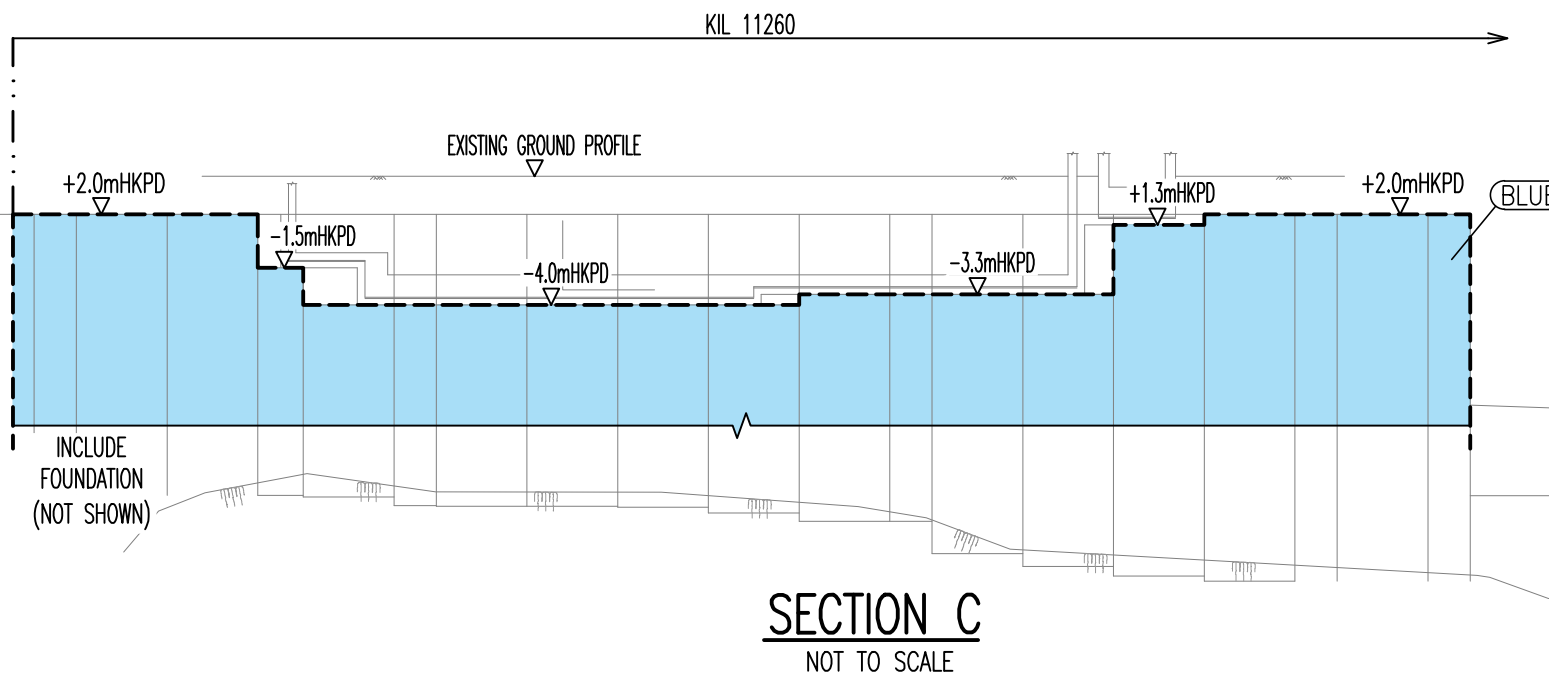
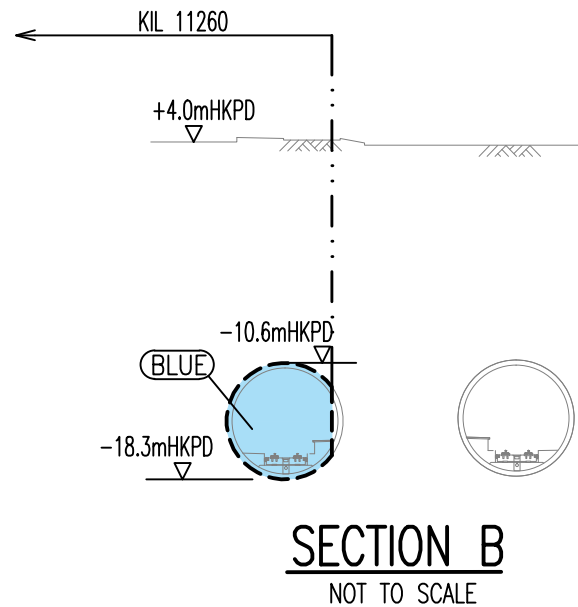
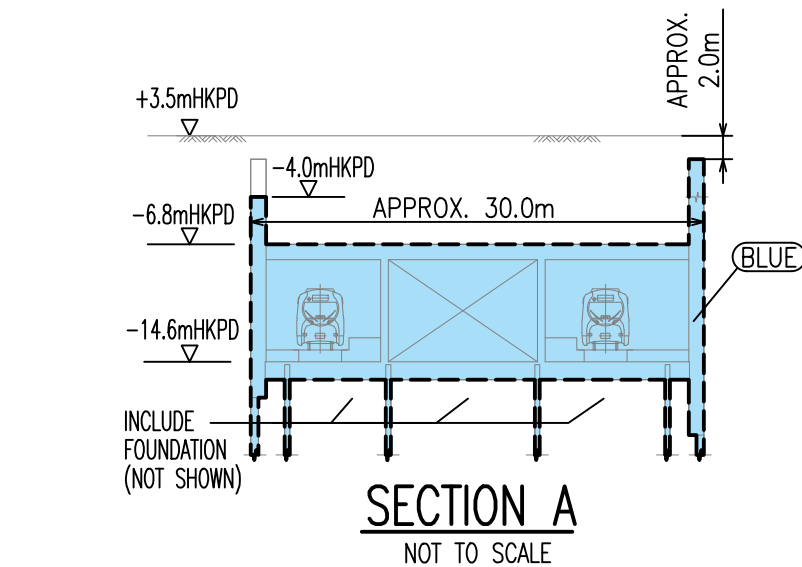


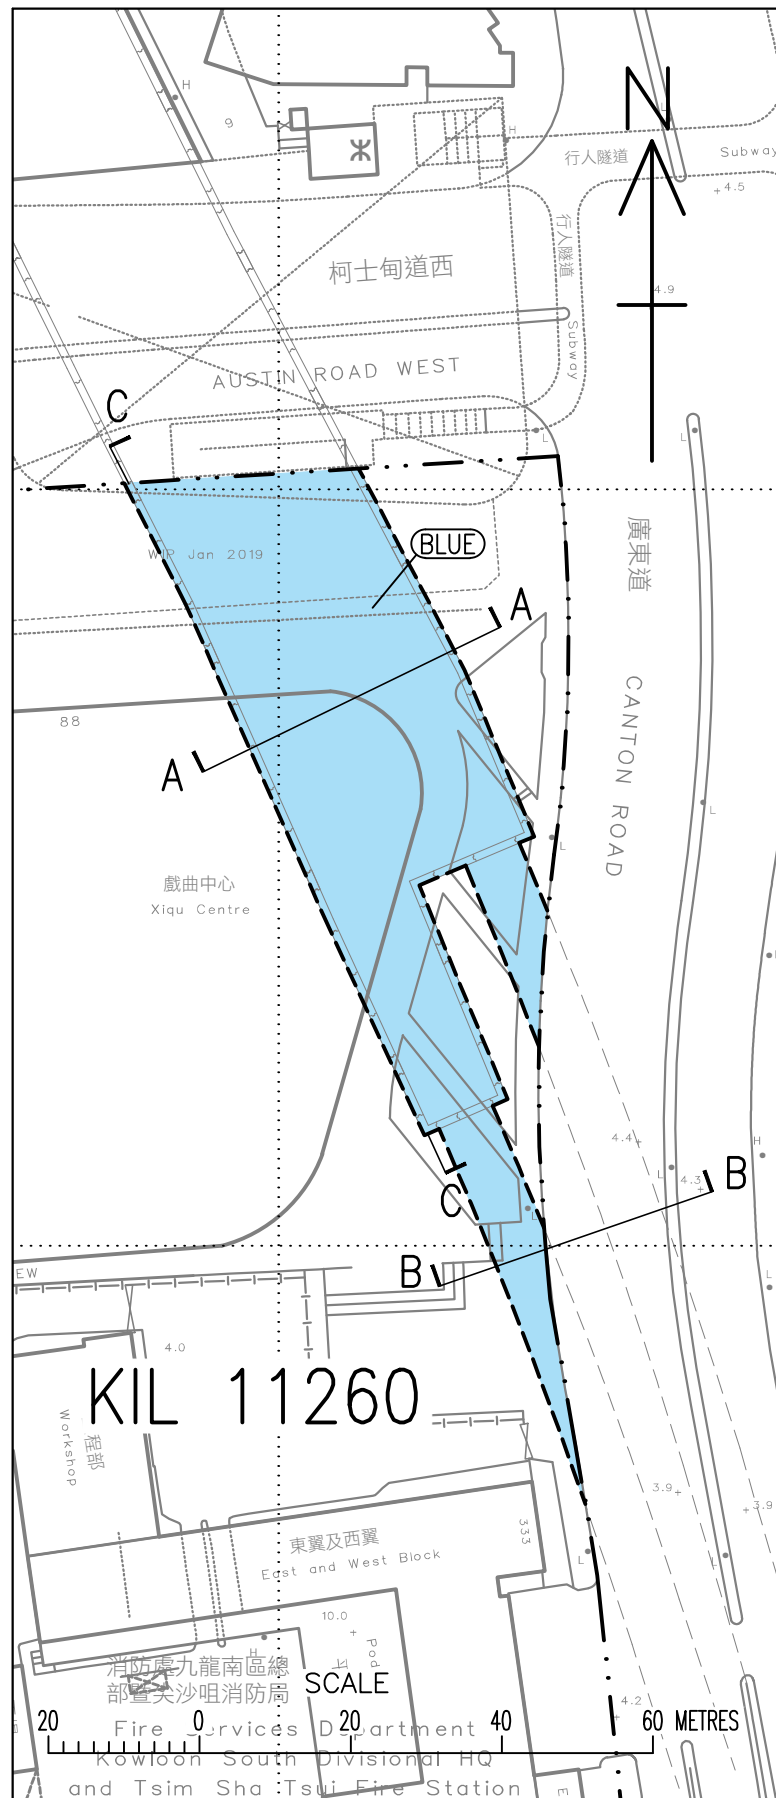

LEGEND

- BOUNDARY OF KIL 11260
- OUTLINE OF EXCLUDED AREA
- OUTLINE OF FEATURE
- BLUE STRATUM OF EXCLUDED AREA
- mHKPD HONG KONG PRINCIPAL DATUM (APPROXIMATE IN METRE)

LAND MARKER (1980) H.K. Co., LTD.
標誌測量(1980)香港有限公司

Survey District : KOWLOON
Survey Sheet : 11-NW-24D
Plan No.: 4192-EA08

KOWLOON INLAND LOT No. 11260 EXCLUDED AREA FOR KSL RAILWAY

SIGNED BY

JOSEPH Y C WONG
AUTHORIZED LAND SURVEYOR FHKIS MRICS RPS(LS)

Date: 27 NOVEMBER 2019