


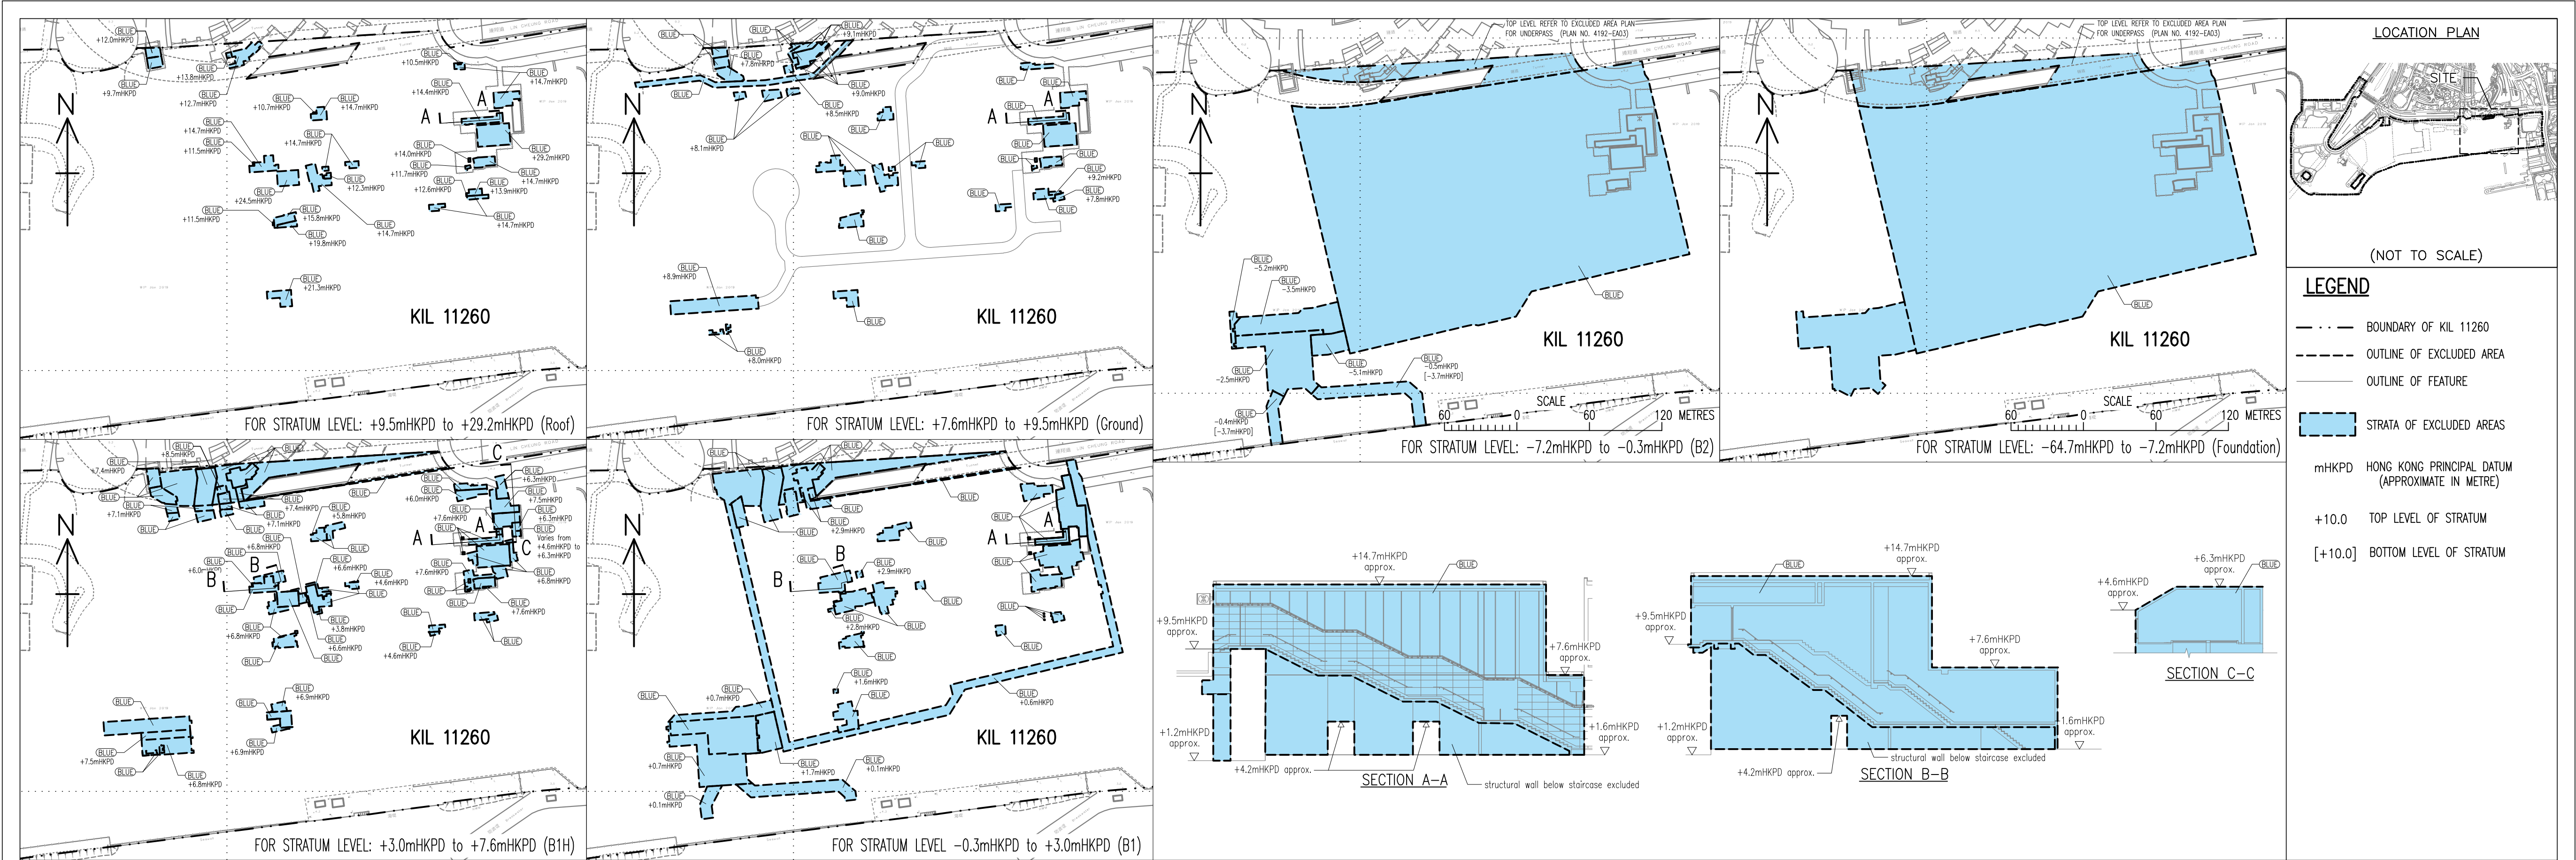

LAND MARKER (1980) H.K. Co., LTD.
標記測量(1980)香港有限公司

Survey District : KOWLOON

Survey Sheet : 11-NW-24C & 11-SW-4A

Plan No.: 4192-EA09

KOWLOON INLAND LOT No. 11260 EXCLUDED AREAS FOR EXPRESS RAIL LINK

SIGNED BY

JOSEPH Y C WONG
AUTHORIZED LAND SURVEYOR FHKIS MRICS RPS(LS)

Date: 27 NOVEMBER 2019