

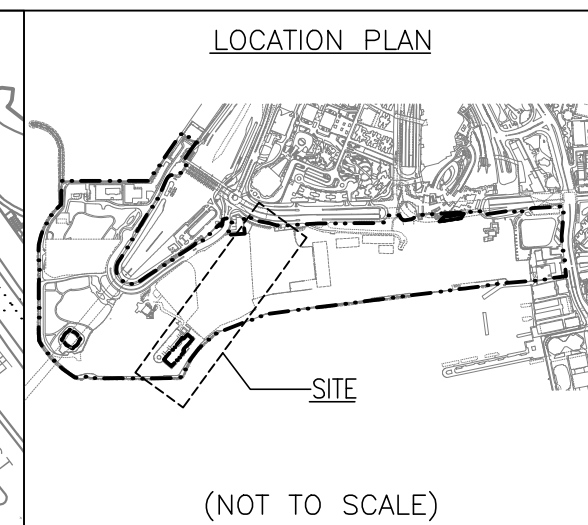


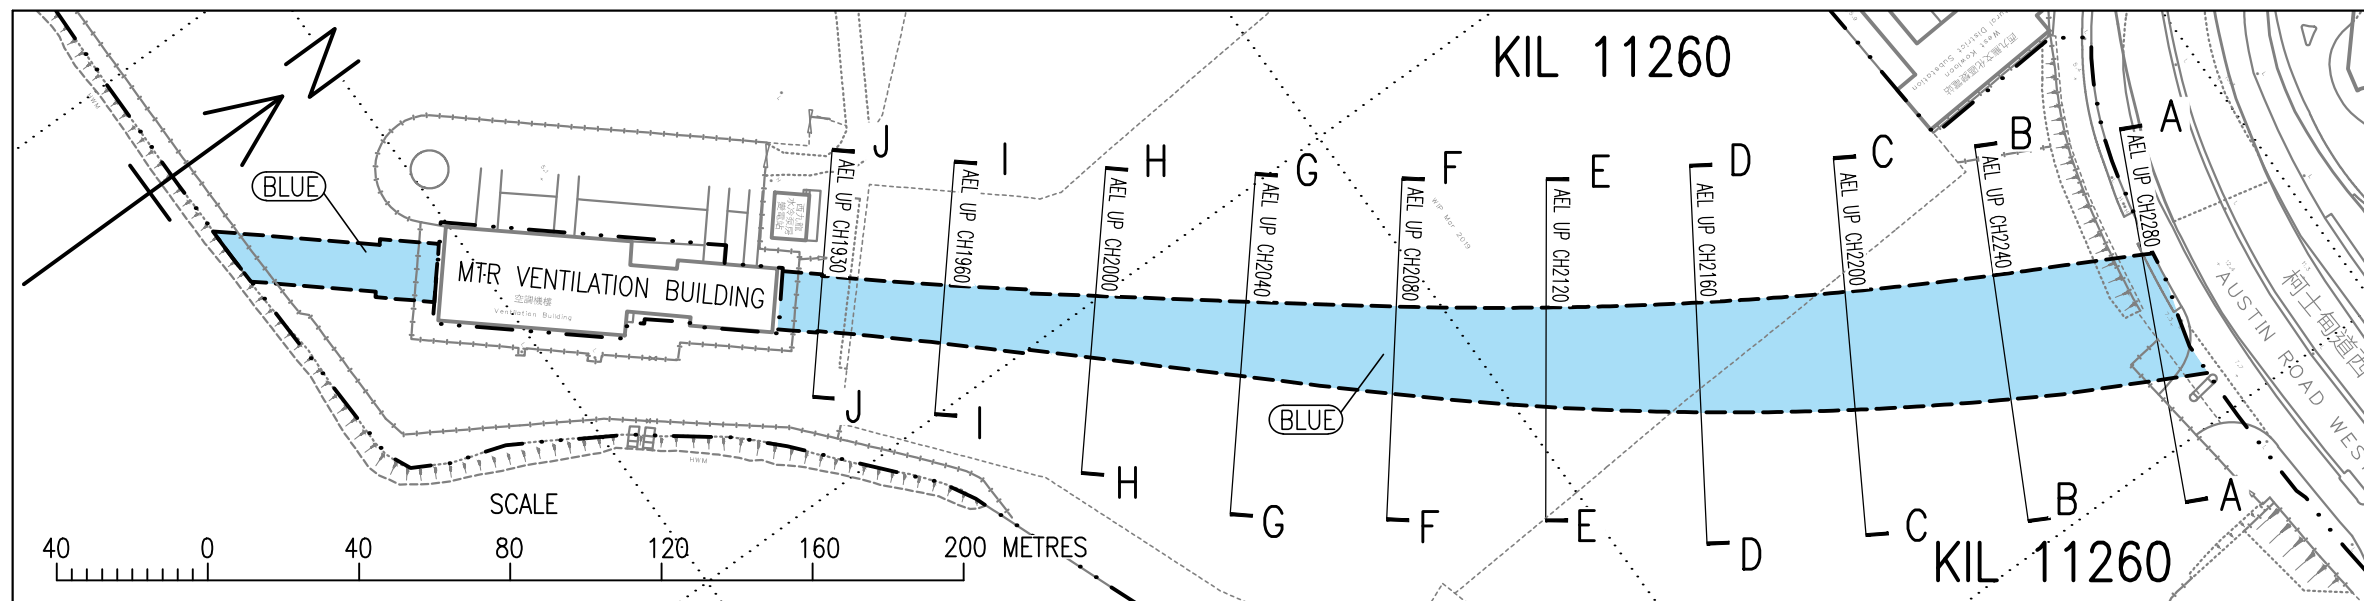

LEGEND

- BOUNDARY OF KIL 11260
- - - OUTLINE OF EXCLUDED AREA
- OUTLINE OF FEATURE
- STRATA OF EXCLUDED AREAS
- mHKPD HONG KONG PRINCIPAL DATUM (APPROXIMATE IN METRE)

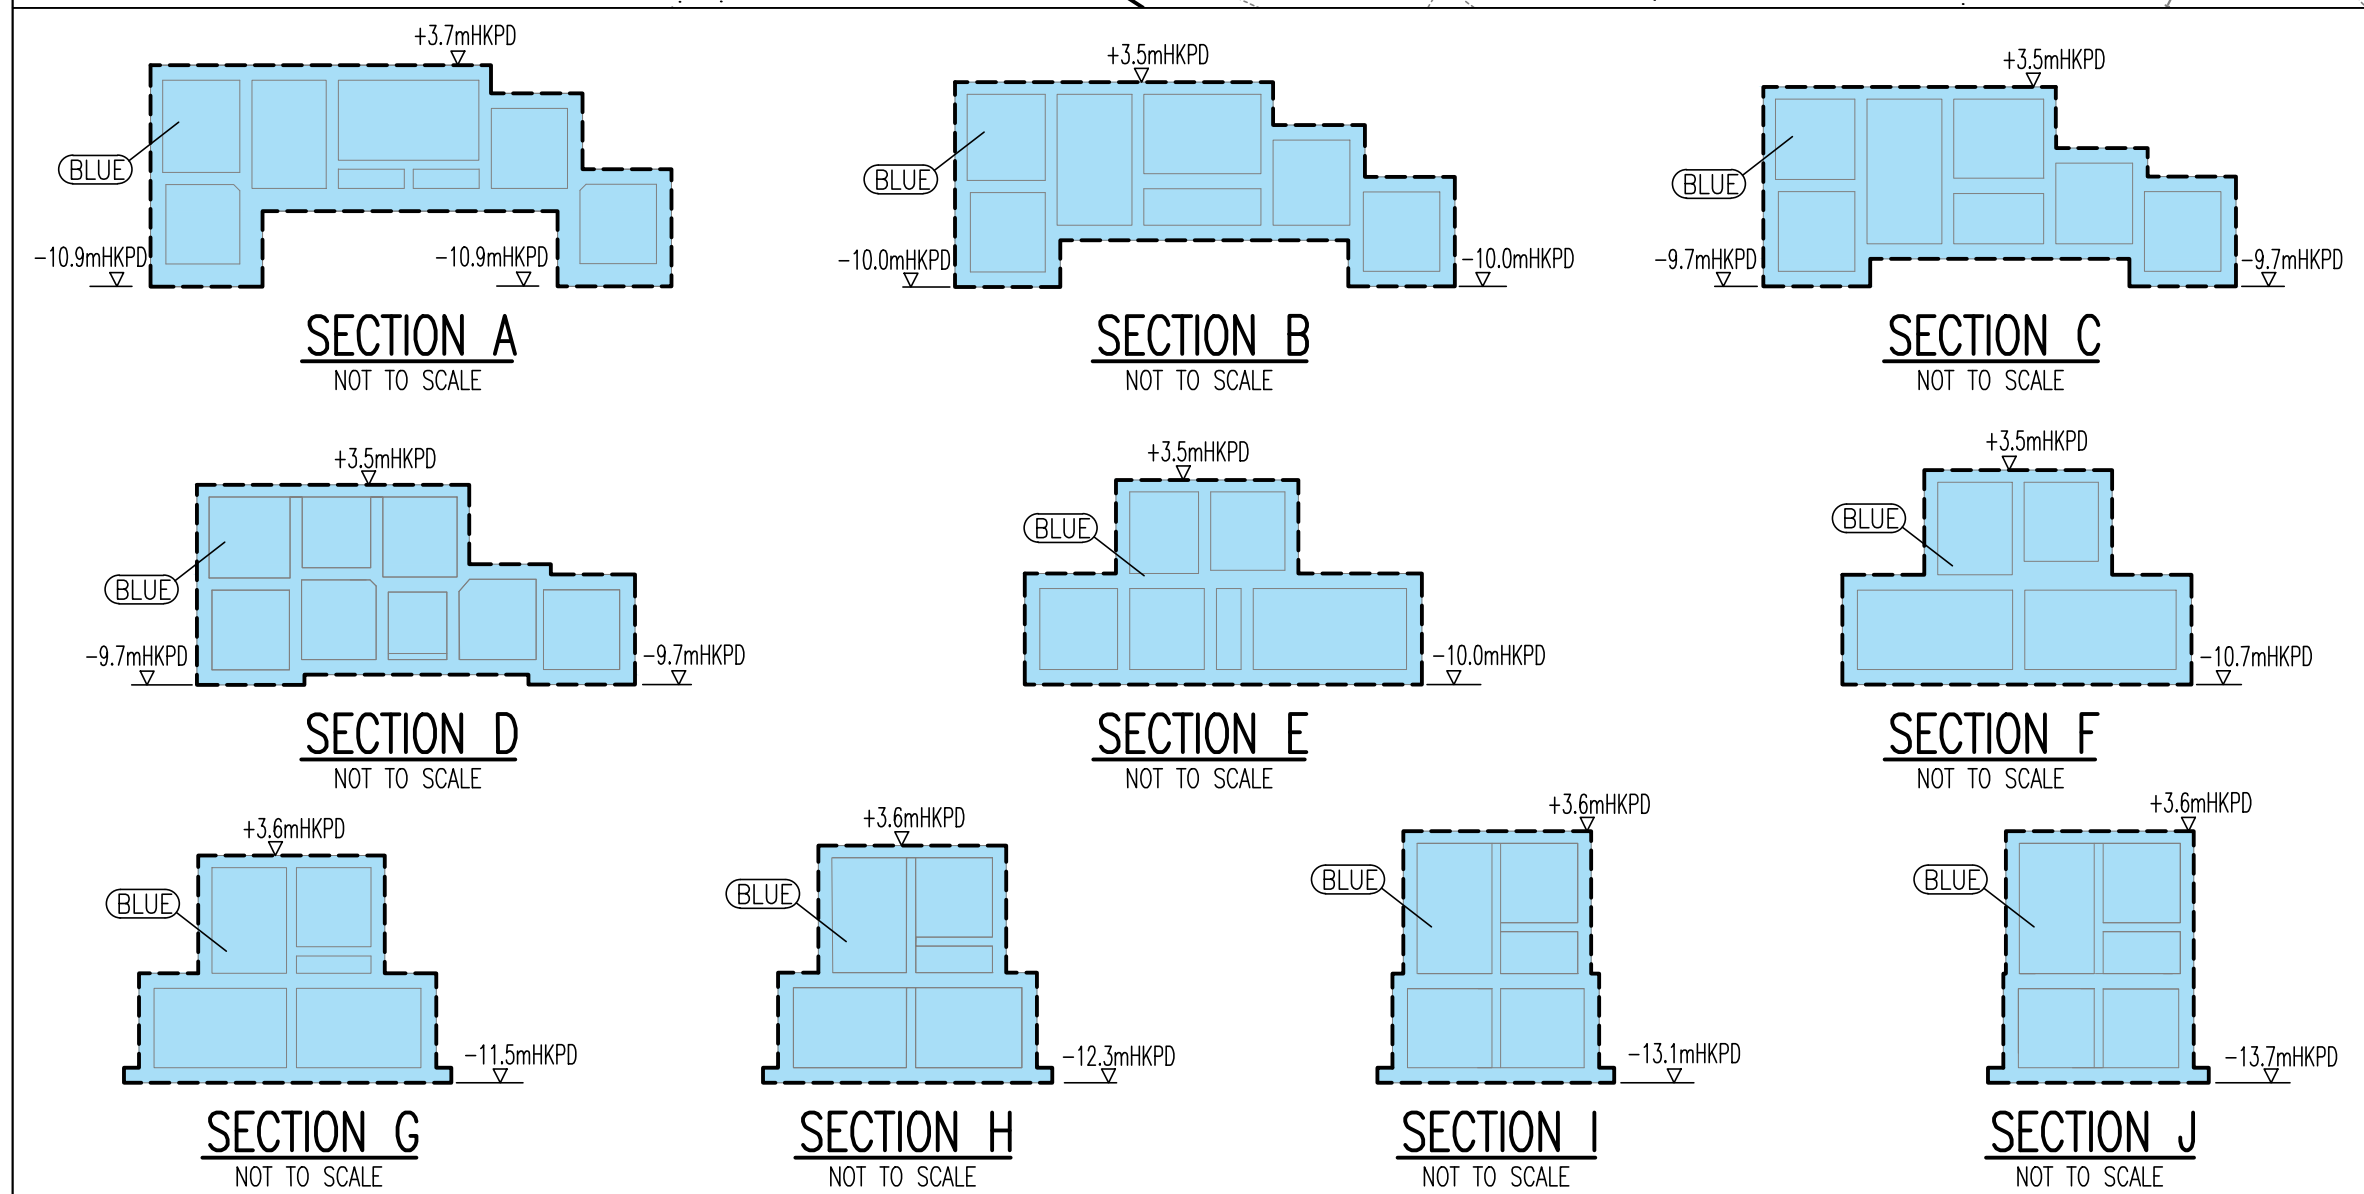

LAND MARKER (1980) H.K. Co., LTD.
標註測量(1980)香港有限公司

Survey District : KOWLOON
Survey Sheet : 11-NW-23D & 24C, 11-SW-3B & 4A
Plan No.: 4192-EA10

KOWLOON INLAND LOT No. 11260 EXCLUDED AREAS FOR MTR LOT No. 2 RP

SIGNED BY

JOSEPH Y C WONG
AUTHORIZED LAND SURVEYOR FHKIS MRICS RPS(LS)

Date: 6 DECEMBER 2019