



The Corporate Seal of the Grantee is affixed by authority of the Board of the Grantee and authenticated by the following members of the Board of the Grantee authorised by the Board:


Member of the Board of the Grantee

Member of the Board of the Grantee

Witness to the signature of  
District Lands Officer, Kowloon West

Civil Servant,  
Lands Department


District Lands Officer,  
Kowloon West

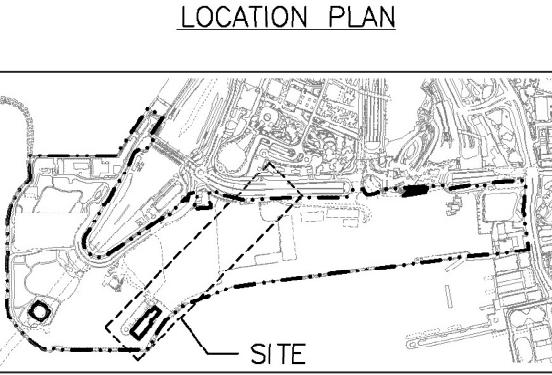

(NOT TO SCALE)


LEGEND

- BOUNDARY OF KIL 11260
- OUTLINE OF FEATURE
- PIPES/CABLES } EXCLUDED AREA
- LAND STRATA
- mHKPD HONG KONG PRINCIPAL DATUM (APPROXIMATE IN METRE)
- TL TOP LEVEL (APPROXIMATE IN mHKPD)
- BL BOTTOM LEVEL (APPROXIMATE IN mHKPD)
- Ø DIAMETER OF PIPE / CABLE

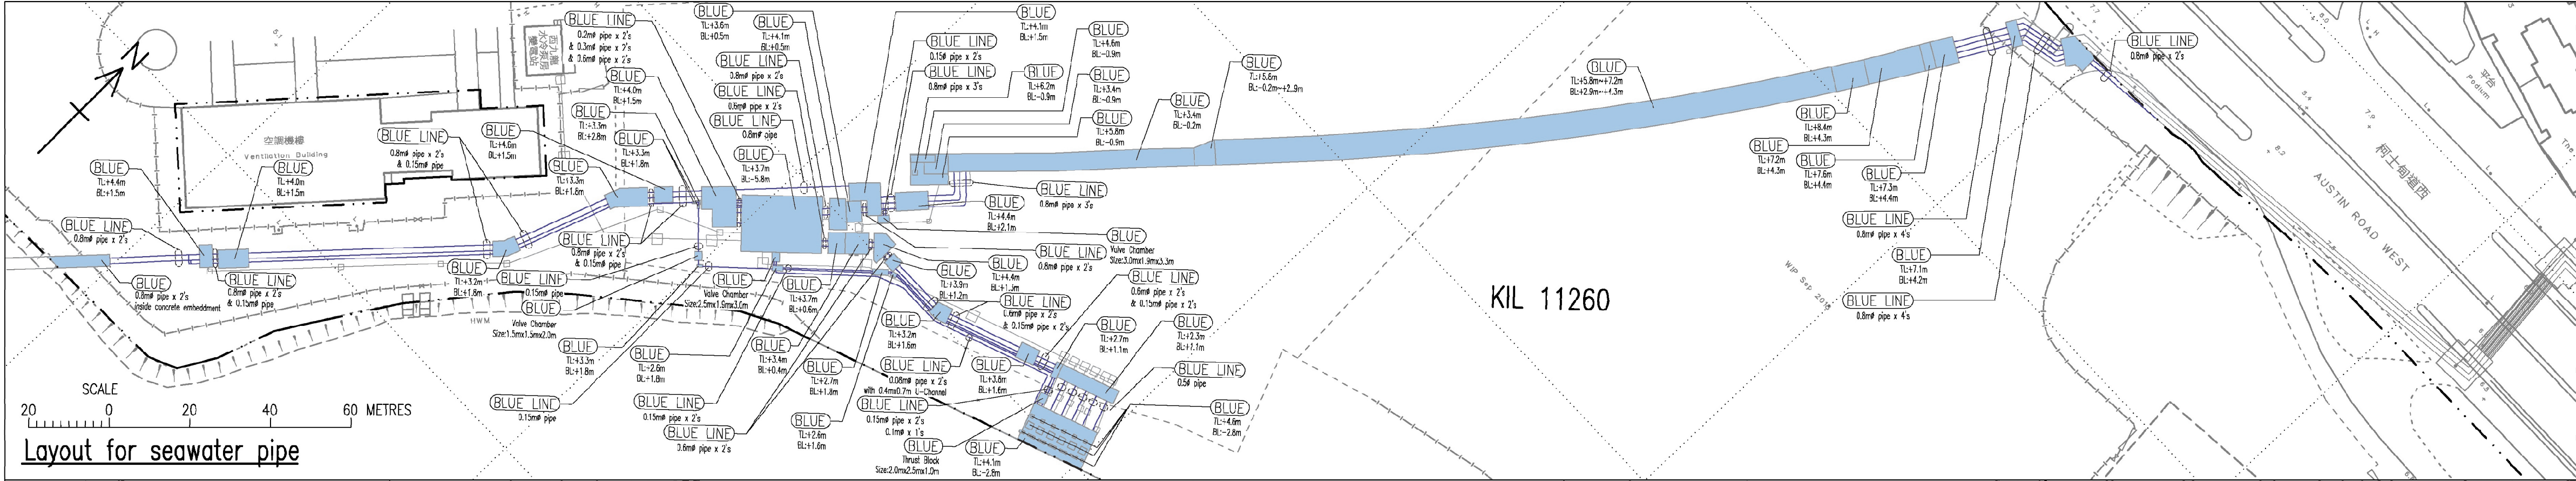

SCALE  
20 0 20 40 60 METRES

Layout for seawater pipe

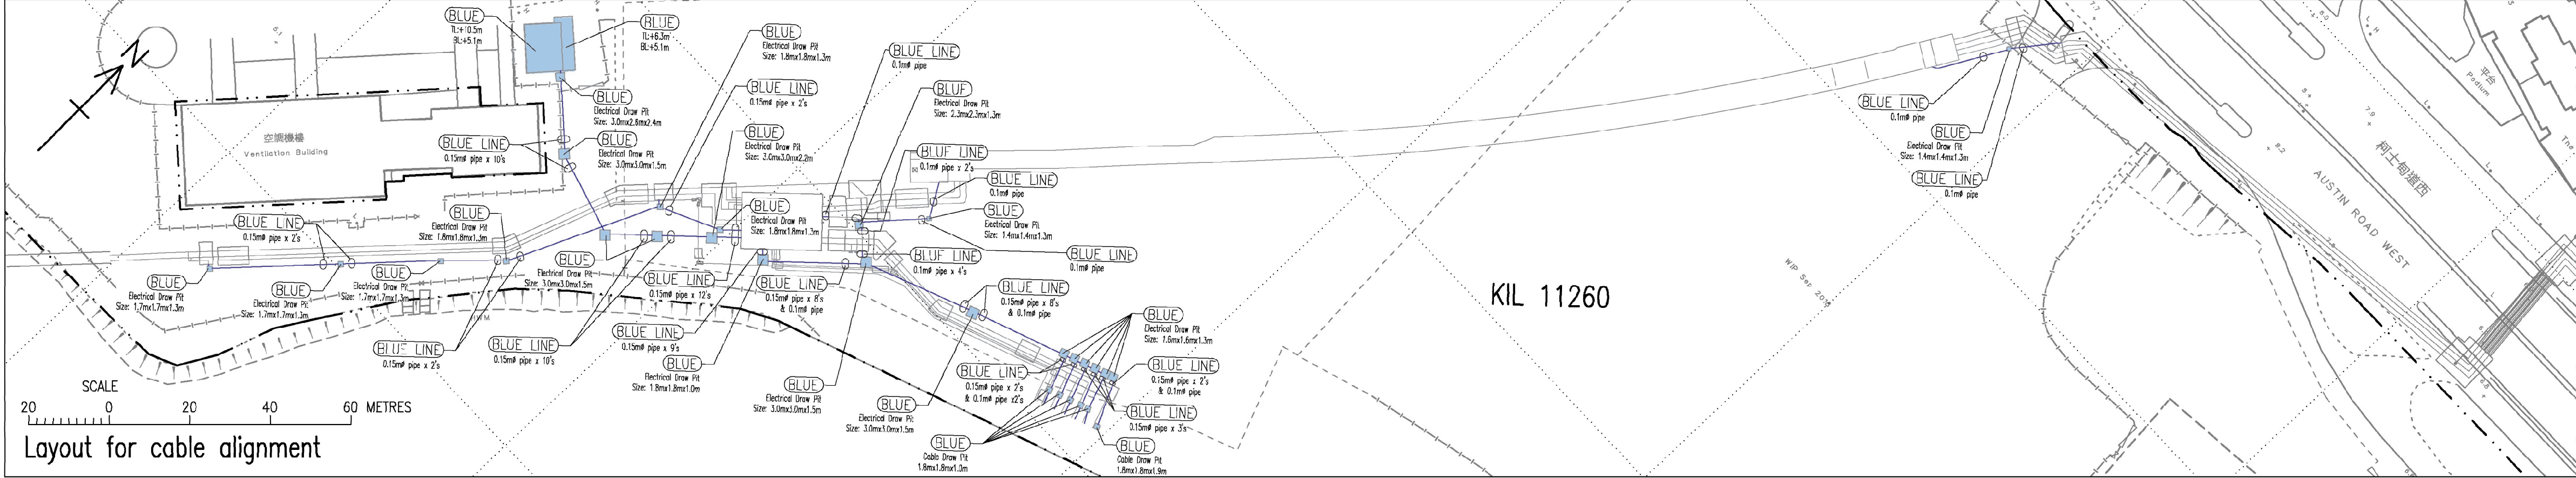

SCALE  
20 0 20 40 60 METRES

Layout for cable alignment

FOR IDENTIFICATION PURPOSES ONLY

District Lands Office, Kowloon West  
Lands Department

Plan Prepared by District Survey Office, Kowloon

© Copyright reserved - Hong Kong SAR Government

KOWLOON INLAND LOT No. 11260  
EXCLUDED AREA FOR PUMP AND COOLING MAINS

File No. DSO/K 031/2015  
Survey Sheet No. 11-NW-23D, 11-SW-3B  
Layout Plan No. ---  
Reference Plan No. 4192-EA11 (06 DEC 2019)  
PLAN No. KL6646-EA11

Date :23/01/2020

Dated this \_\_\_\_ day of \_\_\_\_\_ 20\_\_