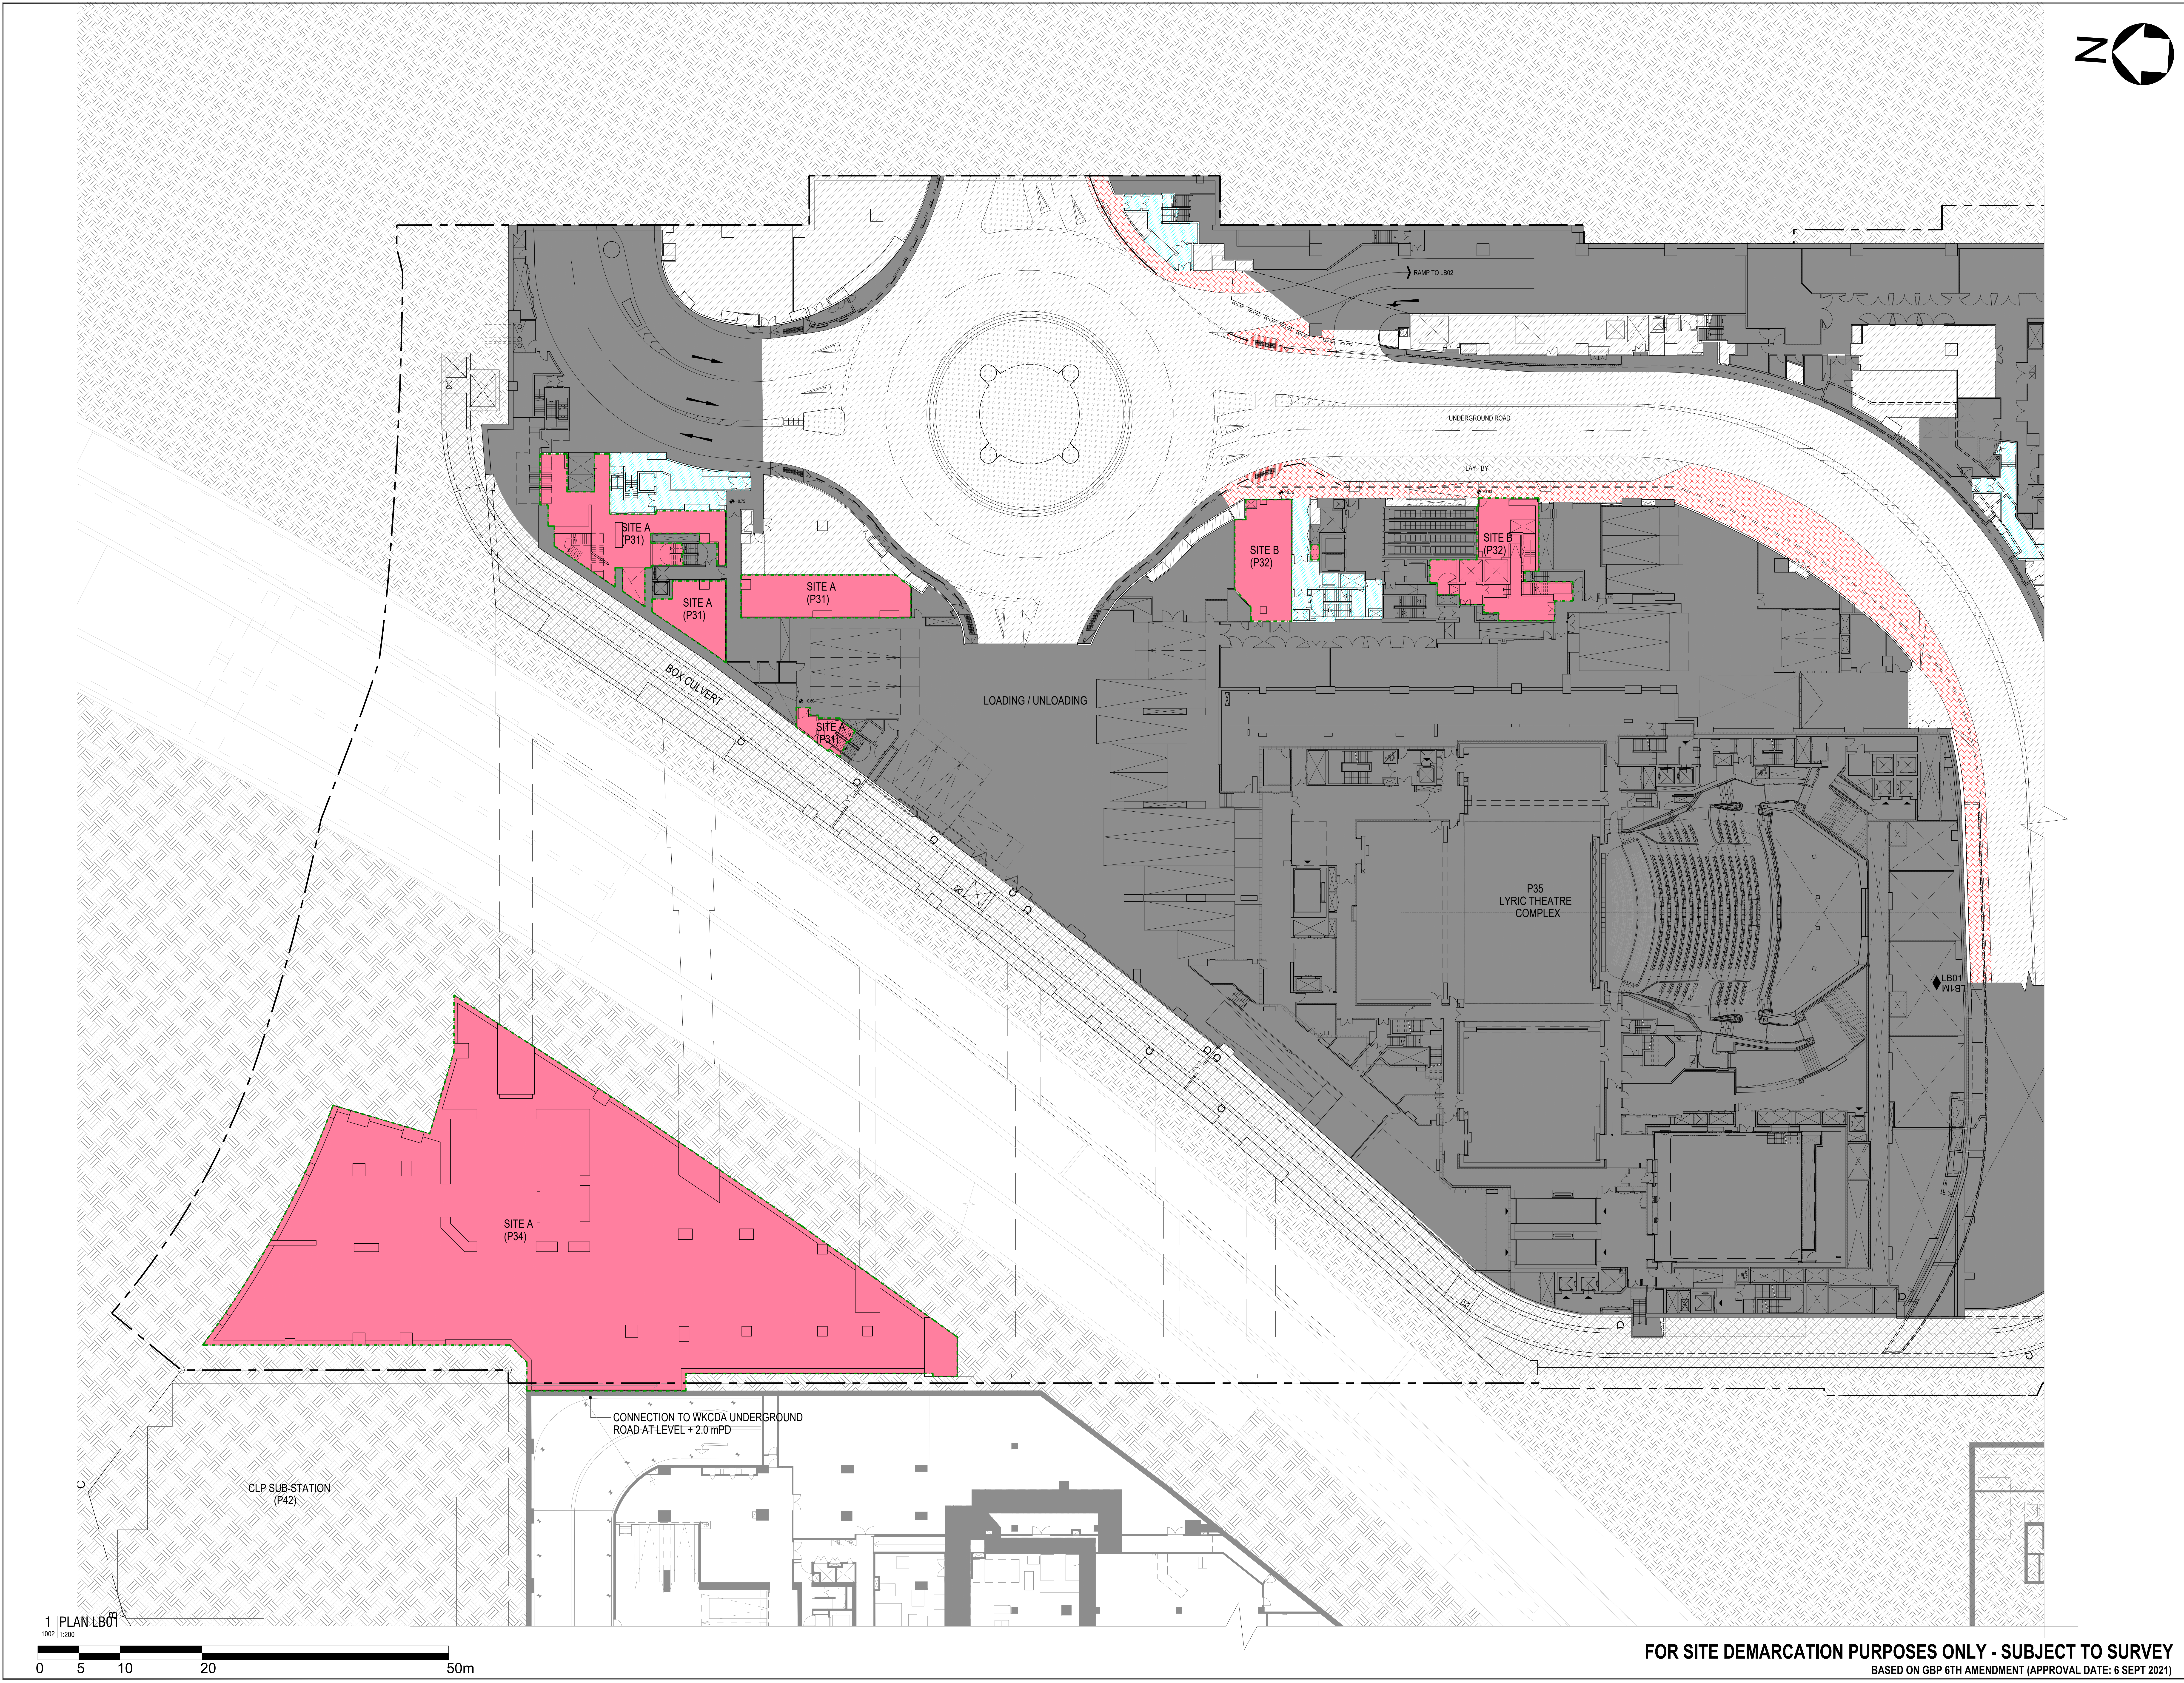

1 PLAN LB01
1002 1:200

FOR SITE DEMARCATION PURPOSES ONLY - SUBJECT TO SURVEY

BASED ON GBP 6TH AMENDMENT (APPROVAL DATE: 6 SEPT 2021)

B.D. REF: 4031/14
F.S.D. REF: FP8 /27927 (G)

KEY PLAN

NOTES:

LEGEND:

▬ ▪ ▬	ZONE 3B BOUNDARY
▨	UR CARRIAGEWAY (GAZETTE)
▨	UR FOOTPATH (GAZETTE)
▨	UR PICK - UP DROP - OFF AREA (GAZETTE)
▨	PEDESTRIAN CROSSING (GAZETTE)
▨	CENTRAL MEDIAN / TRAFFIC ISLAND (GAZETTE)
▨	UR ASSOCIATED PLANT ROOMS / SHAFTS
▨	UR ASSOCIATED MOA / MOE
■	OTHER PREMISES AS IDENTIFIED
▨	UNDER GOVERNMENT MANAGEMENT
▨	EVA
▨	ANCILLARY WORKS AREAS
🟥	SUB-LEASE SITE AREA
▬ ▪ ▬	SUB-LEASE SITE BOUNDARY
▬ ▪ ▬	DEVELOPMENT SITE BOUNDARY
▬	SUB-ZONE BOUNDARY

REV.	DATE		
XD	19.01.2023	GENERAL UPDATE	ADR
XC	25.05.2022	UPDATE AS PER GBP	ADR
XB	23.11.2021	GENERAL UPDATE	ADR
LEAD CONSULTANT		PURPOSE OF RELEASE	PRODUCED BY

UNLESS NOTED OTHERWISE, COPYRIGHT AND DESIGN RIGHTS IN THIS DOCUMENT ARE OWNED BY ONE OR ALL OF THE MEMBERS OF THE UN STUDIO AND AD+RG JOINT VENTURE (UAJV) FORMING THE "CONSULTANT". WITHOUT DEROGATION TO ANY PROVISION OF THE CONSULTANCY AGREEMENT, THE CONSULTANT, RESPECTIVELY THE MEMBER OF THE UAJV THAT OWNS SUCH INTELLECTUAL PROPERTY, HAS GRANTED AND GRANTS ONLY TO THE AUTHORITY, ITS SUCCESSORS AND ASSIGNS A PERPETUAL, UNRESTRICTED, EXCLUSIVE, FREELY ASSIGNABLE AND IRREVOCABLE WORLD-WIDE LICENCE (CARRYING THE RIGHT TO GRANT SUB LICENCES) TO USE, REPRODUCE, MODIFY, ADAPT AND TRANSLATE THE INTELLECTUAL PROPERTY IN THIS DOCUMENT FOR ANY PURPOSE OF THE AUTHORITY. NOTWITHSTANDING THE ABOVE MENTIONED LICENCE, THIS DOCUMENT SHALL BE MODIFIED ADAPTED OR TRANSLATED ONLY BY THE MEMBER OF UAJV INDICATED AS HAVING PRODUCED THIS DOCUMENT. THE USE OF THIS DOCUMENT AND THE INTELLECTUAL PROPERTY VESTED THEREIN BY ANY OTHER PARTY THAN THOSE MENTIONED ABOVE MUST BE SUBJECT TO AN AGREEMENT OR AUTHORISATION BY OR WITH THE AUTHORITY.

UNSTUDIO / AD+RG

LEAD ARCHITECTURAL DESIGNER

UNSTUDIO
Room 4606, Raffles City, 268 Xizang Middle Road,
Shanghai 200001, China

LEAD ARCHITECTURAL CONSULTANT

AD+RG
10/F, 111 Leighton Road,Causeway
Bay, Hong Kong

UAJV SUBCONSULTANT

AECOM
8/F, Grand Central Plaza, Tower2,
138 Shatin Rural Committee Road
Shatin,
Hong Kong

WSP
29/F, AIA Kowloon Tower,
Landmark East, 100 How Ming Street
Kwun Tong, Kowloon
Hong Kong

THE SPACE FACTORY
5 Rue Pizay
Lyon,
France

MARSHALL DAY Acoustics
Suite 1201, Tower 2, The Gateway,
25 Canton Road
Tsimshatsui,
Hong Kong

MVA SYSTRA GROUP
14th Floor West, Warwick House,
Taikoo Place, 979King's Road
Island East,
Hong Kong

AUTHORITY'S CONSULTANT
QUANTITY SURVEYOR

WT PARTNERSHIP
Address: 20/F/ 625 King's Road,
North Point, Hong Kong

JOB TITLE

ARTIST SQUARE TOWERS
(P31 / P34 AND P32)
HOR PROJECT

DRAWING TITLE

DEVELOPMENT SITE PLAN LB01

SCALE	1:250	PRINTED	A0
CHECKED	SKH	DATE	19/01/2023
APPROVED	BL	DATE	19/01/2023
PRODUCED BY	UAJV	DATE	19/01/2023

AUTHOR UAJV

DISCIPLINE ARC

PHASE TENDER

DRAWING NO. 3AAST-ADR-AAC-DWG-1002-P00-LB01-WS3
REV. XD

CAD REF NAME: 3AAST-ADR-AAC-DWG-1002-P00-LB01-WS3-XD

AUTHORITY

westKowloon
西九文化區