
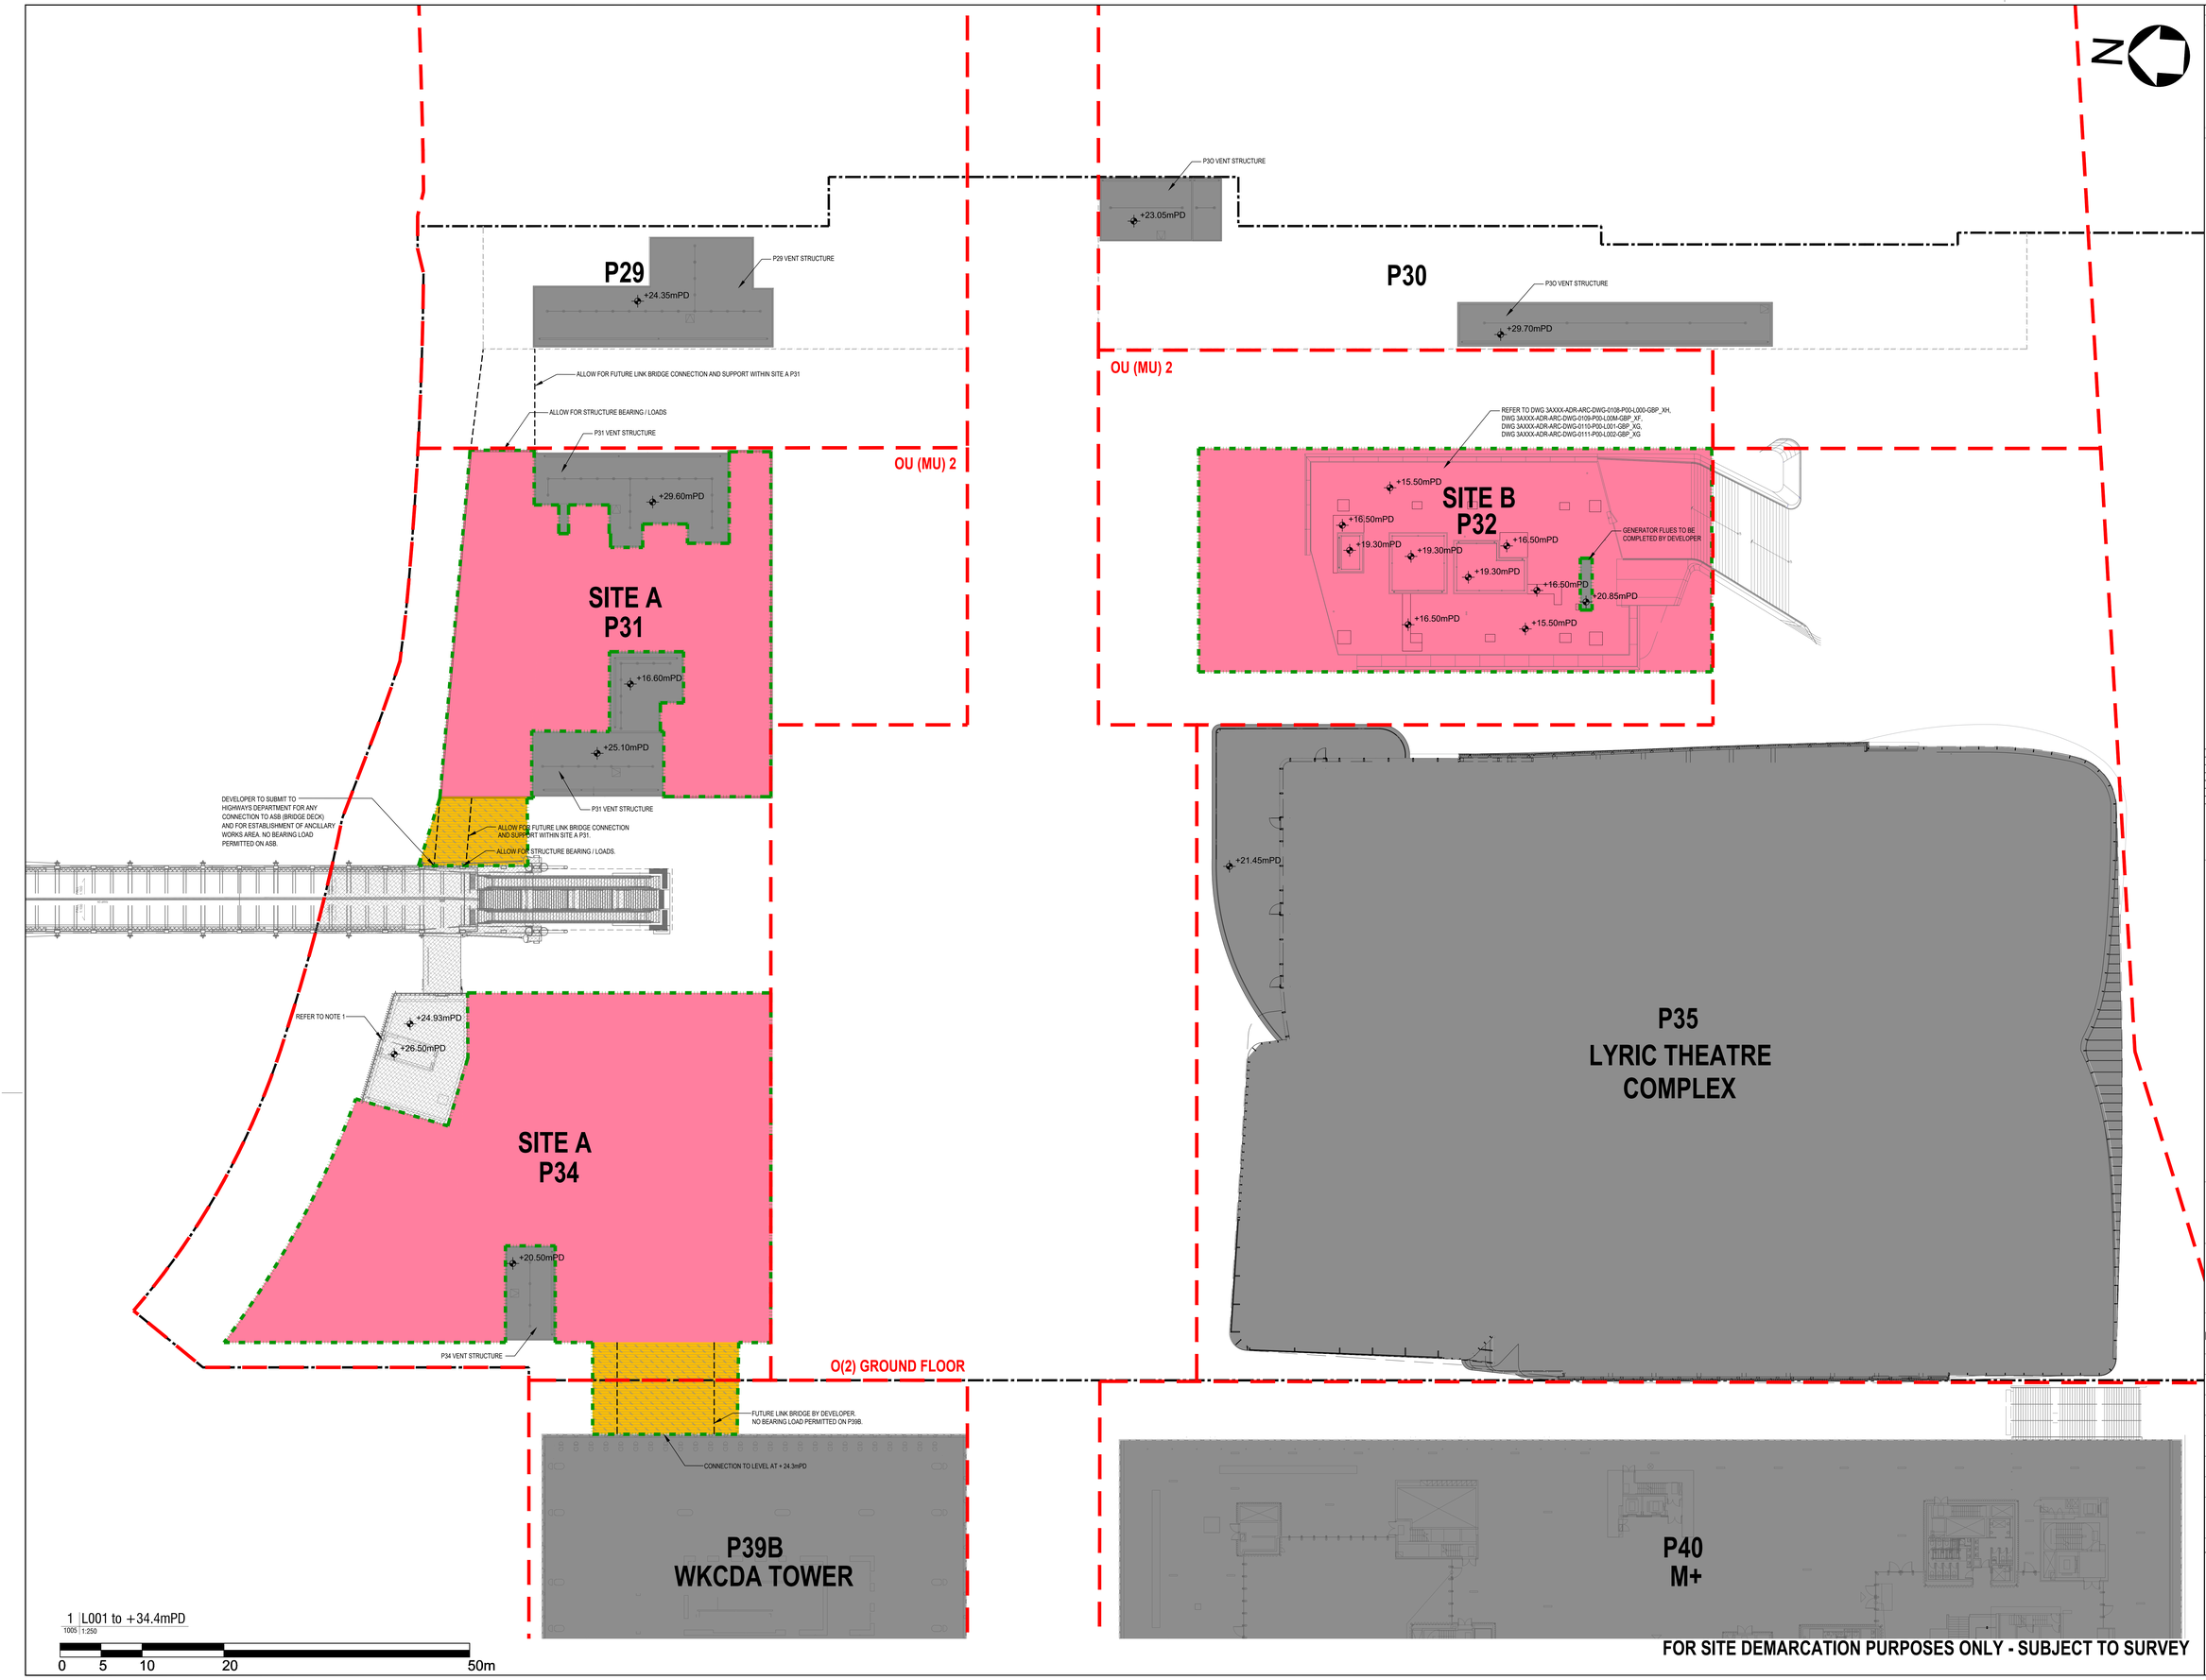


B.D. REF: 4031/14
F.S.D. REF: FP8 /27927 (G)

KEY PLAN

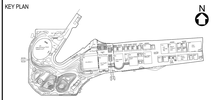

KEY PLAN

NOTES:

LEGEND:

- ZONE 3B BOUNDARY
- UR CARRIAGEWAY (GAZETTE)
- UR FOOTPATH (GAZETTE)
- UR PICK - UP DROP - OFF AREA (GAZETTE)
- PEDESTRIAN CROSSING (GAZETTE)
- CENTRAL MEDIAN / TRAFFIC ISLAND (GAZETTE)
- UR ASSOCIATED PLANT ROOMS / SHAFTS
- UR ASSOCIATED MOA / MOE
- OTHER PREMISES AS IDENTIFIED
- UNDER GOVERNMENT MANAGEMENT
- EVA
- ANCILLARY WORKS AREAS
- SUB-LEASE SITE AREA
- SUB-LEASE SITE BOUNDARY
- DEVELOPMENT SITE BOUNDARY
- SUB-ZONE BOUNDARY

NOTE 1 SUB-LEASE EXTENDS OVER THE ASB LIFT / STAIR TOWER.

REV.	DATE	PURPOSE OF RELEASE	PRODUCED BY
XD	14.01.2022	LEVEL UPDATE	ADR
XC	23.11.2021	GENERAL UPDATE	ADR
XB	17.11.2021	COORDINATES UPDATE	ADR
REV.	DATE	PURPOSE OF RELEASE	PRODUCED BY

LEAD CONSULTANT

UNLESS NOTED OTHERWISE, COPYRIGHT AND DESIGN RIGHTS IN THIS DOCUMENT ARE OWNED BY (1)ALL OF THE MEMBERS OF THE UN STUDIO AND SCHU LIGHT STUDIO (ULX) FORMING THE "CONSULTANT" WITHOUT DEROGATION TO ANY PROVISION OF THE CONSULTANCY AGREEMENT, THE CONSULTANT, RESPECTIVELY THE MEMBER OF THE ULX THAT OWNS SUCH INTELLECTUAL PROPERTY, HAS GRANTED AND GRANTS ONLY TO THE AUTHORITY, ITS SUCCESSORS AND ASSIGNS A PERPETUAL, UNRESTRICTED, EXCLUSIVE, FREE, IRREVOCABLE AND WORLDWIDE LICENCE (CARRYING THE RIGHT TO GRANT SUB-LICENCES) TO USE, REPRODUCE, MODIFY, ADAPT AND TRANSLATE THE INTELLECTUAL PROPERTY IN THIS DOCUMENT FOR ANY PURPOSE OF THE AUTHORITY. NOTWITHSTANDING THE ABOVE MENTIONED LICENCE, THIS DOCUMENT SHALL BE MODIFIED ADAPTED OR TRANSLATED ONLY WITH THE PRIOR WRITTEN CONSENT OF THE CONSULTANT. ANY USE OF THIS DOCUMENT AND THE INTELLECTUAL PROPERTY VESTED THEREIN BY ANY OTHER PARTY THAN THOSE MENTIONED ABOVE MUST BE SUBJECT TO AN AGREEMENT OR AUTHORISATION BY OR WITH THE AUTHORITY.

UNSTUDIO / AD+RG

LEAD ARCHITECTURAL DESIGNER

UNSTUDIO
Room 4606, Raffles City, 268 Xizang Middle Road, Shanghai 200001, China

LEAD ARCHITECTURAL CONSULTANT

AD+RG
10/F., 111 Leighton Road,Causeway Bay, Hong Kong

UAJV SUBCONSULTANT

AECOM
8/F, Grand Central Plaza, Tower2, 138 Shatin Rural Committee Road — Shatin, Hong Kong

WSP
29/F, AIA Kowloon Tower, Landmark East, 100 How Ming Street — Kwun Tong, Kowloon Hong Kong

THE SPACE FACTORY
3 Rue Pizay — Lyon, France

MARSHALL DAY Acoustics
Suite 1201, Tower 2, The Gateway, 25 Canton Road — Tsimshatsui, Hong Kong

MVA
14th Floor West, Warwick House, Taikoo Place, 979King's Road — Island East, Hong Kong

AUTHORITY'S CONSULTANT

QUANTITY SURVEYOR

WT PARTNERSHIP
Address: 20/F/ 625 King's Road, North Point, Hong Kong

JOB TITLE

ARTIST SQUARE TOWERS
(P31 / P34 AND P32)
HOR PROJECT

DRAWING TITLE

DEVELOPMENT SITE PLAN L001 to +34.4mPD

SCALE	1:250	PRINTED	A0
CHECKED	SKH / JT	DATE	11/11/2021
APPROVED	BL	DATE	11/11/2021
PRODUCED BY	UAJV	DATE	11/11/2021
AUTHOR			UAJV
DISCIPLINE			ARC
PHASE			TENDER
DRAWING NO.			REV.
3AAST-ADR-AAC-DWG-1005-P00-L001-WS3			XD
CAD REF NAME:			3AAST-ADR-AAC-DWG-1005-P00-L001-WS3-XD

AUTHORITY

westKowloon
西九文化區