

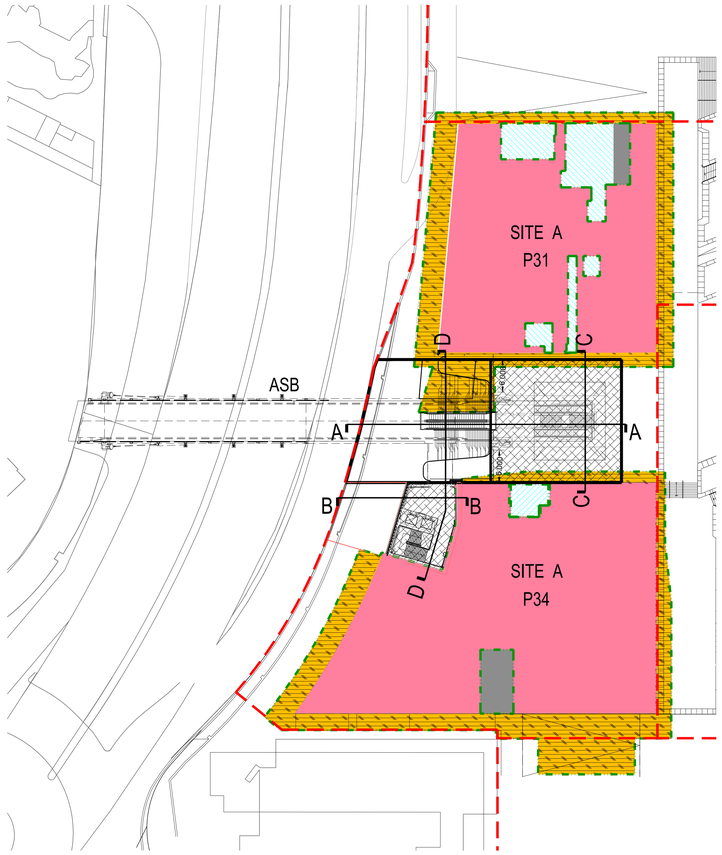



PLAN - 1 @+11.55mPD
SCALE 1:400

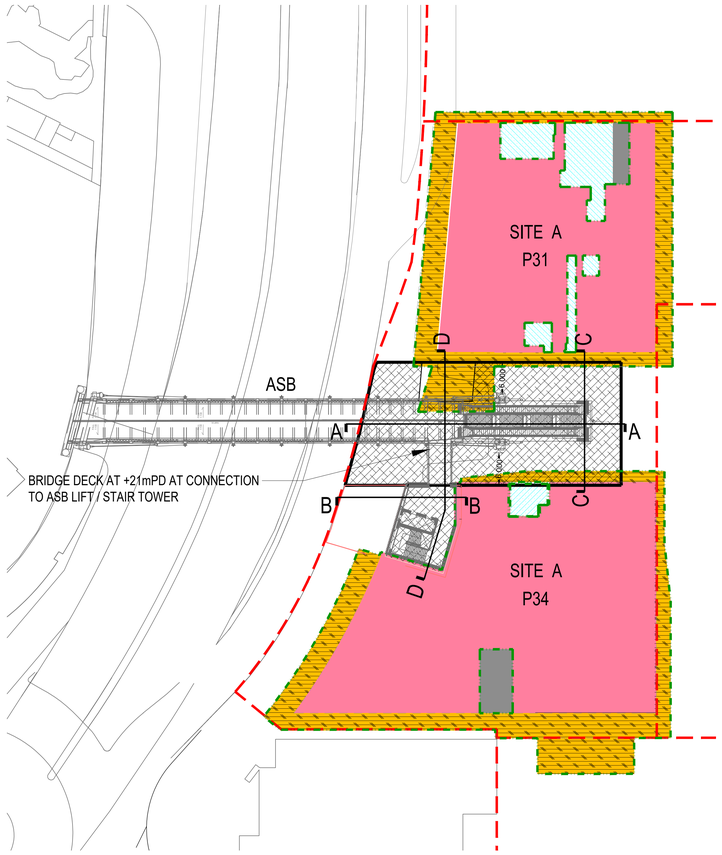


PLAN - 2 @+28.70mPD
SCALE 1:400

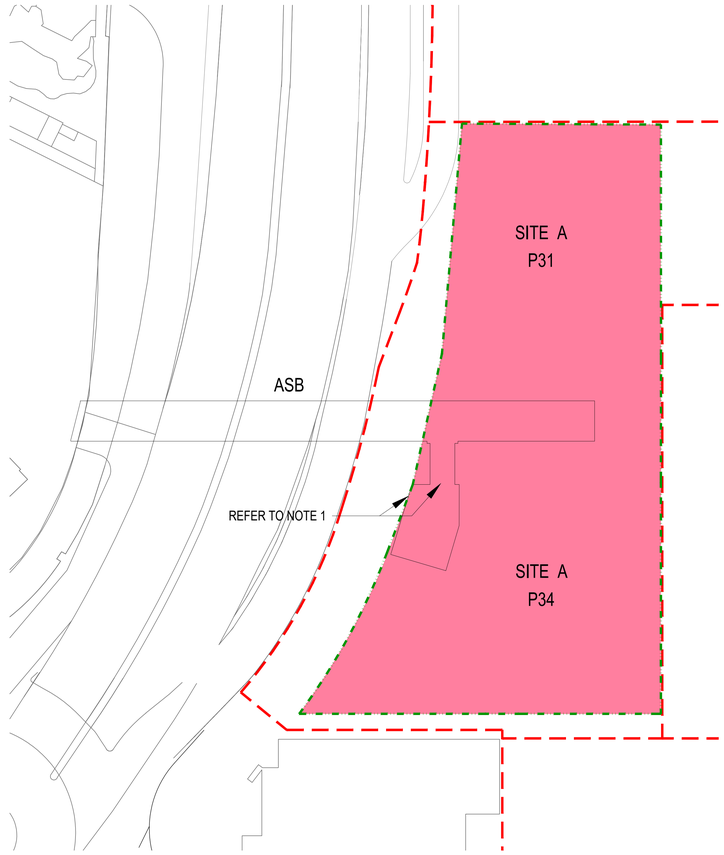


PLAN - 3 @+34.4mPD
SCALE 1:400

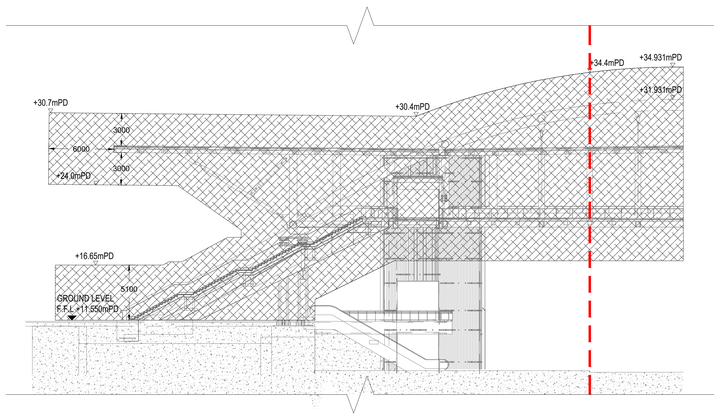


SECTION A
SCALE 1:200

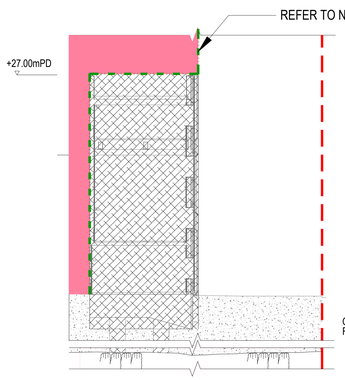

SECTION B
SCALE 1:200

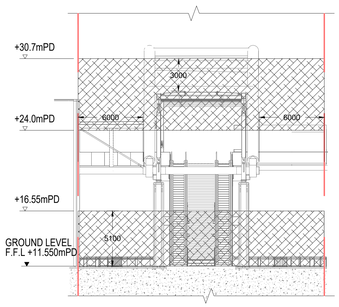

SECTION C
SCALE 1:200

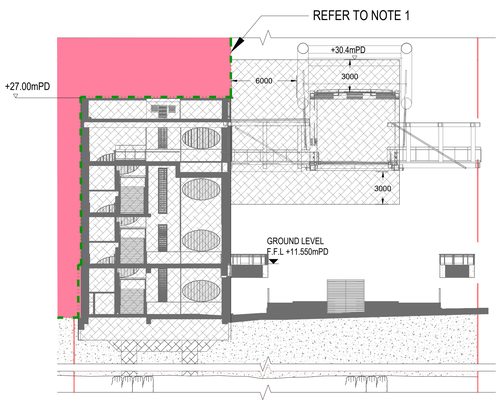


SECTION D
SCALE 1:200

FOR SITE DEMARCATION PURPOSES ONLY - SUBJECT TO SURVEY

B.D. REF: 4031/14
F.S.D. REF: FP8 /27927 (G)

KEY PLAN

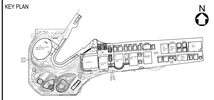

KEY PLAN

NOTES:

LEGEND:

- ZONE 3B BOUNDARY
- UR CARRIAGEWAY (GAZETTE)
- UR FOOTPATH (GAZETTE)
- UR PICK - UP DROP - OFF AREA (GAZETTE)
- PEDESTRIAN CROSSING (GAZETTE)
- CENTRAL MEDIAN / TRAFFIC ISLAND (GAZETTE)
- UR ASSOCIATED PLANT ROOMS / SHAFTS
- UR ASSOCIATED MOA / MOE
- OTHER PREMISES AS IDENTIFIED
- UNDER GOVERNMENT MANAGEMENT
- EVA
- ANCILLARY WORKS AREAS
- SUB-LEASE SITE AREA
- SUB-LEASE SITE BOUNDARY
- DEVELOPMENT SITE BOUNDARY
- SUB-ZONE BOUNDARY

NOTE 1 DEVELOPER'S TOPSIDE TO EXTEND OVER ROOF OF ASB LIFT / STAIR TOWER AND ALIGN AT BOUNDARY WITH ASB FAÇADE.

REV.	DATE	PURPOSE OF RELEASE	PRODUCED BY
XD	19.01.2023	GENERAL UPDATE	ADR
XC	23.11.2021	GENERAL UPDATE	ADR
XB	17.11.2021	COORDINATES UPDATE	ADR
LEAD CONSULTANT			

UNLESS NOTED OTHERWISE, COPYRIGHT AND DESIGN RIGHTS IN THIS DOCUMENT ARE OWNED BY (THE OR ALL OF THE MEMBERS OF THE UNSTUDIO AND AD+RG JOINT VENTURE ("UAJV") AND MAY NOT BE USED WITHOUT THE PRIOR WRITTEN CONSENT OF THE UAJV. IN THE CONSULTANCY AGREEMENT, THE CONSULTANT, IRRESPECTIVE OF WHETHER A MEMBER OF THE UAJV THAT OWNS SUCH INTELLECTUAL PROPERTY, HAS GRANTED AND GRANTS ONLY TO THE AUTHORITY, ITS SUCCESSORS AND ASSIGNS A PERPETUAL, UNRESTRICTED, EXCLUSIVE, FREE, ASSIGNABLE AND SUB-LICENSABLE LICENCE TO USE, COPY, REPRODUCE, MODIFY, ADAPT, TRANSLATE AND DEVELOP, AND TO AUTHORISE OTHERS TO USE, COPY, REPRODUCE, MODIFY, ADAPT AND TRANSLATE THE INTELLECTUAL PROPERTY IN THIS DOCUMENT FOR ANY PURPOSE OF THE AUTHORITY. NOTWITHSTANDING THE ABOVE MENTIONED LICENCE, THIS DOCUMENT SHALL BE MODIFIED, ADAPTED OR TRANSLATED ONLY BY THE MEMBER OF UAJV INDICATED AS HAVING PRODUCED THIS DOCUMENT. THE USE OF THIS DOCUMENT AND THE INTELLECTUAL PROPERTY VESTED THEREIN BY ANY OTHER PARTY THAN THOSE MENTIONED ABOVE MUST BE SUBJECT TO AN AGREEMENT OR AUTHORISATION BY OR WITH THE AUTHORITY.

UNSTUDIO / AD+RG

LEAD ARCHITECTURAL DESIGNER

UNSTUDIO
Room 4606, Raffles City, 268 Xizang Middle Road, Shanghai 200001, China

LEAD ARCHITECTURAL CONSULTANT

AD+RG
10/F., 111 Leighton Road,Causeway Bay, Hong Kong

UAJV SUBCONSULTANT

AECOM
8/F, Grand Central Plaza, Tower2, 138 Shatin Rural Committee Road — Shatin, Hong Kong

WSP
29/F, AIA Kowloon Tower, Landmark East, 100 How Ming Street — Kwun Tong, Kowloon Hong Kong

THE SPACE FACTORY
5 Rue Pizay — Lyon, France

MARSHALL DAY Acoustics
Suite 1201, Tower 2, The Gateway, 25 Canton Road — Tsimshatsui, Hong Kong

MVA
14th Floor West, Warwick House, Taikoo Place, 979King's Road — Island East, Hong Kong

AUTHORITY'S CONSULTANT

QUANTITY SURVEYOR

WT PARTNERSHIP
Address: 20/F/ 625 King's Road, North Point, Hong Kong

JOB TITLE

THE DESIGN AND CONSTRUCTION OF THE LYRIC THEATRE OF THE WEST KOWLOON CULTURAL DISTRICT

DRAWING TITLE

DEVELOPMENT SITE PLAN ASB AREA

SCALE	AS SHOWN	PRINTED	A0
CHECKED	SKH	DATE	19/01/2023
APPROVED	BL	DATE	19/01/2023
PRODUCED BY	UAJV	DATE	19/01/2023
AUTHOR			UAJV
DISCIPLINE			ARC
PHASE			TENDER
DRAWING NO.			REV.
3AAST-ADR-AAC-DWG-1007-P00-XXXX-WS3			XD
CAD REF NAME:	3AAST-ADR-AAC-DWG-1007-P00-XXXX-WS3-XD		

AUTHORITY

westKowloon
西九文化區