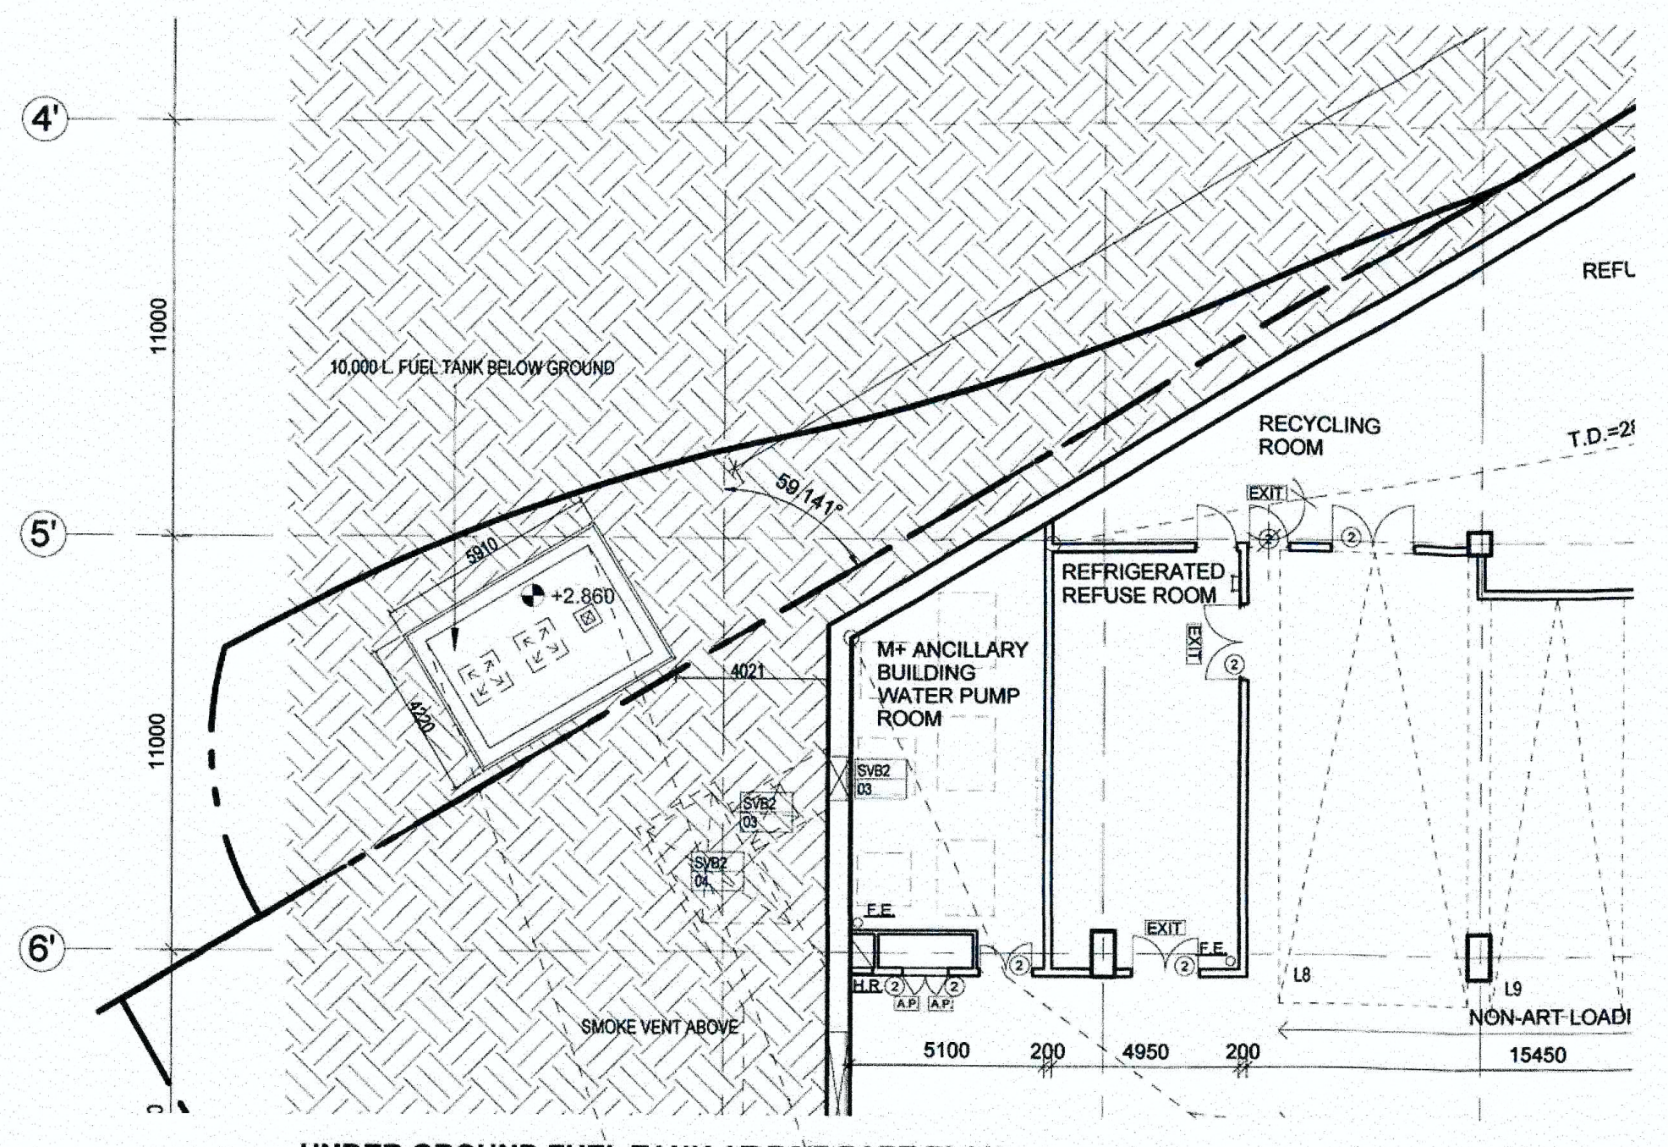

UNDER GROUND FUEL TANK AT B2/F PART PLAN
1 : 200

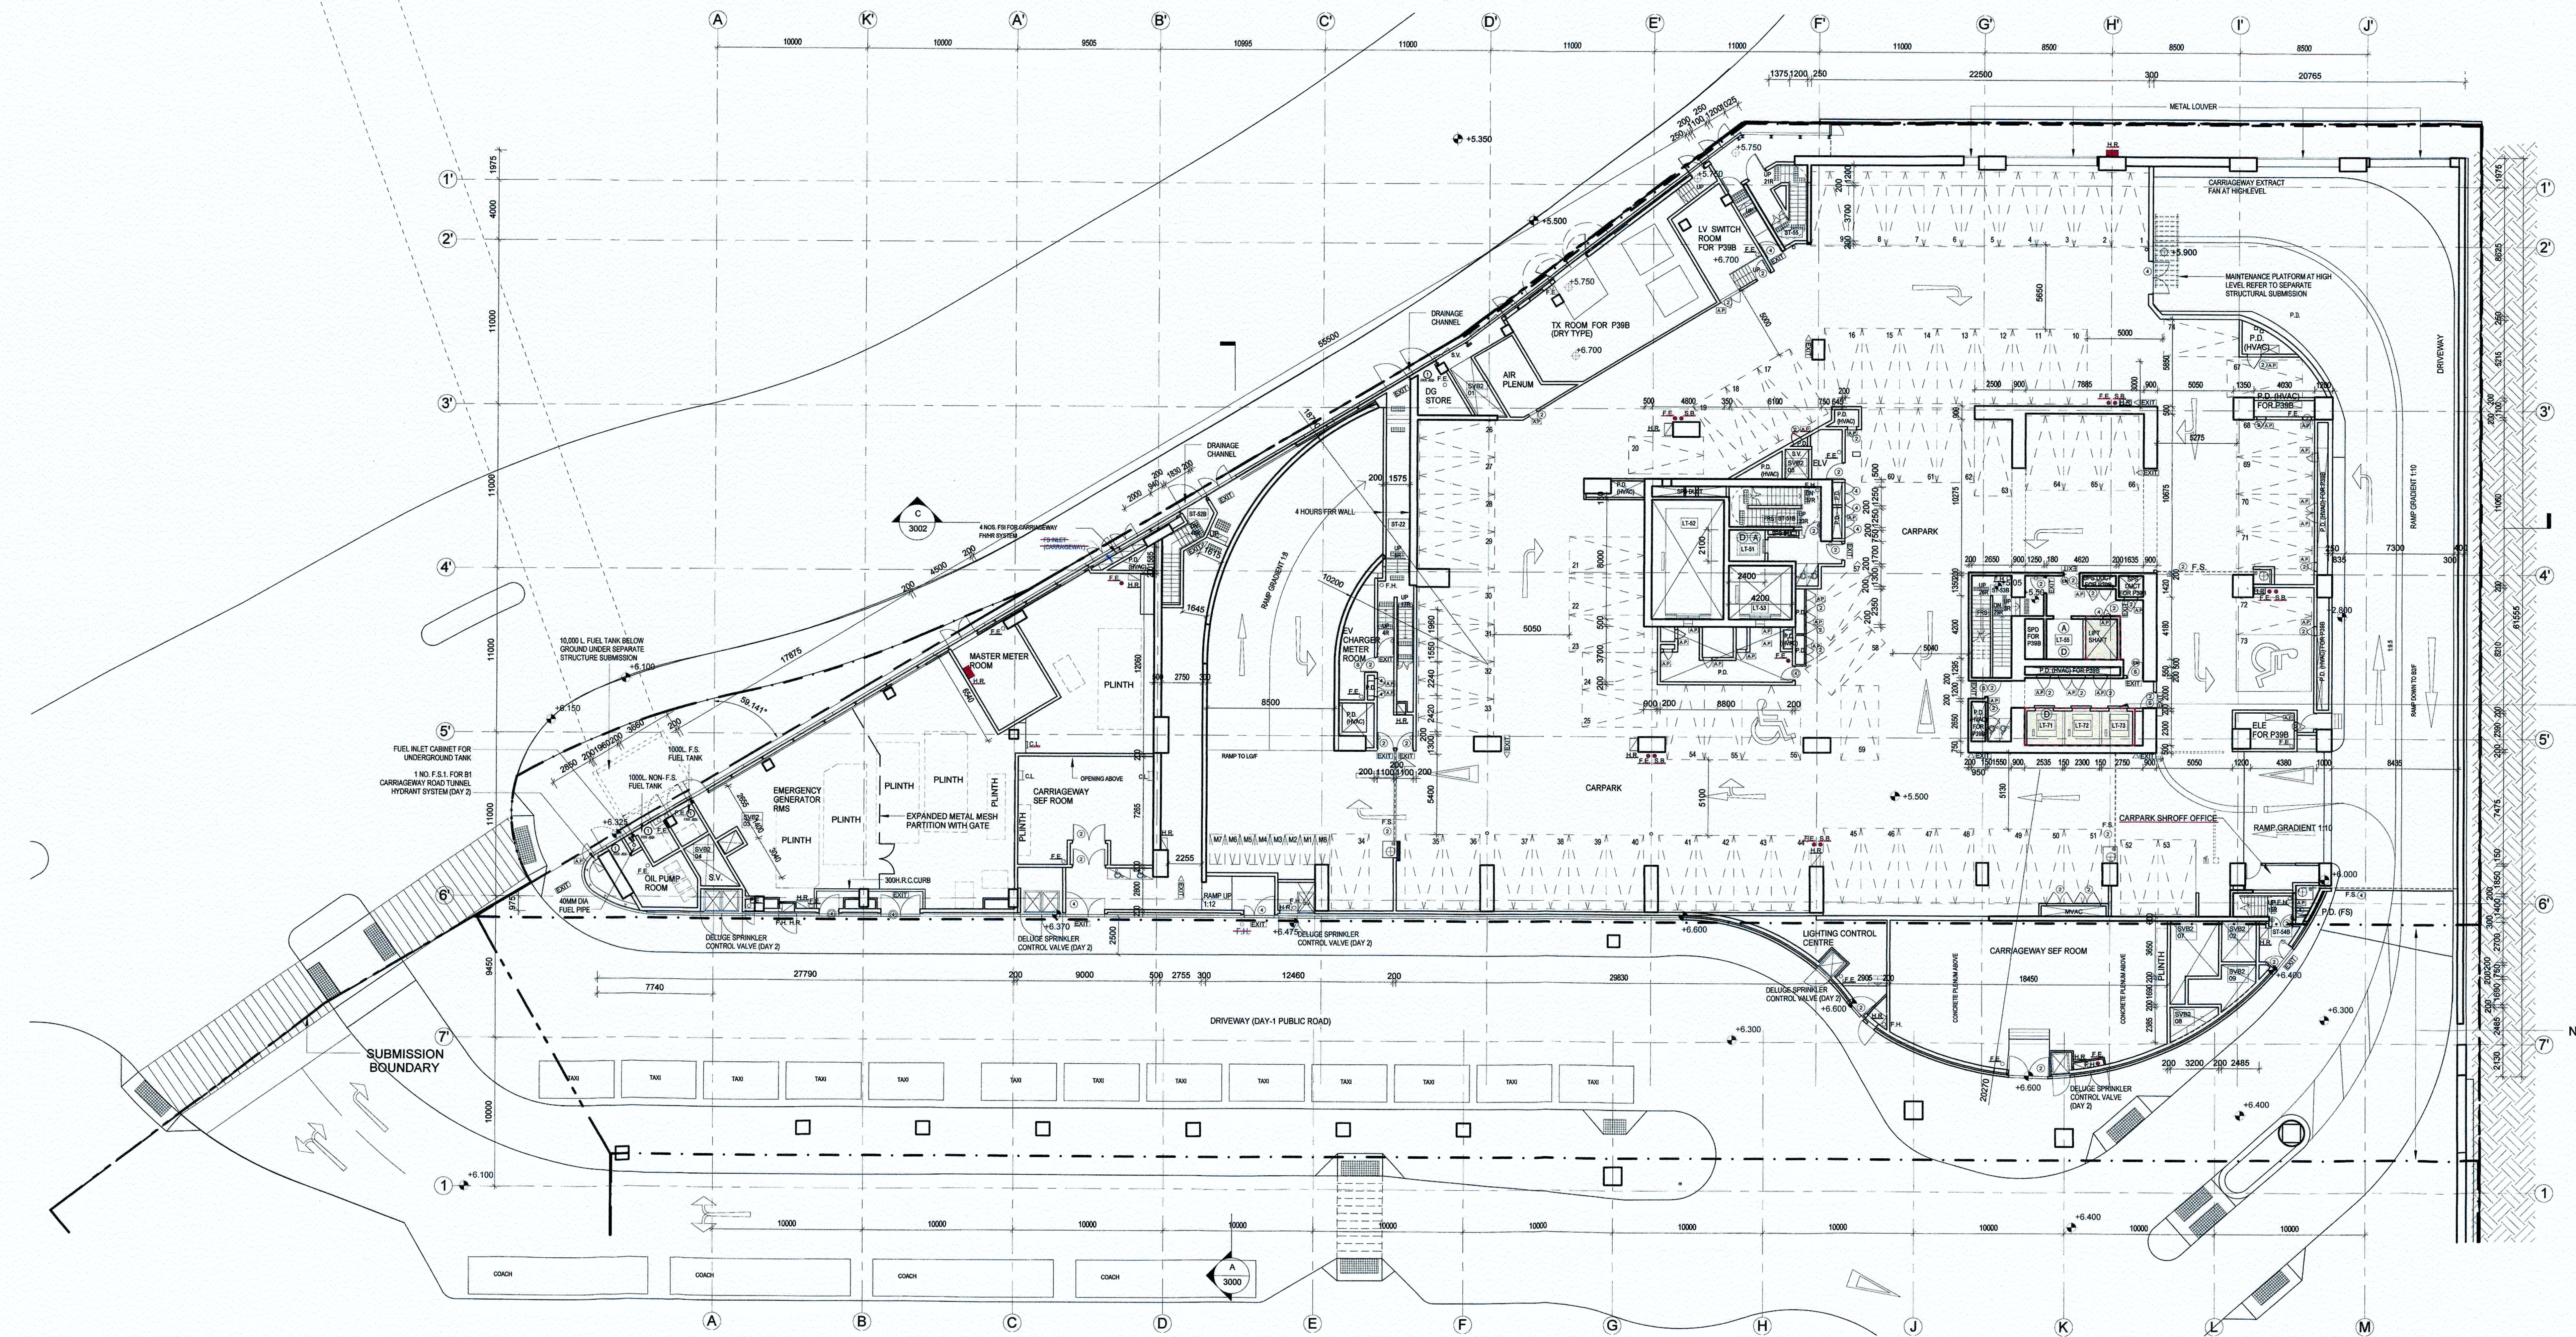

B1/F PLAN (2 OF 2)
1 : 200

NO. OF CARPARK AT B1/F : 74
(IN WHICH 2 NOS. FOR DISABLED)

FRR -/240/240 TEMPORARY SEPARATION TO
BLOCK OUT LT-71, 72 & 73 LIFT OPENING
PHASE 1 OP;
AND TO BE REMOVED FOR PHASE 2 OP
INSPECTION

NO.20 PACKAGE
BOUNDARY

RECEIVED BY
2020 JUN 23 P 5:05
BUILDINGS DEPARTMENT

Note: This plan has been processed on a curtailed check basis under the centralized processing system as promulgated in PNAP ADM-19. The duties of the authorized person, registered structural engineer and/or registered geotechnical engineer concerned as specified under section 4(3)(b) and the provision of section 14(3)(c) of the Buildings Ordinance are of particular relevance in this regard.

LEUNG CHI HUNG

RECORD PLAN

"THE WORKS SHOWN ON THESE PLANS ARE TYPE II WORKS (GENERAL BUILDING WORKS) IN RESPECT OF WHICH CONSENT IS APPLIED FOR THE PURPOSE OF FAST TRACK CONSENT APPLICATION UNDER REGULATION 33 OF THE BUILDING (ADMINISTRATION) REGULATIONS."

Li Kwok Hing
LI KWOK-HING
REGISTERED ARCHITECT,
AUTHORIZED PERSON (ARCHITECT)
AP (A) 39/95

A0 (1189mm x 841mm) Sheet Size

B.D. REF: 2/4096/13 (P)
F.S.D REF:

KEY PLAN

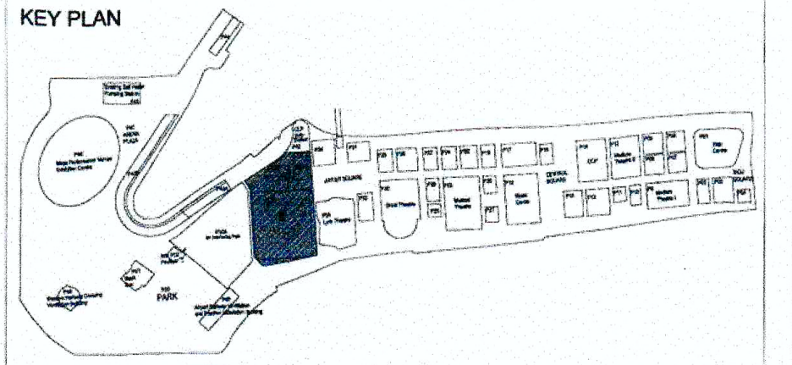

KEY PLAN

NOTES:

☐ PHASE 1
▨ PHASE 2

DAY 2 : FOR FUTURE CARRIAGEWAY PROVISIONS

Plan Approved
LI Ming-cham, Gordon
Senior Building Surveyor
for BUILDING AUTHORITY
-3 JUL 2020

UNLESS NOTED OTHERWISE, COPYRIGHT AND DESIGN RIGHTS IN THIS DOCUMENT ARE OWNED BY ONE OR ALL OF THE MEMBERS OF THE M+ CONSULTANCY JV FORMING THE "CONSULTANT". WITHOUT DEROGATION TO ANY PROVISION OF THE CONSULTANCY AGREEMENT, THE CONSULTANT, RESPECTIVELY THE MEMBER OF THE M+ CONSULTANCY JV THAT OWNS SUCH INTELLECTUAL PROPERTY, HAS GRANTED AND GRANTS ONLY TO THE AUTHORITY, ITS SUCCESSORS AND ASSIGNS A PERPETUAL, UNRESTRICTED, EXCLUSIVE, FREELY ASSIGNABLE AND IRREVOCABLE WORLD-WIDE LICENCE (CARRYING THE RIGHT TO GRANT SUB LICENSES) TO USE, REPRODUCE, MODIFY, ADAPT AND TRANSLATE THE INTELLECTUAL PROPERTY IN THIS DOCUMENT FOR ANY PURPOSE OF THE AUTHORITY. NOTWITHSTANDING THE ABOVE MENTIONED LICENCE, THIS DOCUMENT SHALL BE MODIFIED ADAPTED OR TRANSLATED ONLY BY THE MEMBER OF M+ CONSULTANCY JV INDICATED AS HAVING PRODUCED THIS DOCUMENT. THE USE OF THIS DOCUMENT AND THE INTELLECTUAL PROPERTY VESTED THEREIN BY ANY OTHER PARTY THAN THOSE MENTIONED ABOVE MUST BE SUBJECT TO AN AGREEMENT OR AUTHORIZATION BY OR WITH THE AUTHORITY

O	22.06.2020	GBP 16TH AMENDMENT	TFP
N	20.02.2020	GBP 15TH AMENDMENT	TFP
M	18.11.2019	GBP 14TH AMENDMENT	TFP
L	18.10.2019	GBP 13TH AMENDMENT	TFP
K	18.07.2019	GBP 12TH AMENDMENT	TFP
J	30.04.2019	GBP 11TH AMENDMENT	TFP
I	28.12.2017	GBP 8TH AMENDMENT	TFP
H	10.08.2017	GBP 7TH AMENDMENT	TFP
G	15.02.2017	GBP 6TH AMENDMENT	TFP
F	27.05.2016	GBP 5TH AMENDMENT	TFP
E	05.02.2016	GBP 4TH AMENDMENT	TFP
D	28.12.2015	GBP 3RD AMENDMENT	TFP
REV.	DATE	PURPOSE OF RELEASE	PRODUCED BY

CONSULTANT
M+ CONSULTANCY JV

DESIGN CONSULTANT
HERZOG & DE MEURON
HERZOG & DE MEURON BASEL LTD., RHEINSCHANZE 6, CH 4056
BASEL, SWITZERLAND

EXECUTIVE ARCHITECT
TFP | FARRELLS
TFP FARRELLS LIMITED, SUITES 1301-02, 13/F, 625 KING'S ROAD,
NORTH POINT, HONG KONG

ENGINEERING CONSULTANT
ARUP
OVE ARUP & PARTNERS HONG KONG LIMITED, LEVEL 5 FESTIVAL
WALK, 80 TAT CHEE AVENUE, KOWLOON TONG, HONG KONG.

MJV-SUBCONSULTANT

AUTHORITY'S CONSULTANT

QUANTITY SURVEYOR
LangdonSeah
威寧謝
AN ARCADIS COMPANY

JOB TITLE
MUSEUM PLUS (M+) OF THE
WEST KOWLOON CULTURAL
DISTRICT

DRAWING TITLE
B1/F PLAN (2 OF 2)

SCALE	1:200 [@ A0]	PRINTED	22.06.2020
CHECKED	DL	DATE	22.06.2020
APPROVED	FL	DATE	22.06.2020
PRODUCED BY	KL	DATE	22.06.2020

AUTHOR TFP
DISCIPLINE ARC
PHASE GBP
DRAWING NO. 3AXXX-TFP-ARC-DWG-0992-P00-LB01-GBP
REV. O
CAD REF NAME: 3AXXX-TFP-ARC-DWG-0992-P00-LB01-GBP-O.dwg
AUTHORITY
westKowloon
西九文化區