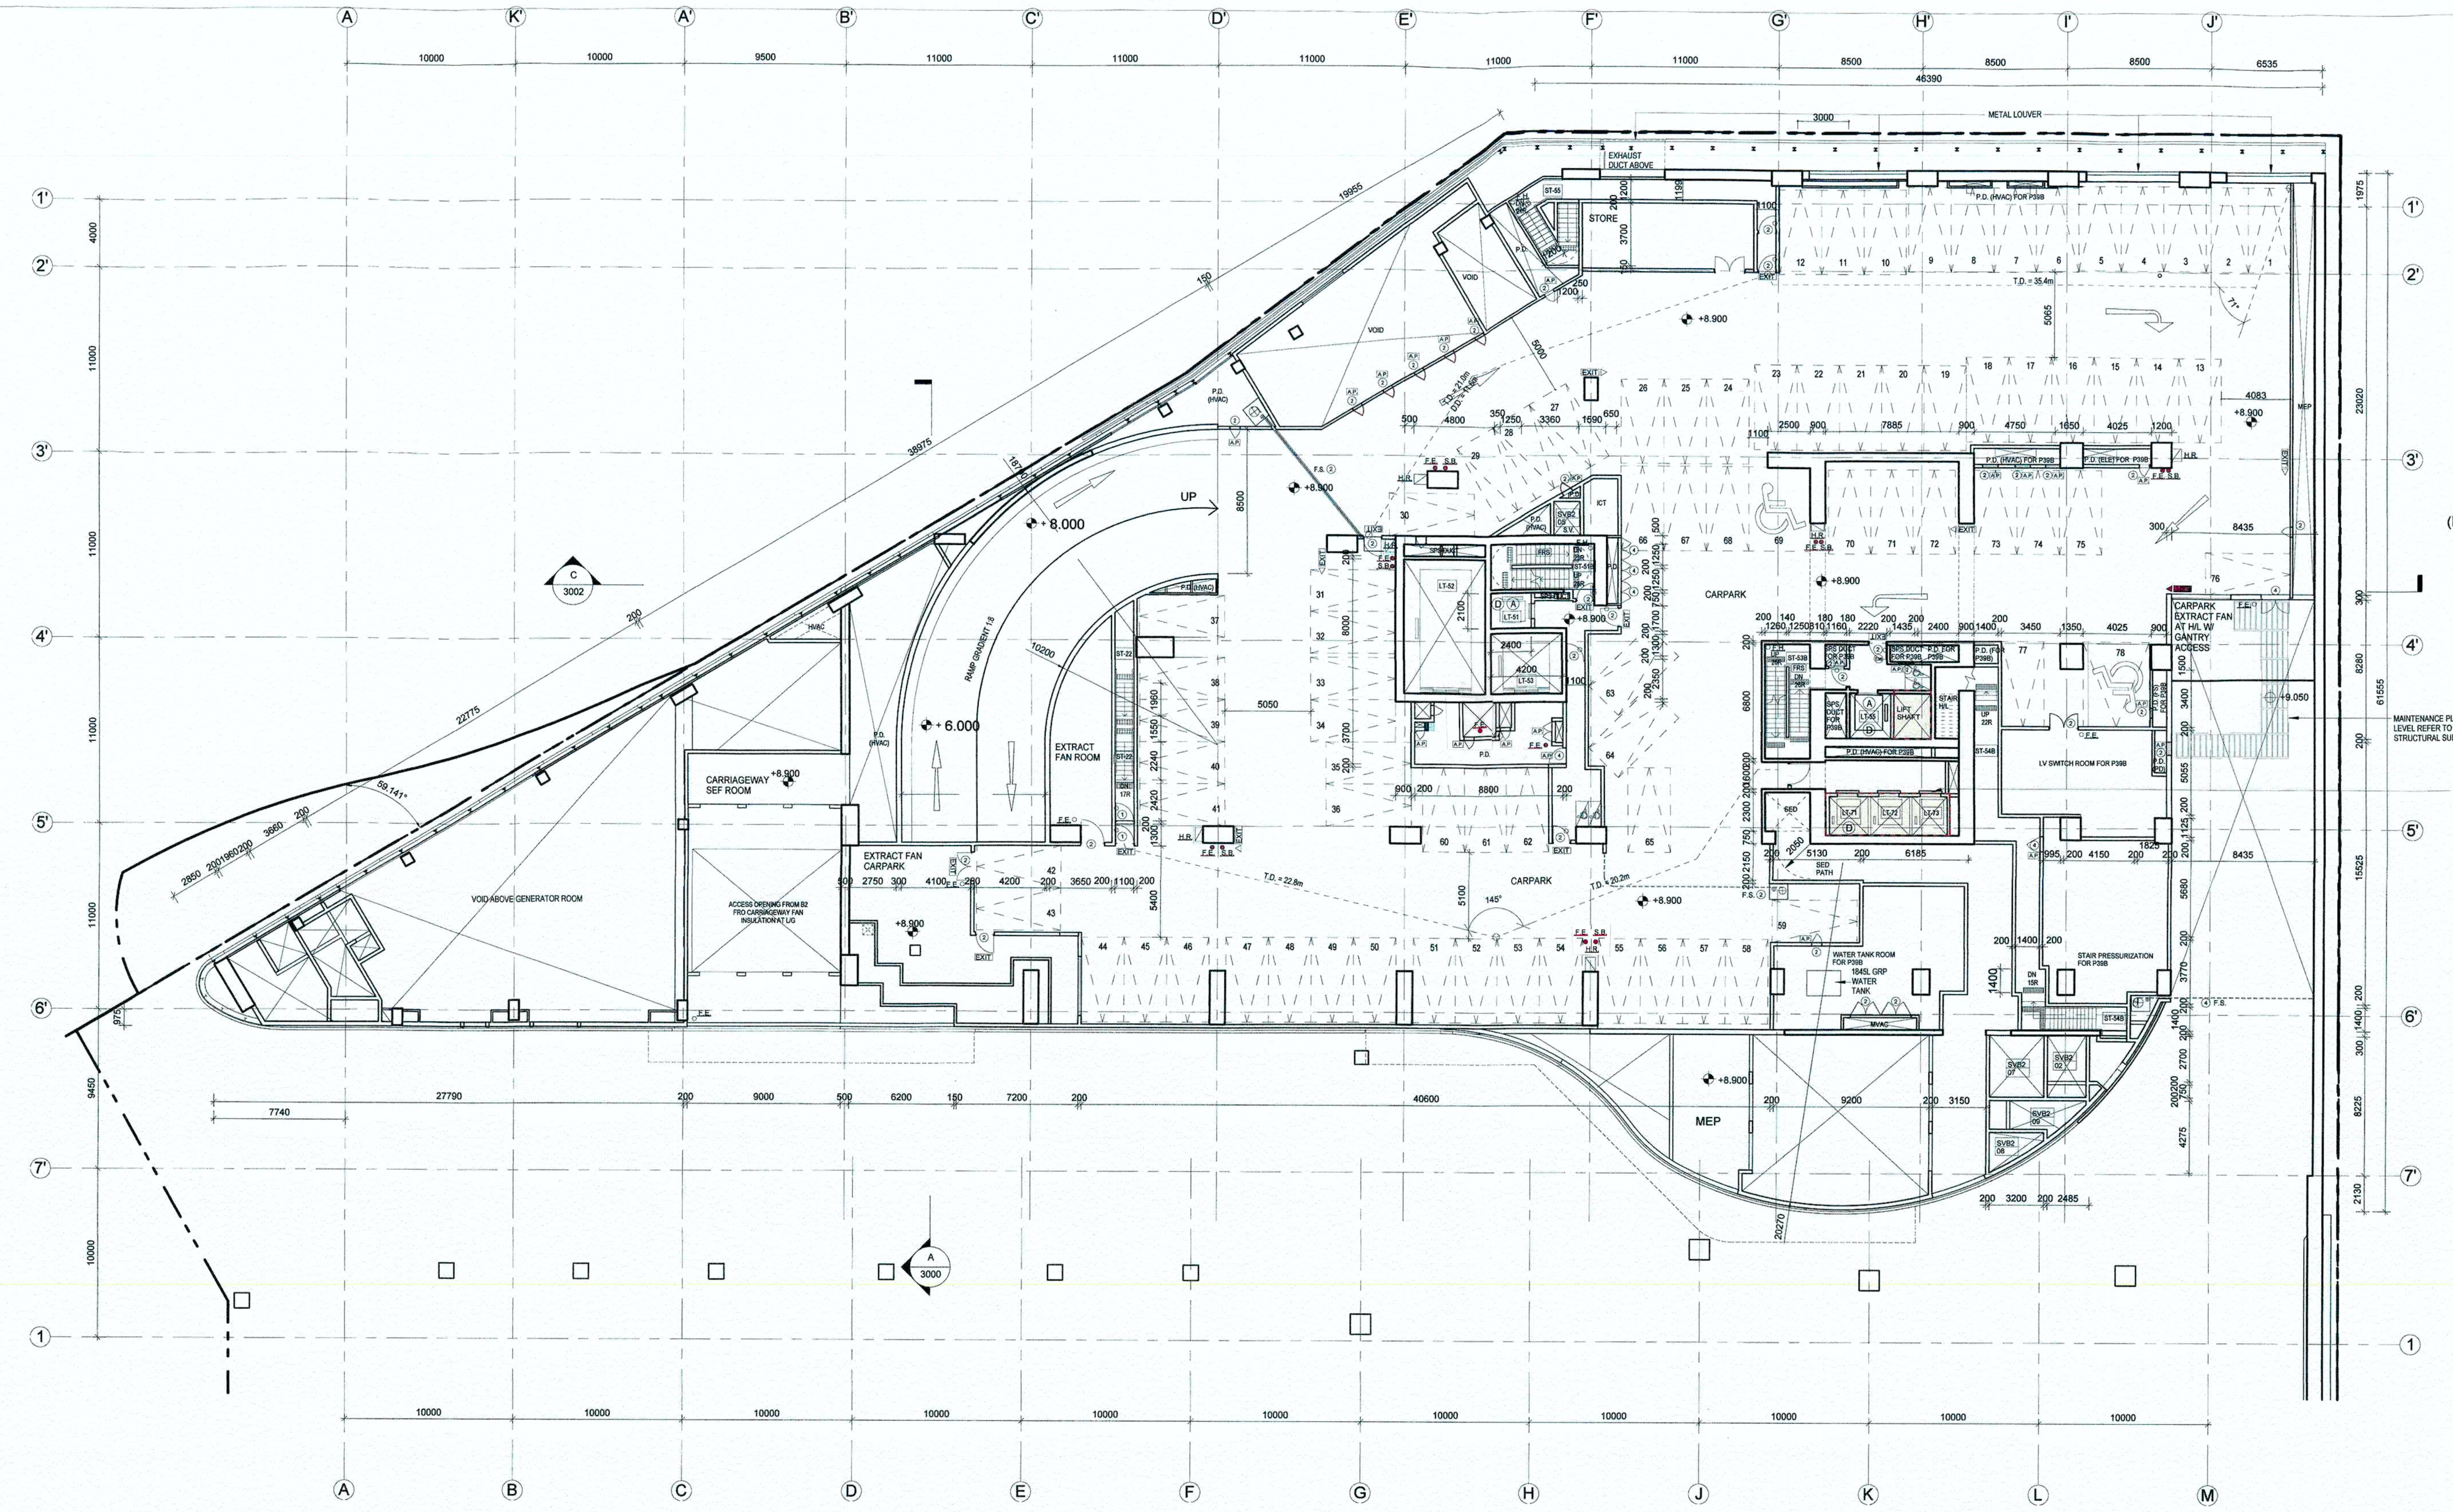
CARPARK
EXTRACT FAN CARPARK
EXTRACT FAN ROOM
CARRIAGEWAY SEF ROOM
VOID ABOVE GENERATOR ROOM
STORE
VOID
EXHAUST DUCT ABOVE
METAL LOUVER
UP
RAMP
+8.900
+8.000
+6.000
+9.050
WATER TANK ROOM
LV SWITCH ROOM
STAIR PRESSURISATION
CARPARK EXTRACT FAN AT HL W/ GANTRY ACCESS
MEP
EXIT
MAINTENANCE PLATFORM AT HIGH LEVEL REFER TO SEPARATE STRUCTURAL SUBMISSION

NO. OF CARPARK AT LG/F : 78
(IN WHICH 2 NOS. FOR DISABLED)

FRR -/240/240 TEMPORARY
SEPARATION TO BLOCK OUT
LT-71, 72 & 73 LIFT OPENING
PHASE 1 OP;
AND TO BE REMOVED FOR PHASE
2 OP INSPECTION.

LG/F PLAN
1 : 200

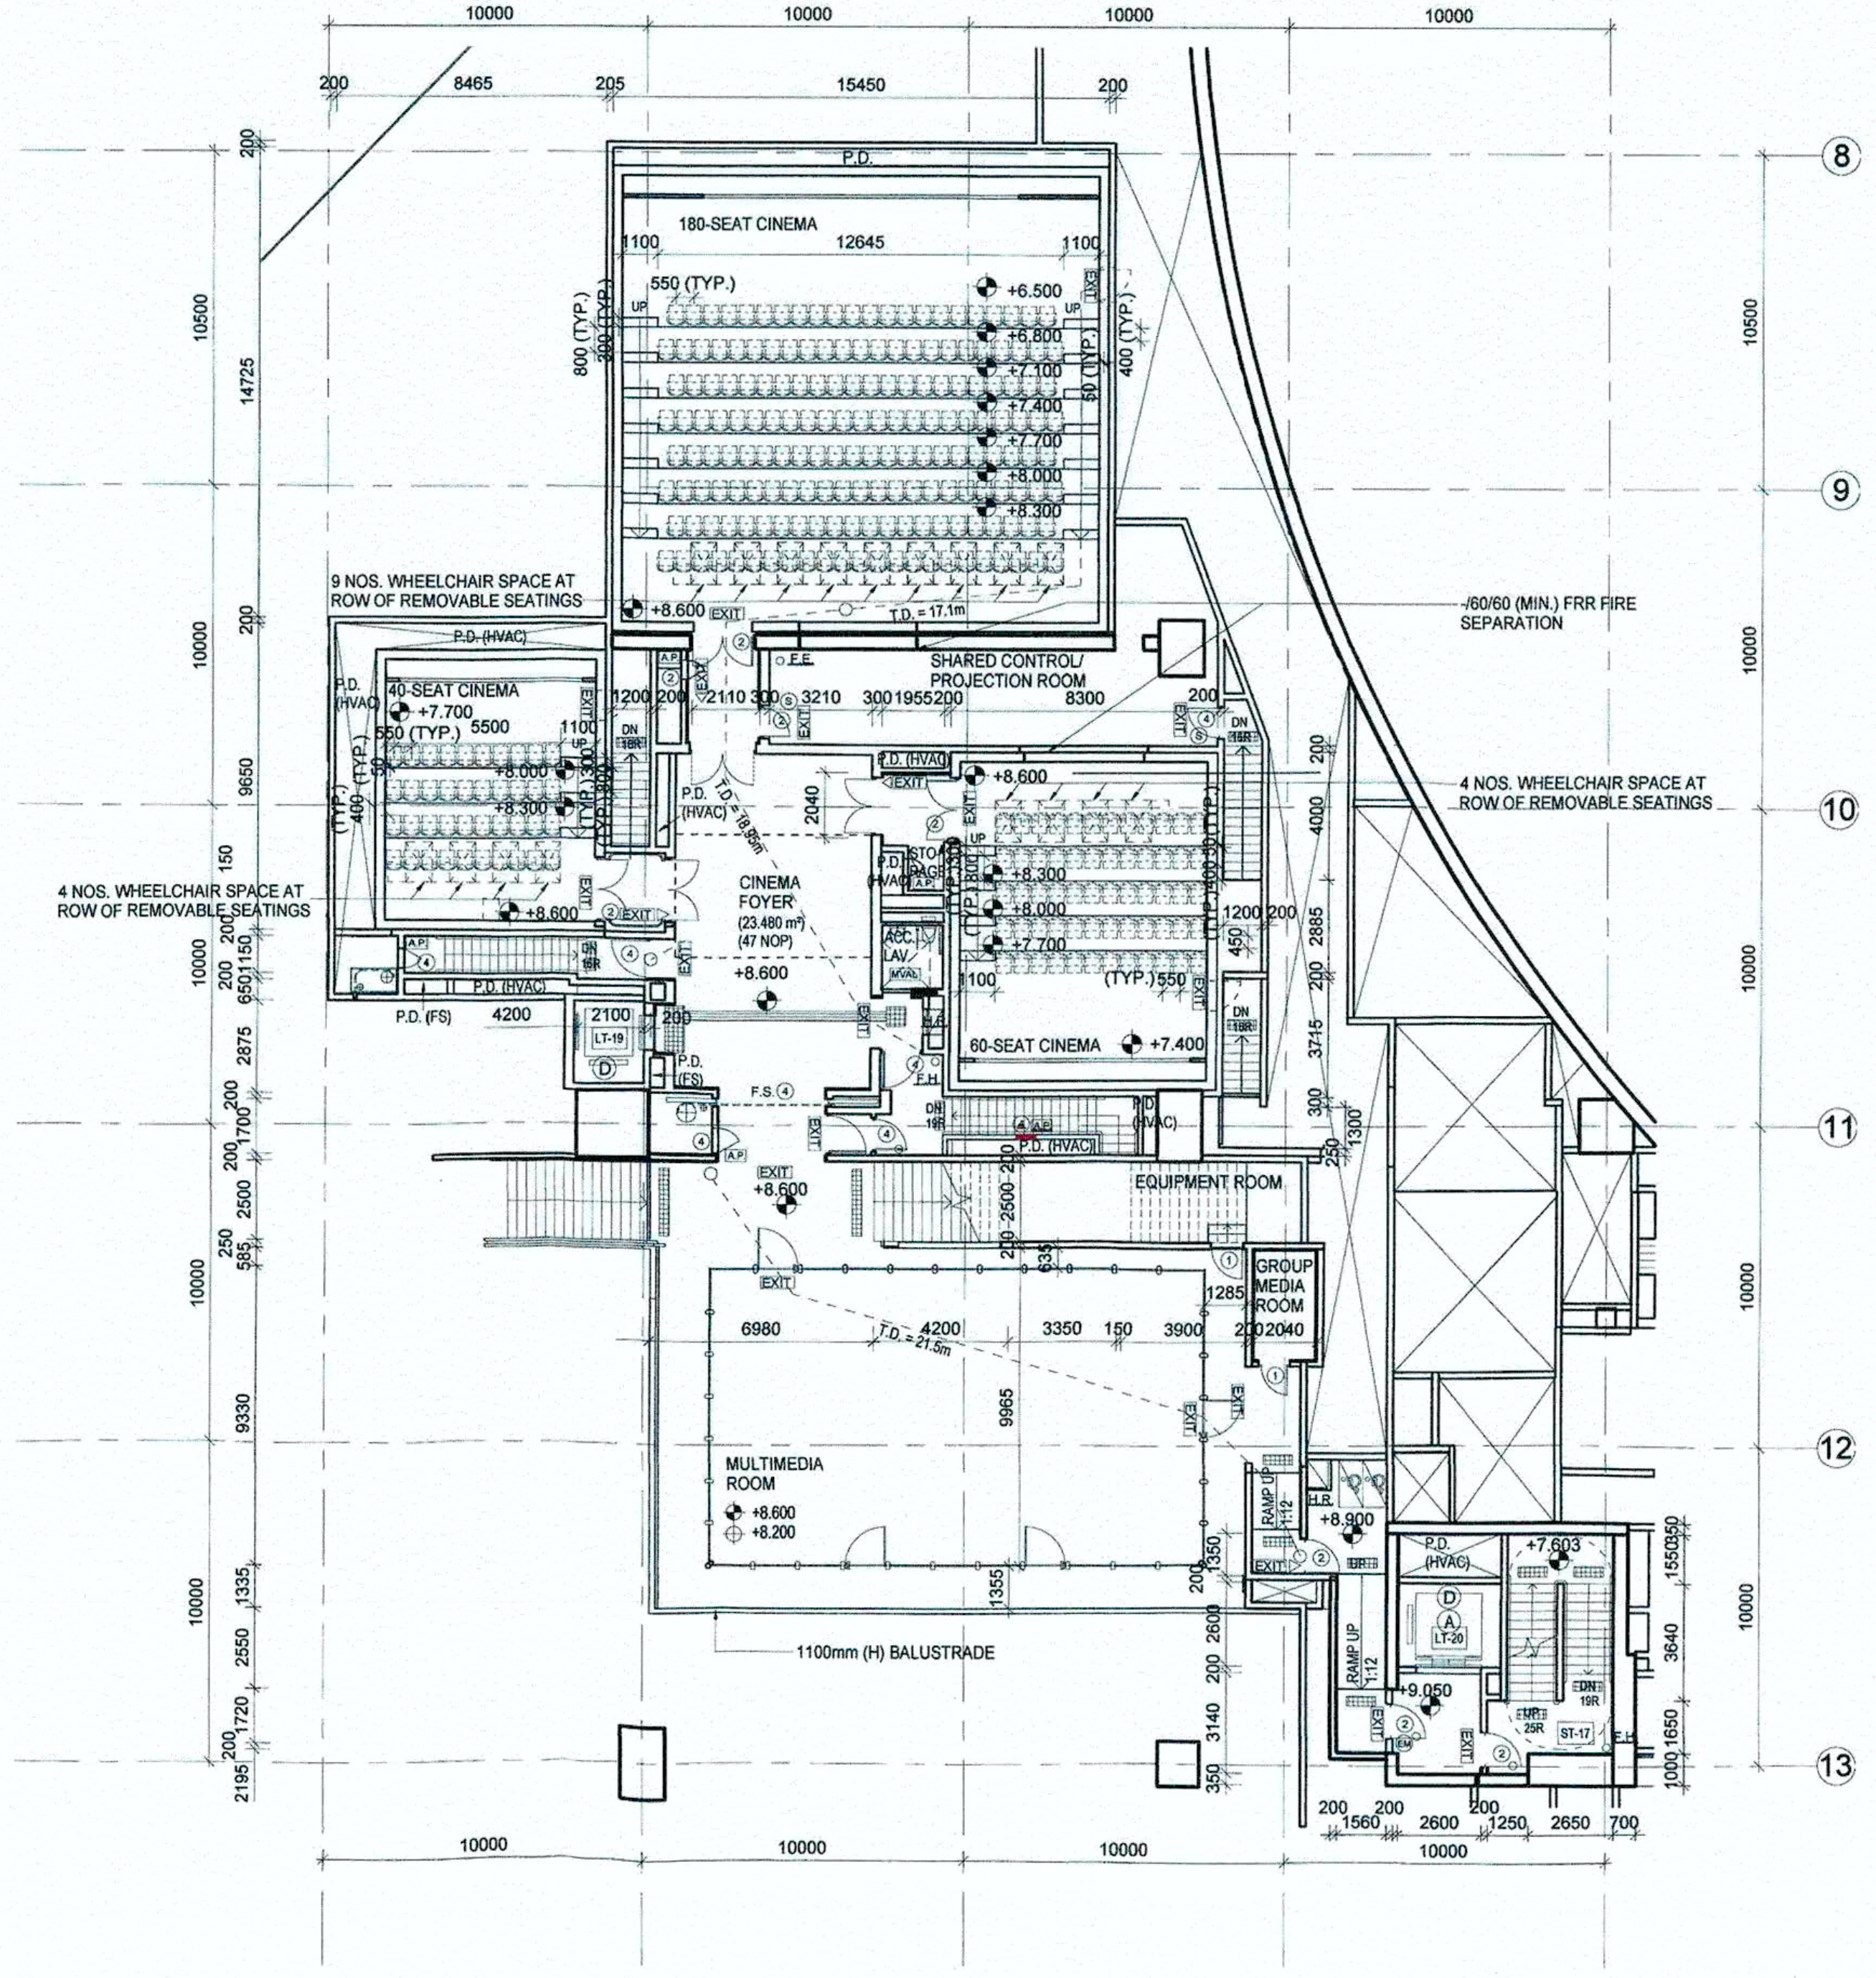
180-SEAT CINEMA
60-SEAT CINEMA
60-SEAT CINEMA
CINEMA FOYER
SHARED CONTROL/ PROJECTION ROOM
EQUIPMENT ROOM
GROUP MEDIA ROOM
MULTIMEDIA ROOM
9 NOS. WHEELCHAIR SPACE AT ROW OF REMOVABLE SEATINGS
4 NOS. WHEELCHAIR SPACE AT ROW OF REMOVABLE SEATINGS
4 NOS. WHEELCHAIR SPACE AT ROW OF REMOVABLE SEATINGS
-/60/60 (MIN.) FRR FIRE SEPARATION
1100mm (H) BALUSTRADE
+8.600
+7.700
+6.500
+8.200
+8.050

LG/F PART PLAN AT +8.6mPD
1 : 200

A0 (1188mm x 840mm) Sheet Size

RECEIVED BY
2020 JUN 23 P 5:05
R.4.D. Registry (NDs)
BUILDINGS DEPARTMENT

B.D. REF: 2/4096/13 (P)
F.S.D REF:

KEY PLAN

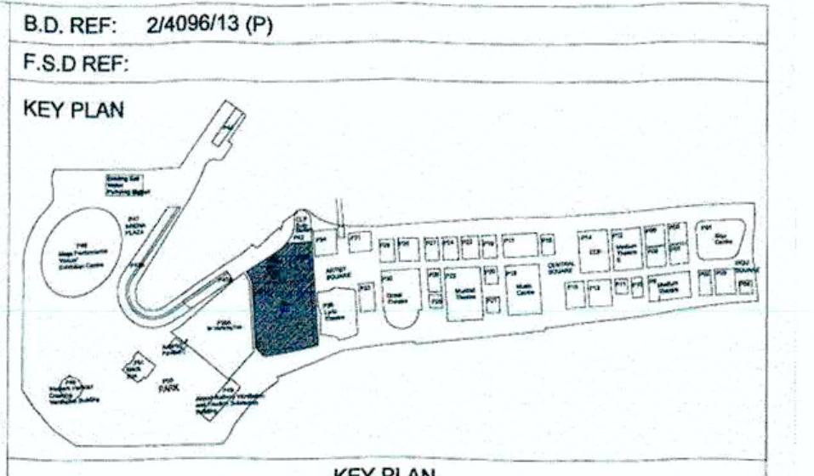

KEY PLAN

NOTES:

☐ PHASE 1
☐ PHASE 2

Plan Approved
LI Ming-chan, Gordon
Senior Building Surveyor
for BUILDING AUTHORITY
-3 JUL 2020

UNLESS NOTED OTHERWISE, COPYRIGHT AND DESIGN RIGHTS IN THIS DOCUMENT ARE OWNED BY ONE OR ALL OF THE MEMBERS OF THE M+ CONSULTANCY JV FORMING THE "CONSULTANT". WITHOUT DEROGATION TO ANY PROVISION OF THE CONSULTANCY AGREEMENT, THE CONSULTANT, RESPECTIVELY THE MEMBER OF THE M+ CONSULTANCY JV THAT OWNS SUCH INTELLECTUAL PROPERTY, HAS GRANTED AND GRANTS ONLY TO THE AUTHORITY, ITS SUCCESSORS AND ASSIGNS A PERPETUAL, UNRESTRICTED, EXCLUSIVE, FREELY ASSIGNABLE AND IRREVOCABLE WORLD-WIDE LICENCE (CARRYING THE RIGHT TO GRANT SUB LICENSES) TO USE, REPRODUCE, MODIFY, ADAPT AND TRANSLATE THE INTELLECTUAL PROPERTY IN THIS DOCUMENT FOR ANY PURPOSE OF THE AUTHORITY. NOTWITHSTANDING THE ABOVE MENTIONED LICENCE, THIS DOCUMENT SHALL BE MODIFIED ADAPTED OR TRANSLATED ONLY BY THE MEMBER OF M+ CONSULTANCY JV INDICATED AS HAVING PRODUCED THIS DOCUMENT. THE USE OF THIS DOCUMENT AND THE INTELLECTUAL PROPERTY VESTED THEREIN BY ANY OTHER PARTY THAN THOSE MENTIONED ABOVE MUST BE SUBJECT TO AN AGREEMENT OR AUTHORIZATION BY OR WITH THE AUTHORITY

REV.	DATE	PURPOSE OF RELEASE	PRODUCED BY
O	22.06.2020	GBP 16TH AMENDMENT	TFP
N	20.02.2020	GBP 15TH AMENDMENT	TFP
M	18.11.2019	GBP 14TH AMENDMENT	TFP
L	18.10.2019	GBP 13TH AMENDMENT	TFP
K	18.07.2019	GBP 12TH AMENDMENT	TFP
J	30.04.2019	GBP 11TH AMENDMENT	TFP
I	28.12.2017	GBP 8TH AMENDMENT	TFP
H	10.08.2017	GBP 7TH AMENDMENT	TFP
G	15.02.2017	GBP 6TH AMENDMENT	TFP
F	27.05.2016	GBP 5TH AMENDMENT	TFP
E	05.02.2016	GBP 4TH AMENDMENT	TFP
D	28.12.2015	GBP 3RD AMENDMENT	TFP

CONSULTANT
M+ CONSULTANCY JV

DESIGN CONSULTANT
HERZOG & DE MEURON
HERZOG & DE MEURON BASEL LTD., RHEINSCHANZE 6, CH 4056
BASEL, SWITZERLAND

EXECUTIVE ARCHITECT
TFP | FARRELLS
TFP FARRELLS LIMITED, SUITES 1301-02, 13/F, 625 KING'S ROAD,
NORTH POINT, HONG KONG

ENGINEERING CONSULTANT
ARUP
OVE ARUP & PARTNERS HONG KONG LIMITED, LEVEL 5 FESTIVAL
WALK, 80 TAT CHEE AVENUE, KOWLOON TONG, HONG KONG.

MJV-SUBCONSULTANT

AUTHORITY'S CONSULTANT

QUANTITY SURVEYOR
LangdonSeah
威寧謝
AN ARCADIS COMPANY

JOB TITLE
MUSEUM PLUS (M+) OF THE
WEST KOWLOON CULTURAL
DISTRICT

DRAWING TITLE
LG/F PLAN

SCALE	1:200 [@ A0]	PRINTED	22.06.2020
CHECKED	DL	DATE	22.06.2020
APPROVED	FL	DATE	22.06.2020
PRODUCED BY	KL	DATE	22.06.2020

AUTHOR TFP
DISCIPLINE ARC
PHASE GBP

DRAWING NO.	REV.
3AXXX-TFP-ARC-DWG-0997-P00-LL00-GBP	O

CAD REF NAME: 3AXXX-TFP-ARC-DWG-0997-P00-LL00-GBP-O.dwg

AUTHORITY

westKowloon
西九文化區

Note: This plan has been processed on a curtailed check basis under the centralized processing system as promulgated in PNAP ADM-19. The duties of the authorized person, registered structural engineer and/or registered geotechnical engineer concerned as specified under section 4(3)(b) and the provision of section 14(2)(e) of the Buildings Ordinance are of particular relevance in this regard.

LEUNG CHI HUNG

"THE WORKS SHOWN ON THESE PLANS ARE TYPE II WORKS (GENERAL BUILDING WORKS) IN RESPECT OF WHICH CONSENT IS APPLIED FOR THE PURPOSE OF FAST TRACK CONSENT APPLICATION UNDER REGULATION 33 OF THE BUILDING (ADMINISTRATION) REGULATIONS."

Li Kwok-Hing
LI KWOK-HING
REGISTERED ARCHITECT,
AUTHORIZED PERSON (ARCHITECT)
AP (A) 39/95

RECORD PLAN